



Iso R+1

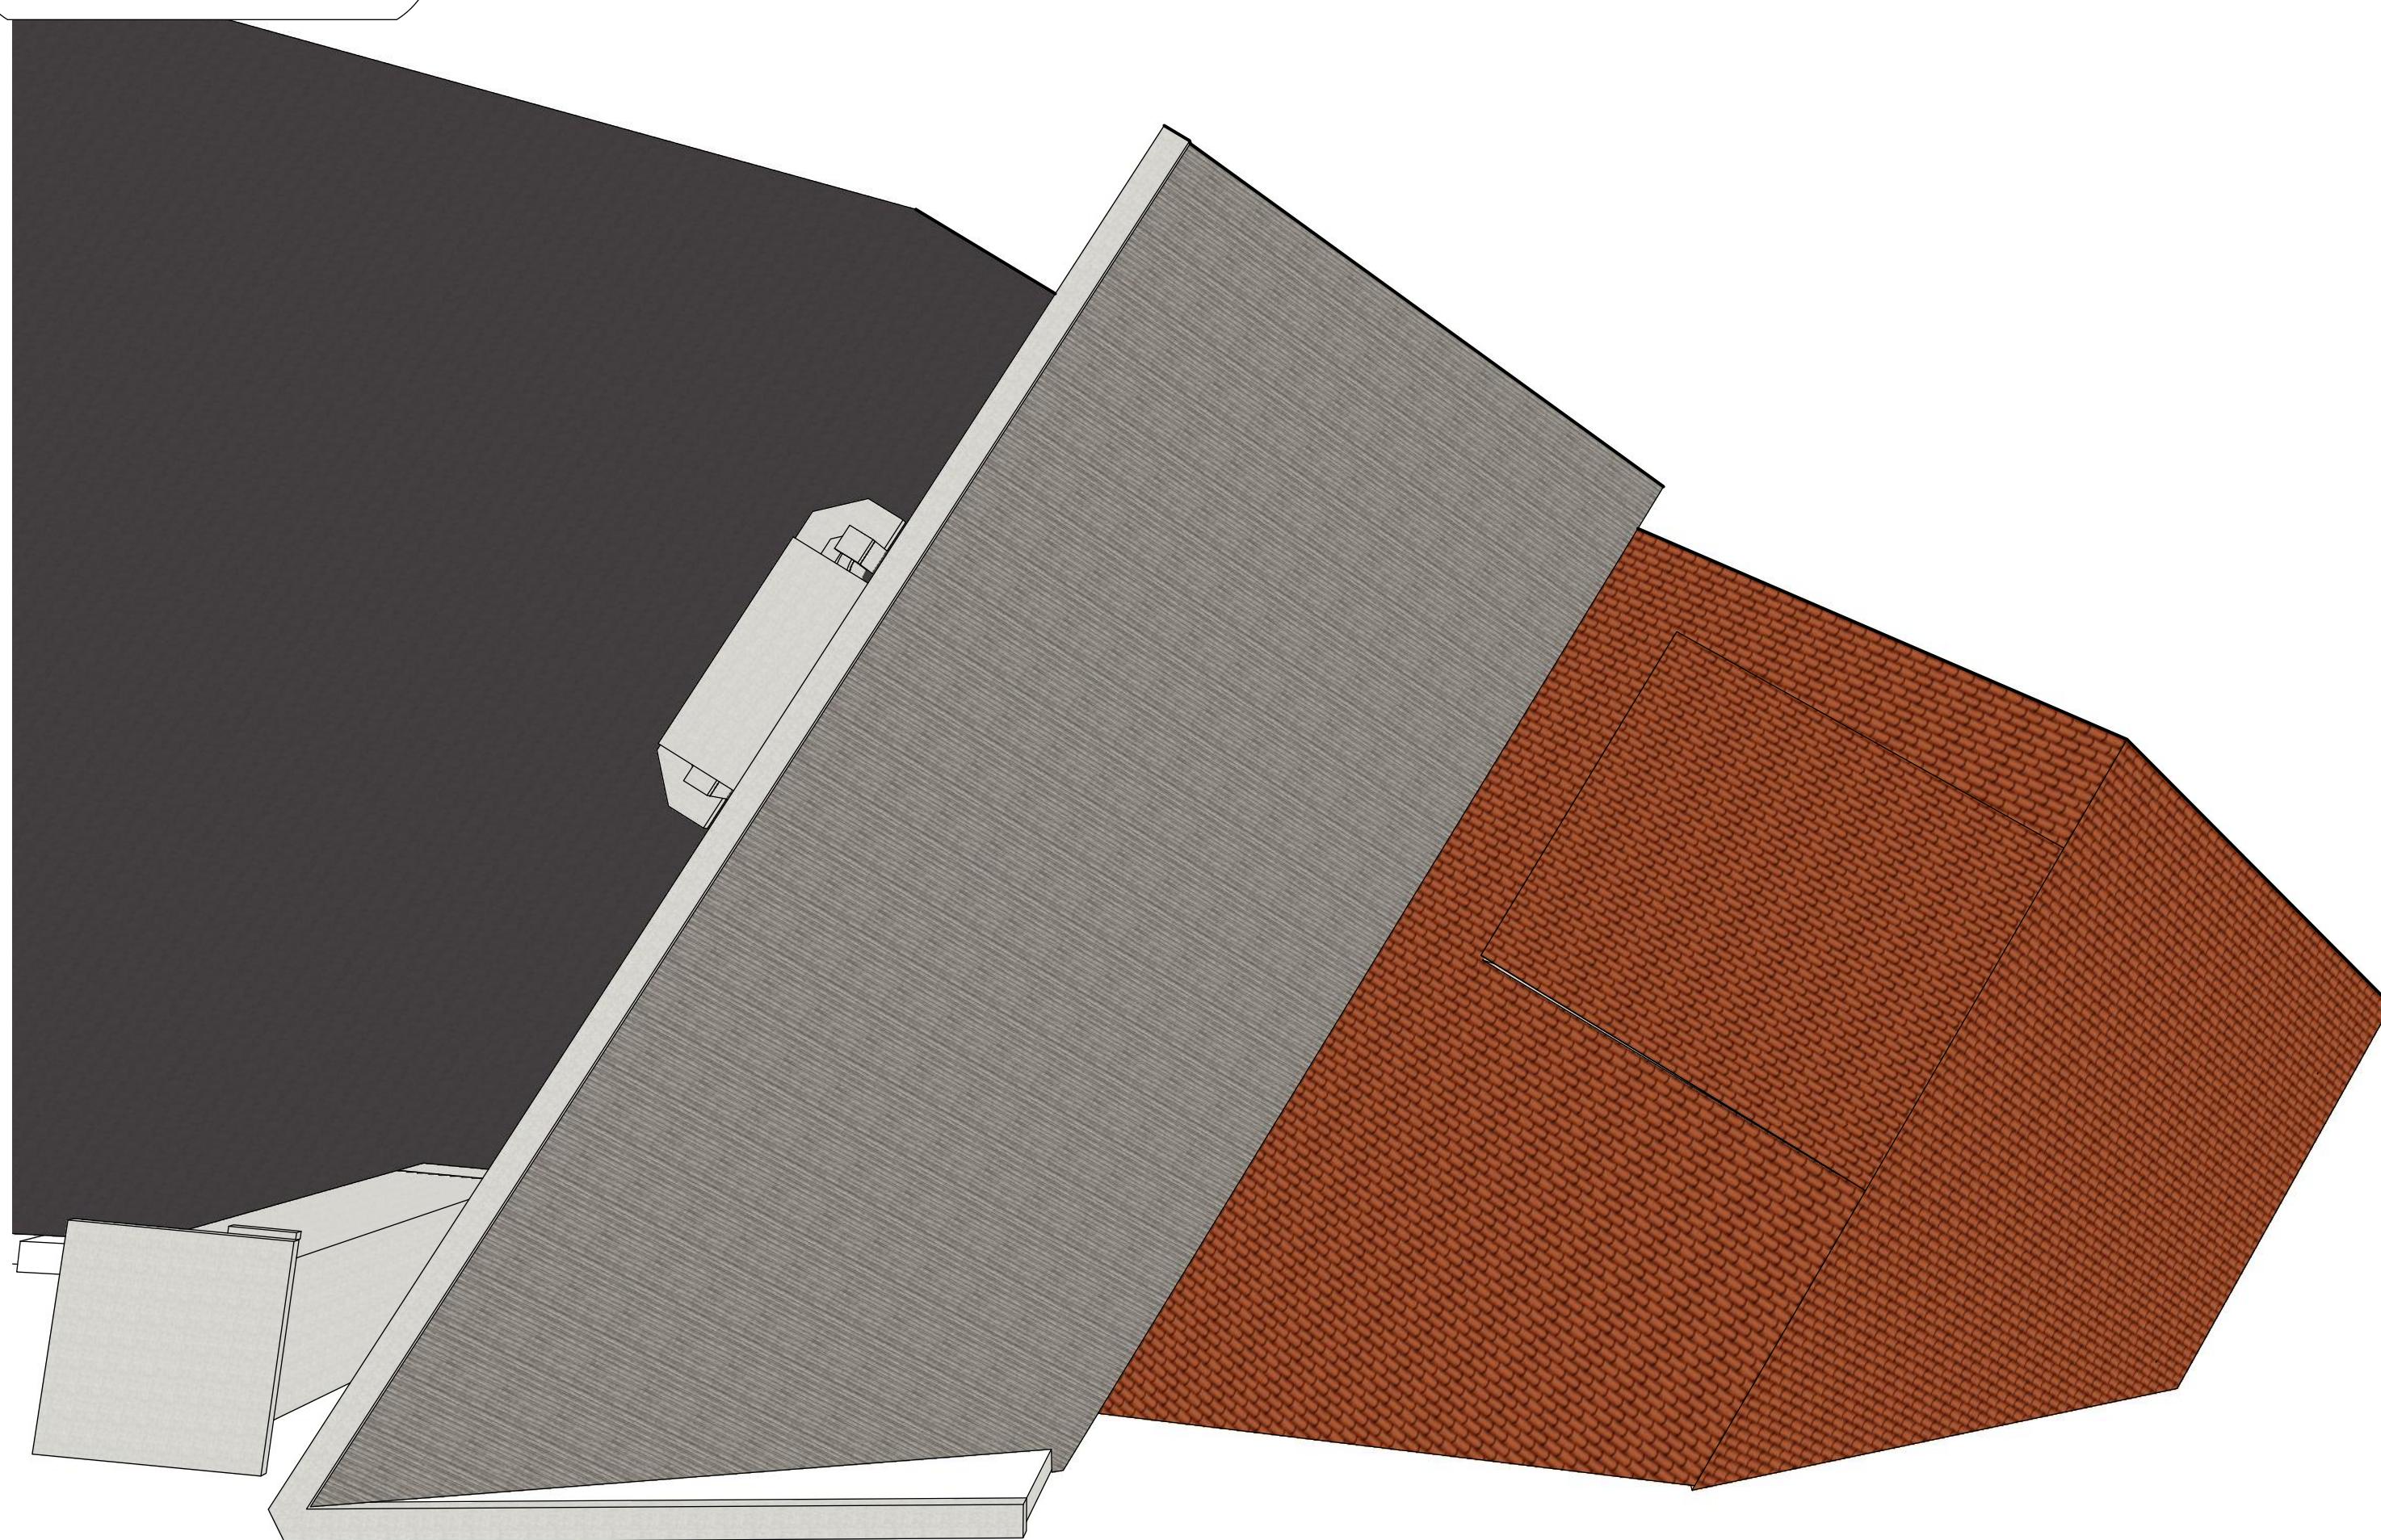

Façade Nord




Iso R 0

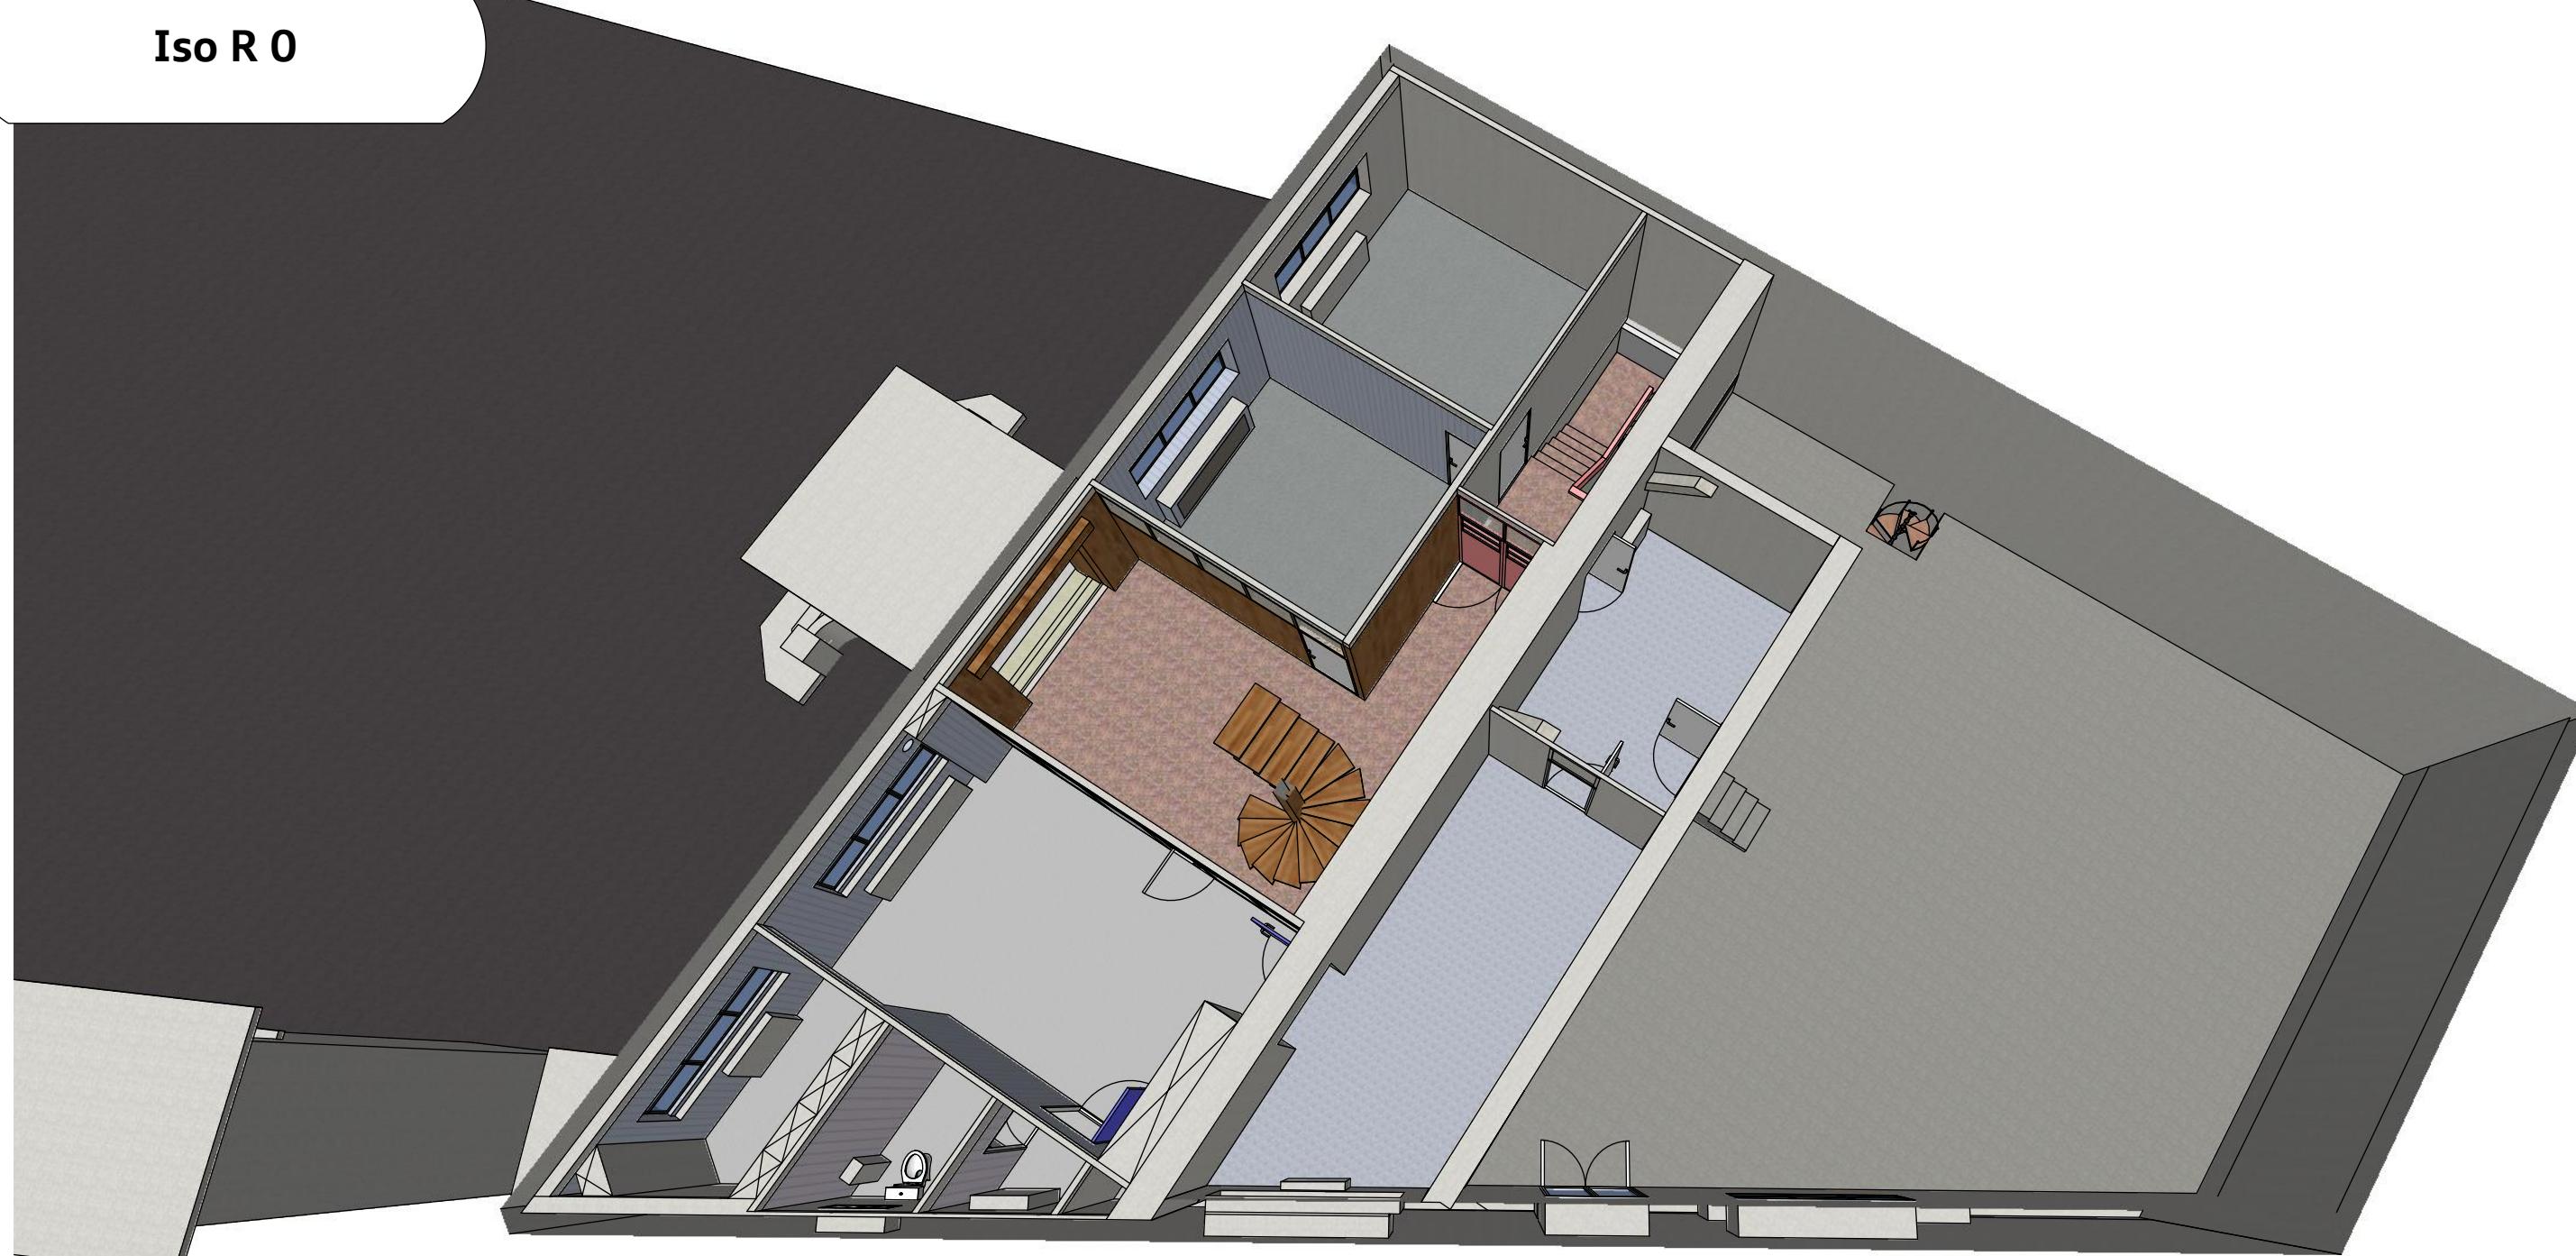

Façade Nord



Iso R-1

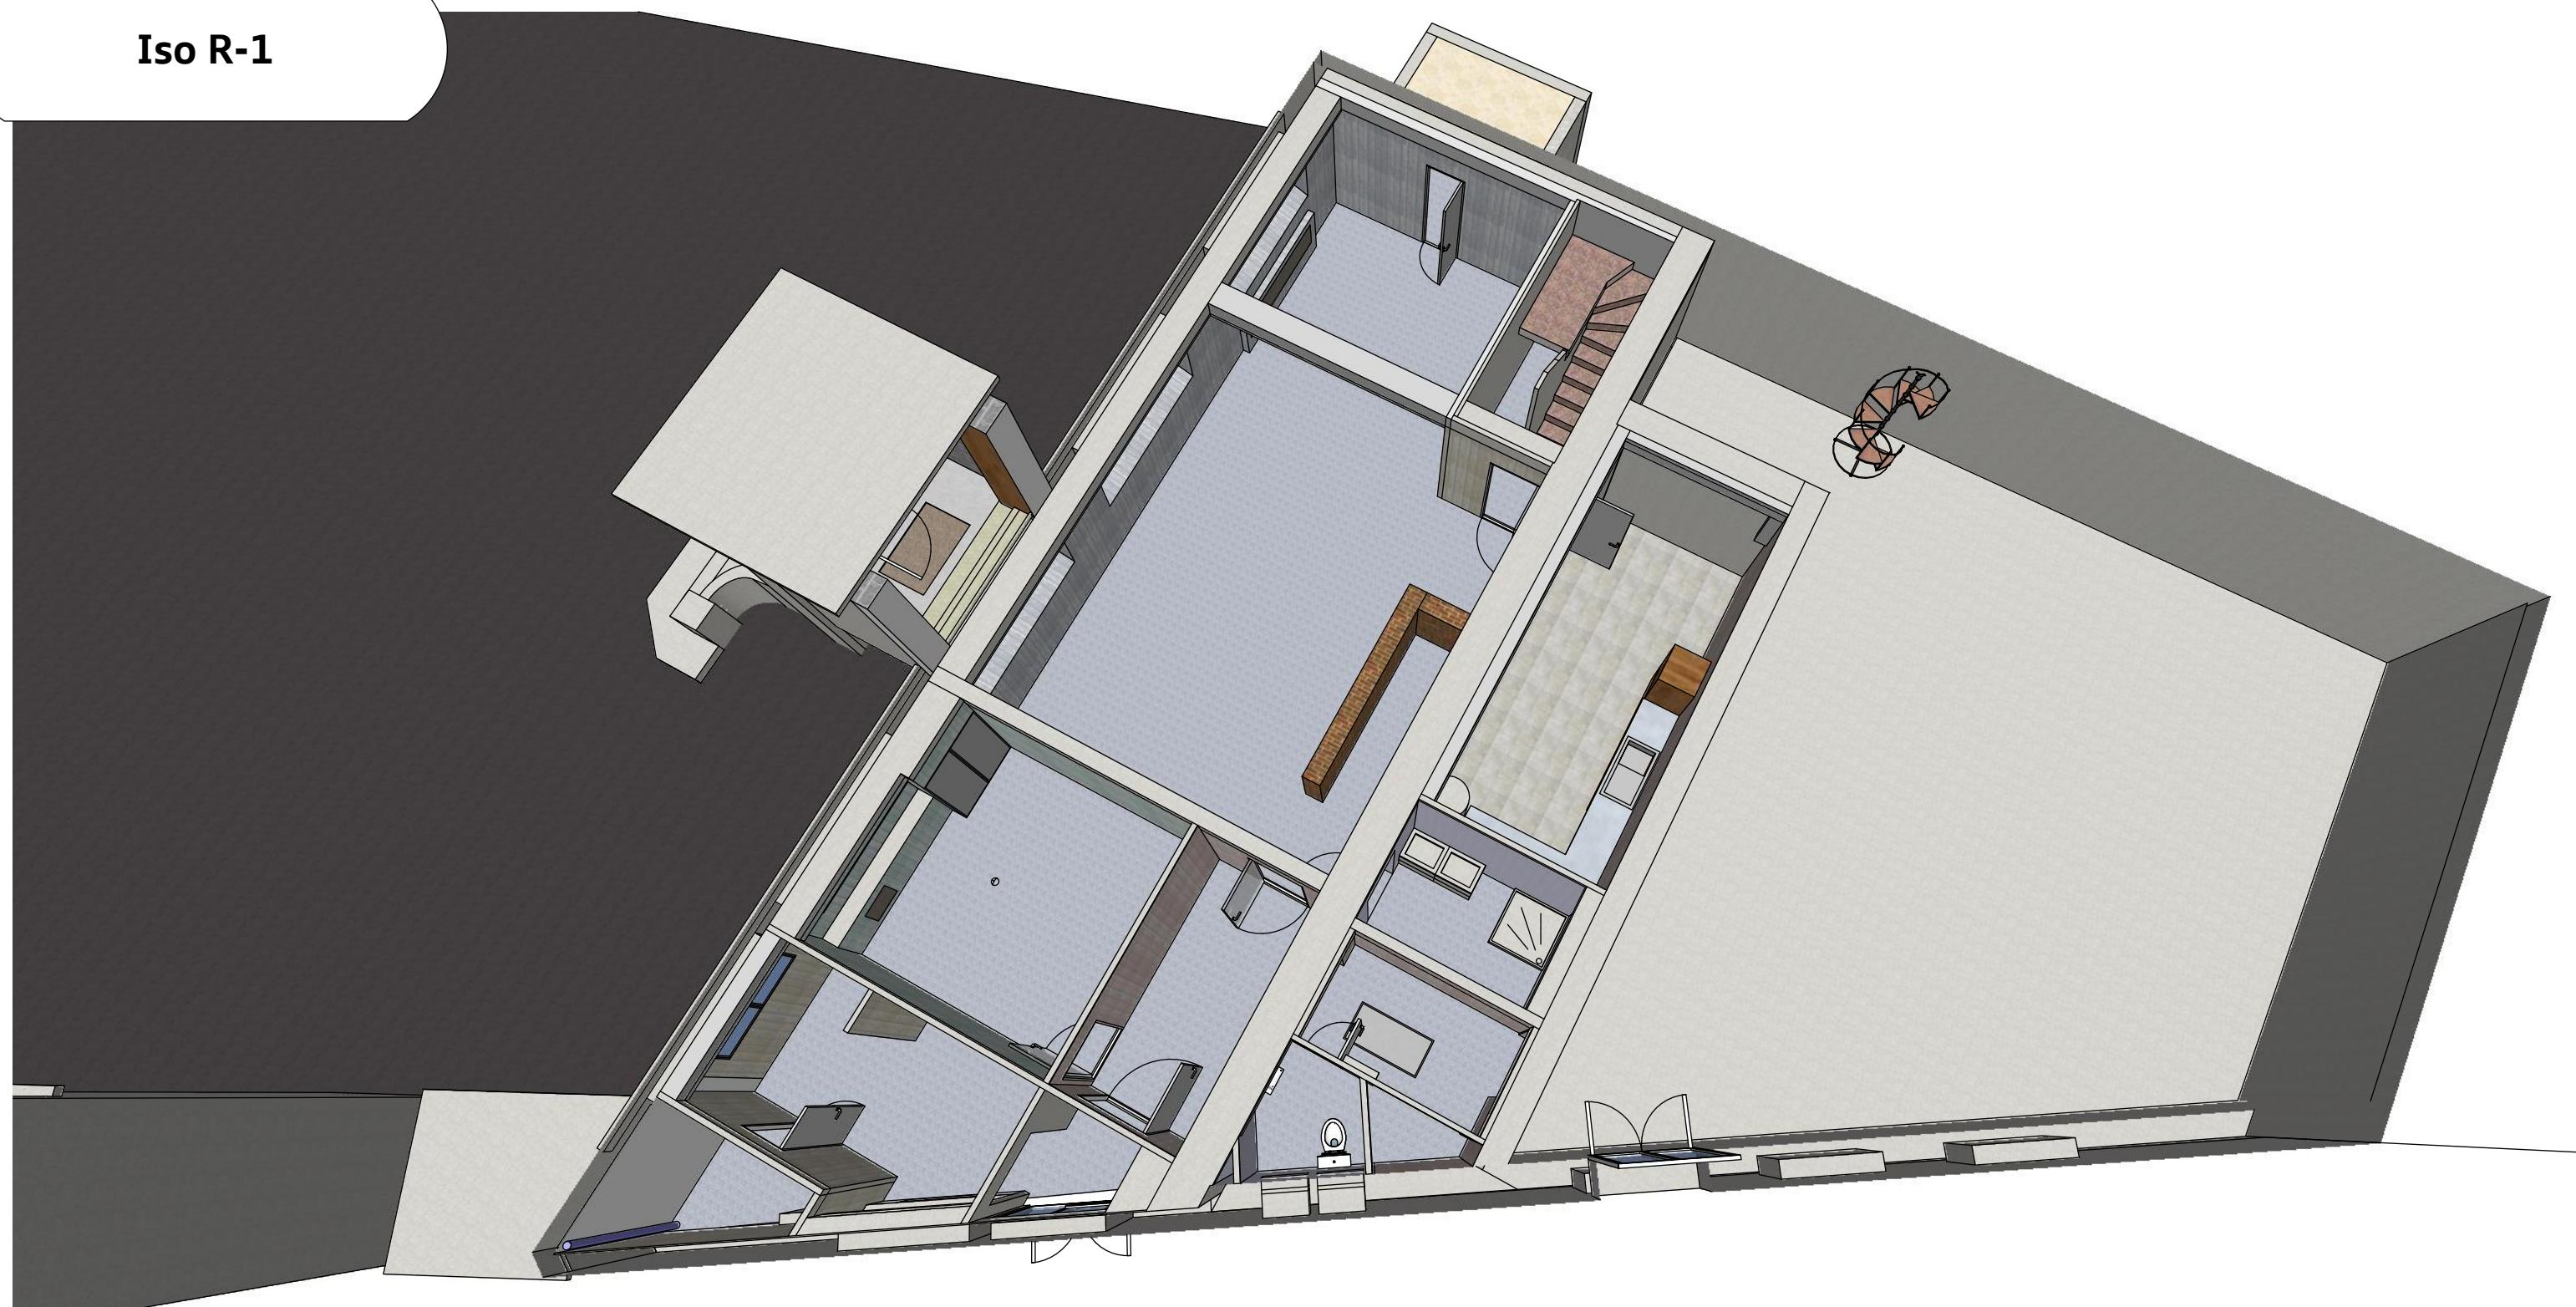

AP EI
ap.bureau.etude@gmail.com **1**


12-14 Rue de la Gare Le Méréville 91660
Résidence Le DUC d'Uber

Plan état existant - Localisation / Toitures / Iso
Echelle :

Dernière modification : 24/10/2023
Révision : v0.03



Voir le Bâtiment en 3D

An aerial map showing the location of the building. The map includes property boundaries, street names like 'Rue de la Gare Le Méréville', and house numbers. A QR code is provided for further information.

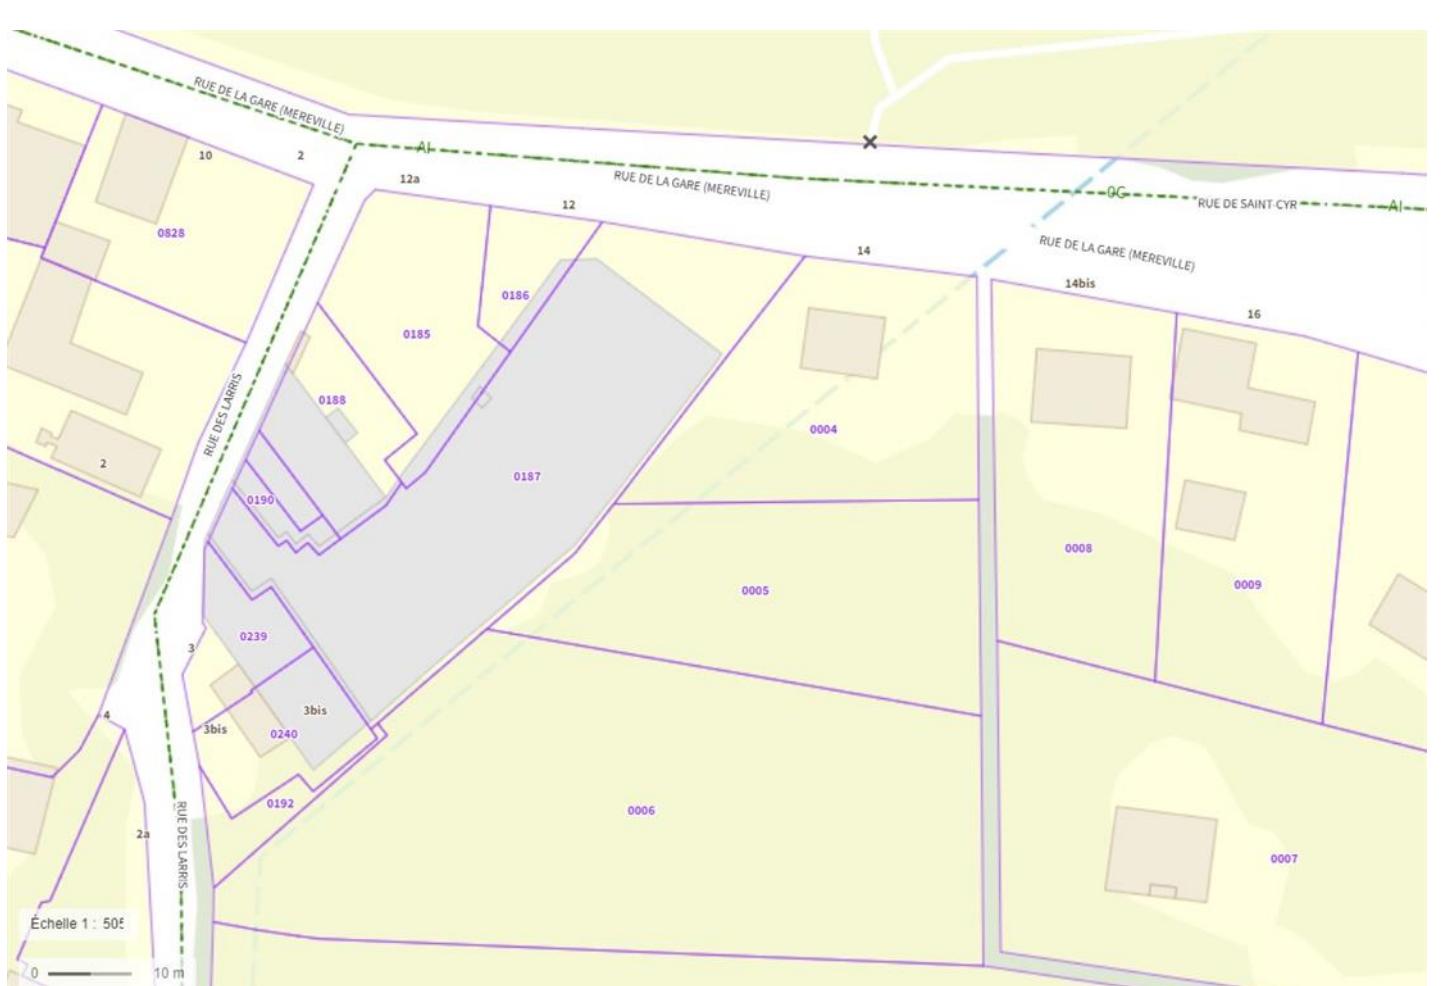

Façade Est
1/50


Façade Sud
1/50

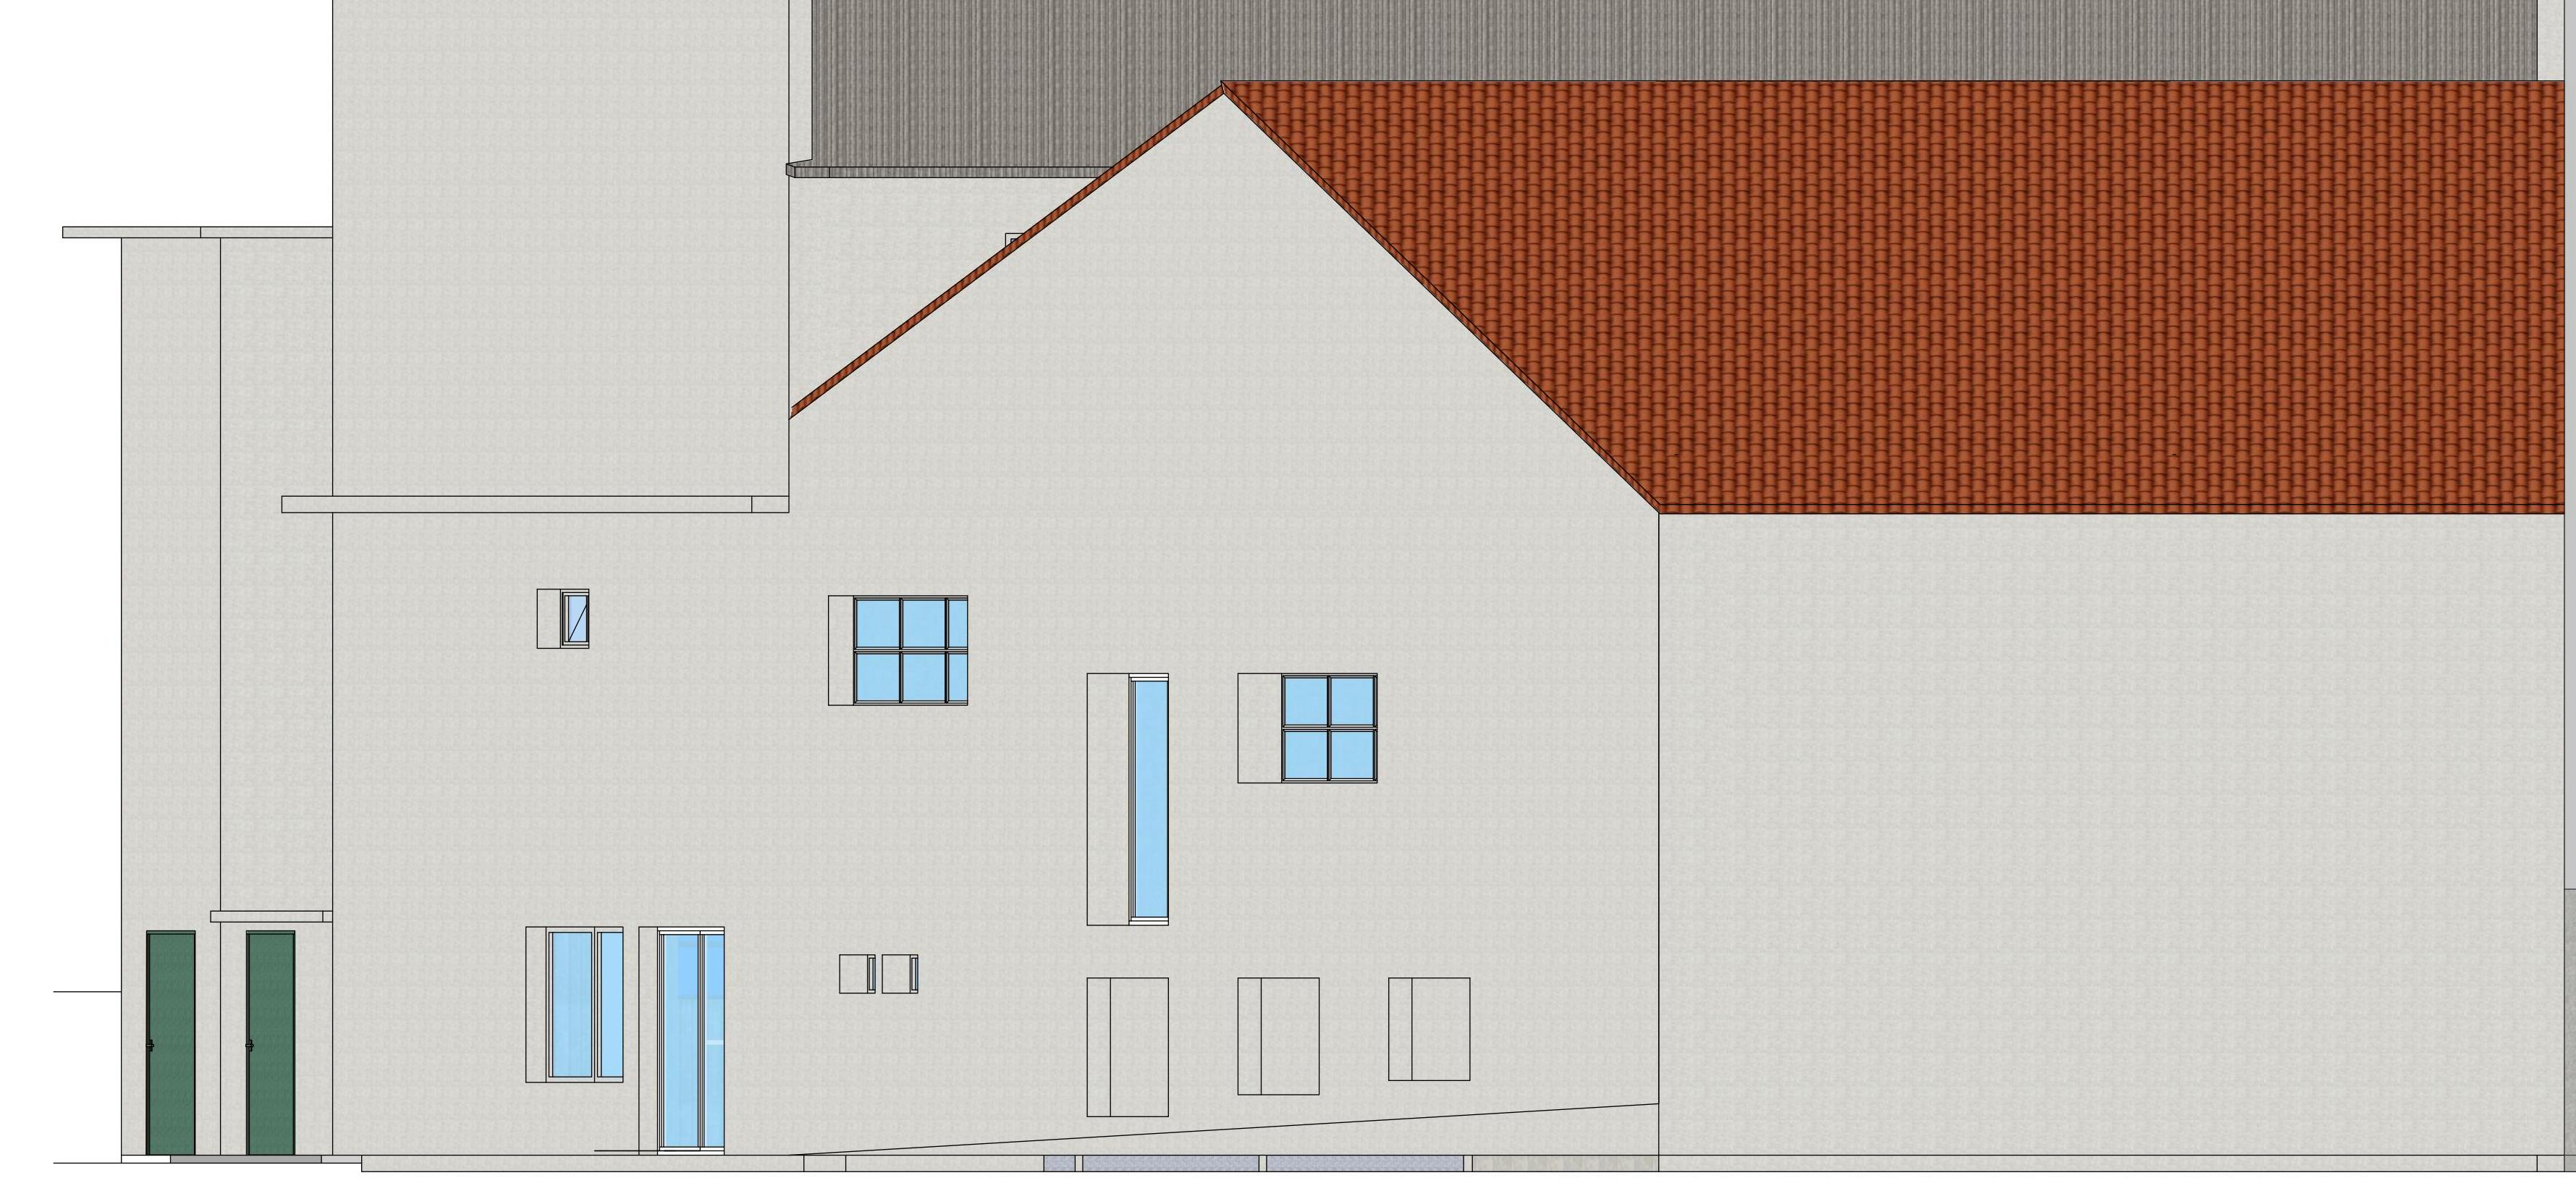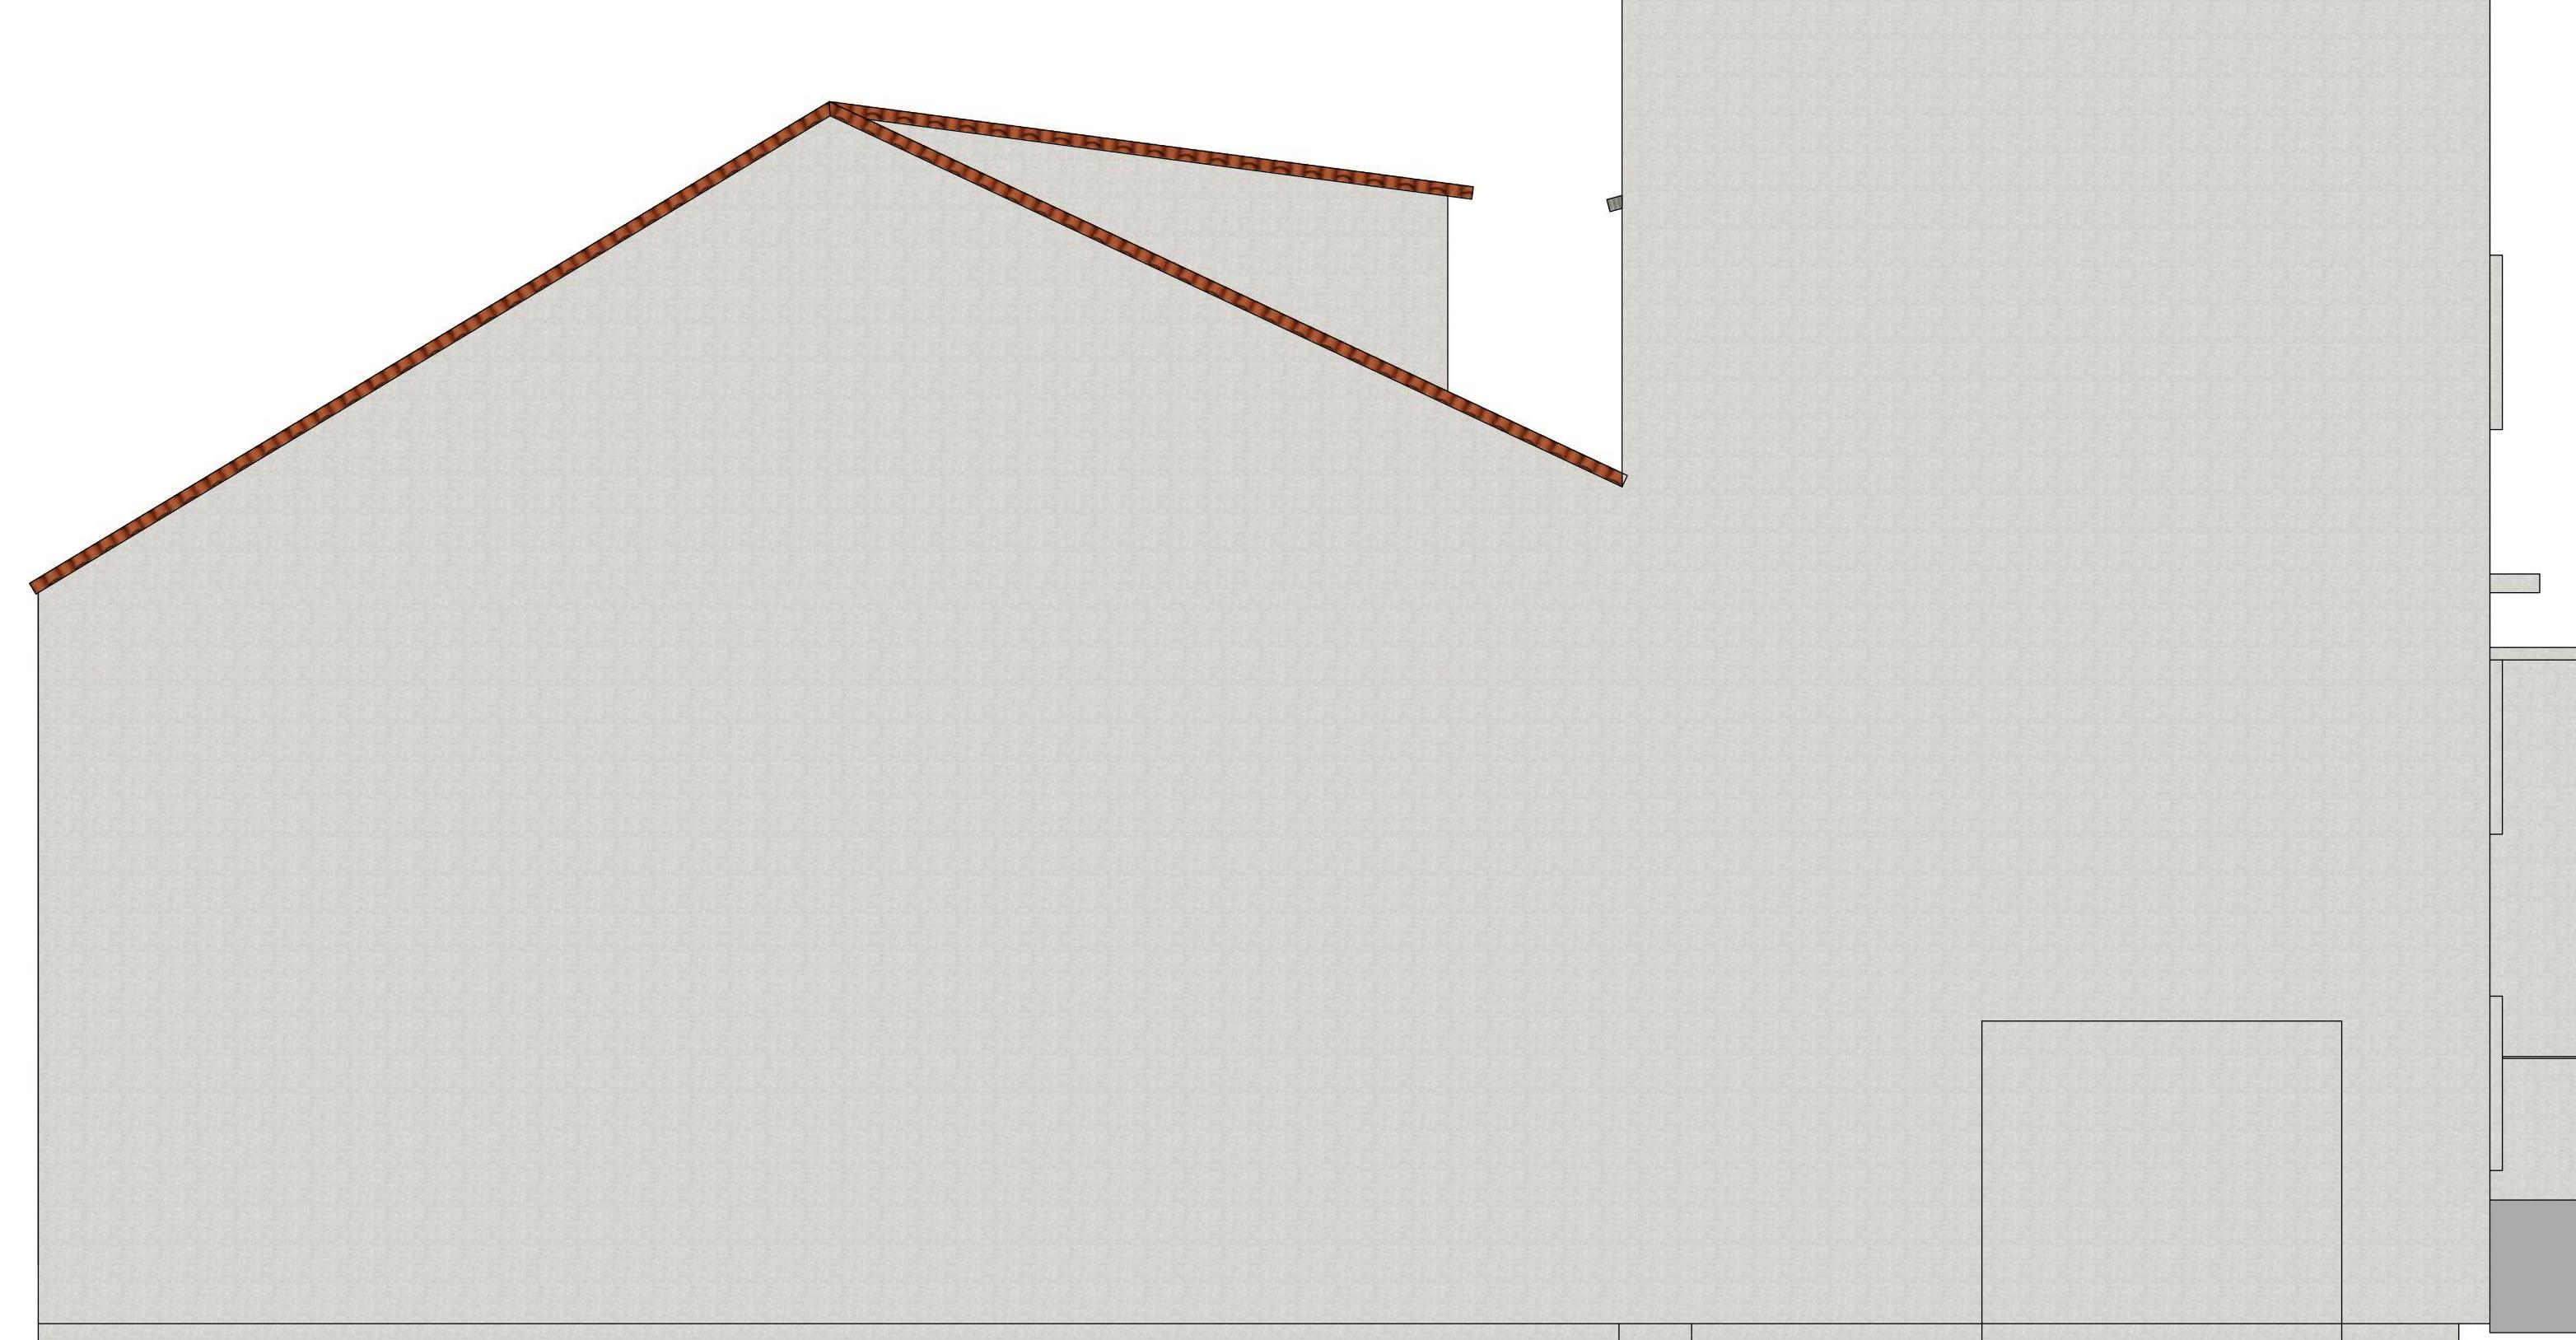

Façade Ouest
1/50



Façade Nord
1/50


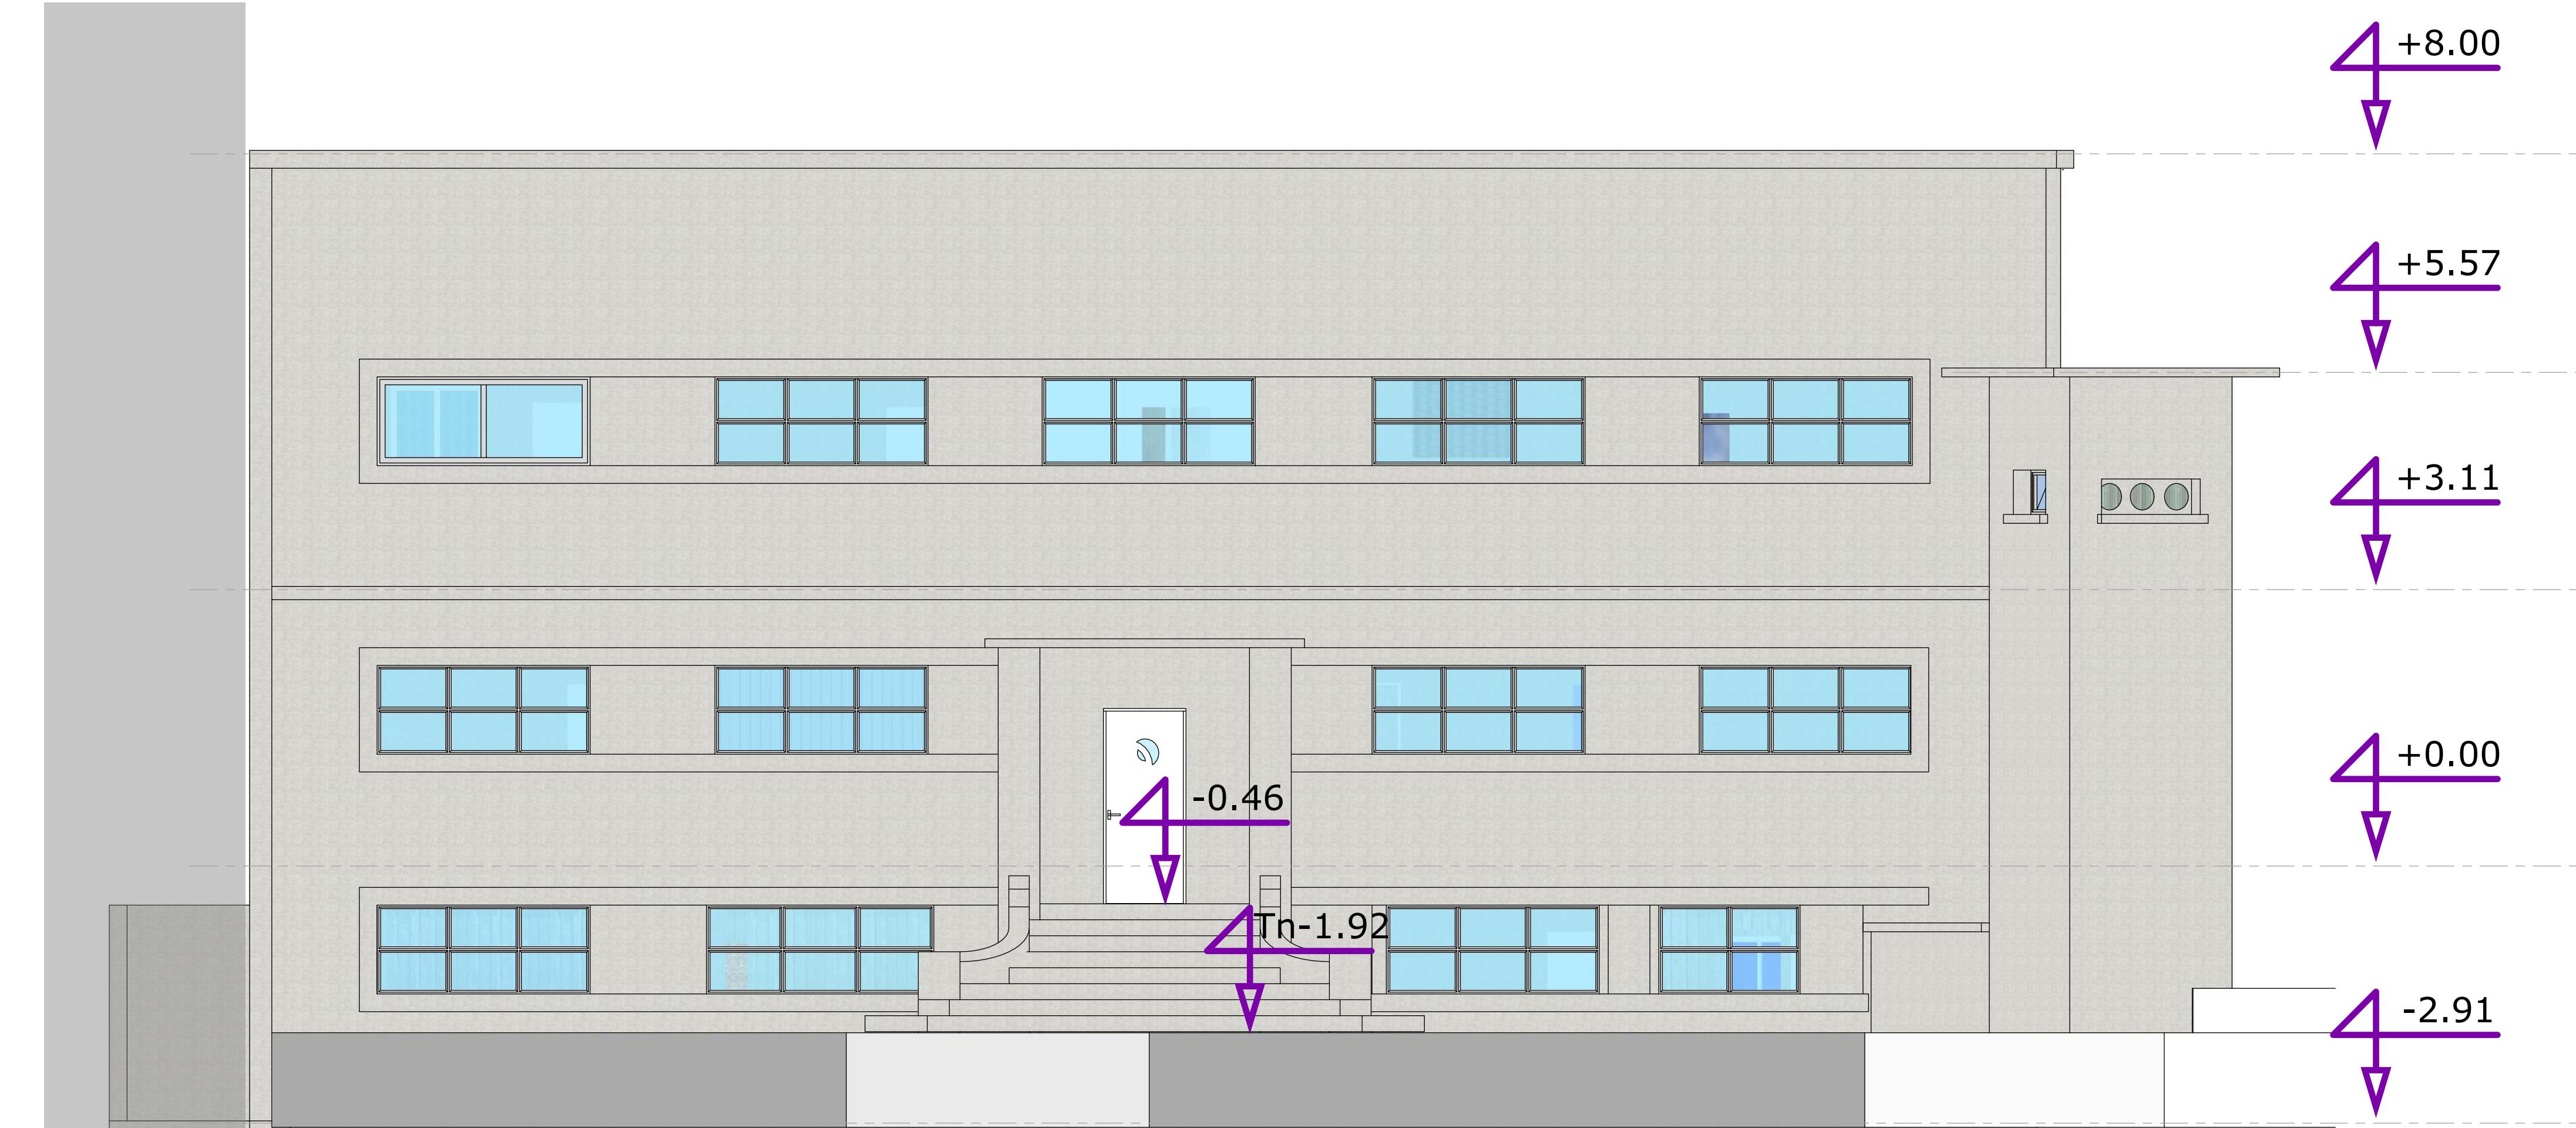


A AP EI
ap.bureau.etude@gmail.com 2


12-14 Rue de la Gare Le Mérévillon 91660
Résidence Le DUC d'Uber

Plan état existant - Façades
Echelle : 1/50

Dernière modification : 24/10/2023
Révision : v0.03

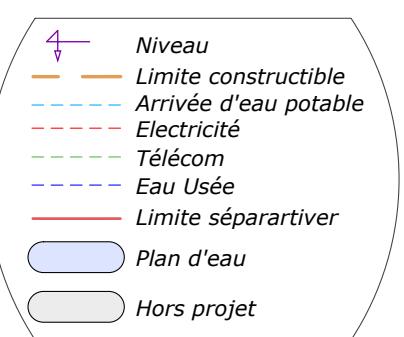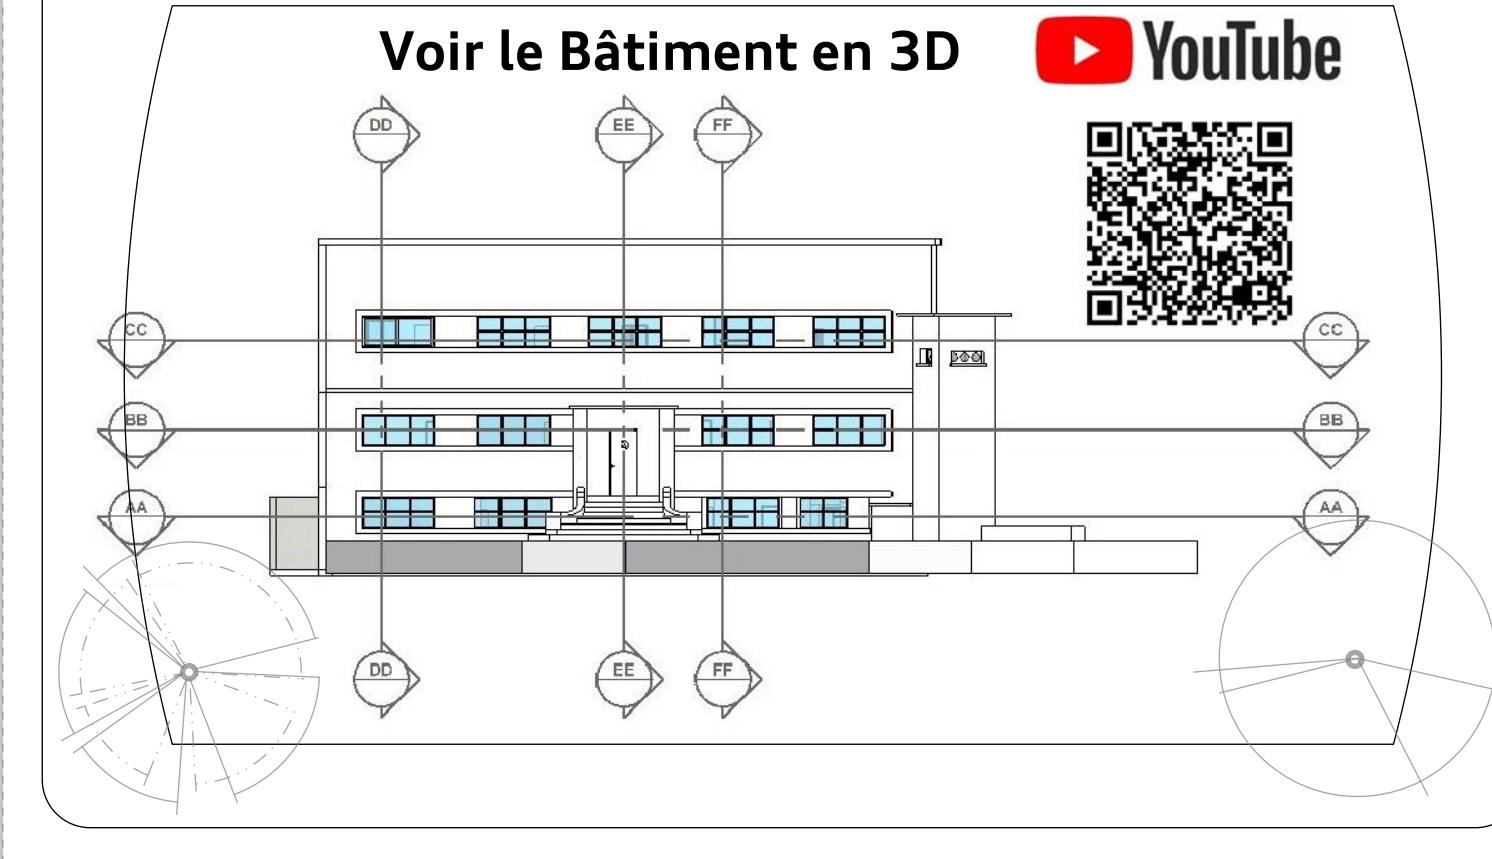


Coupe DD
1/50

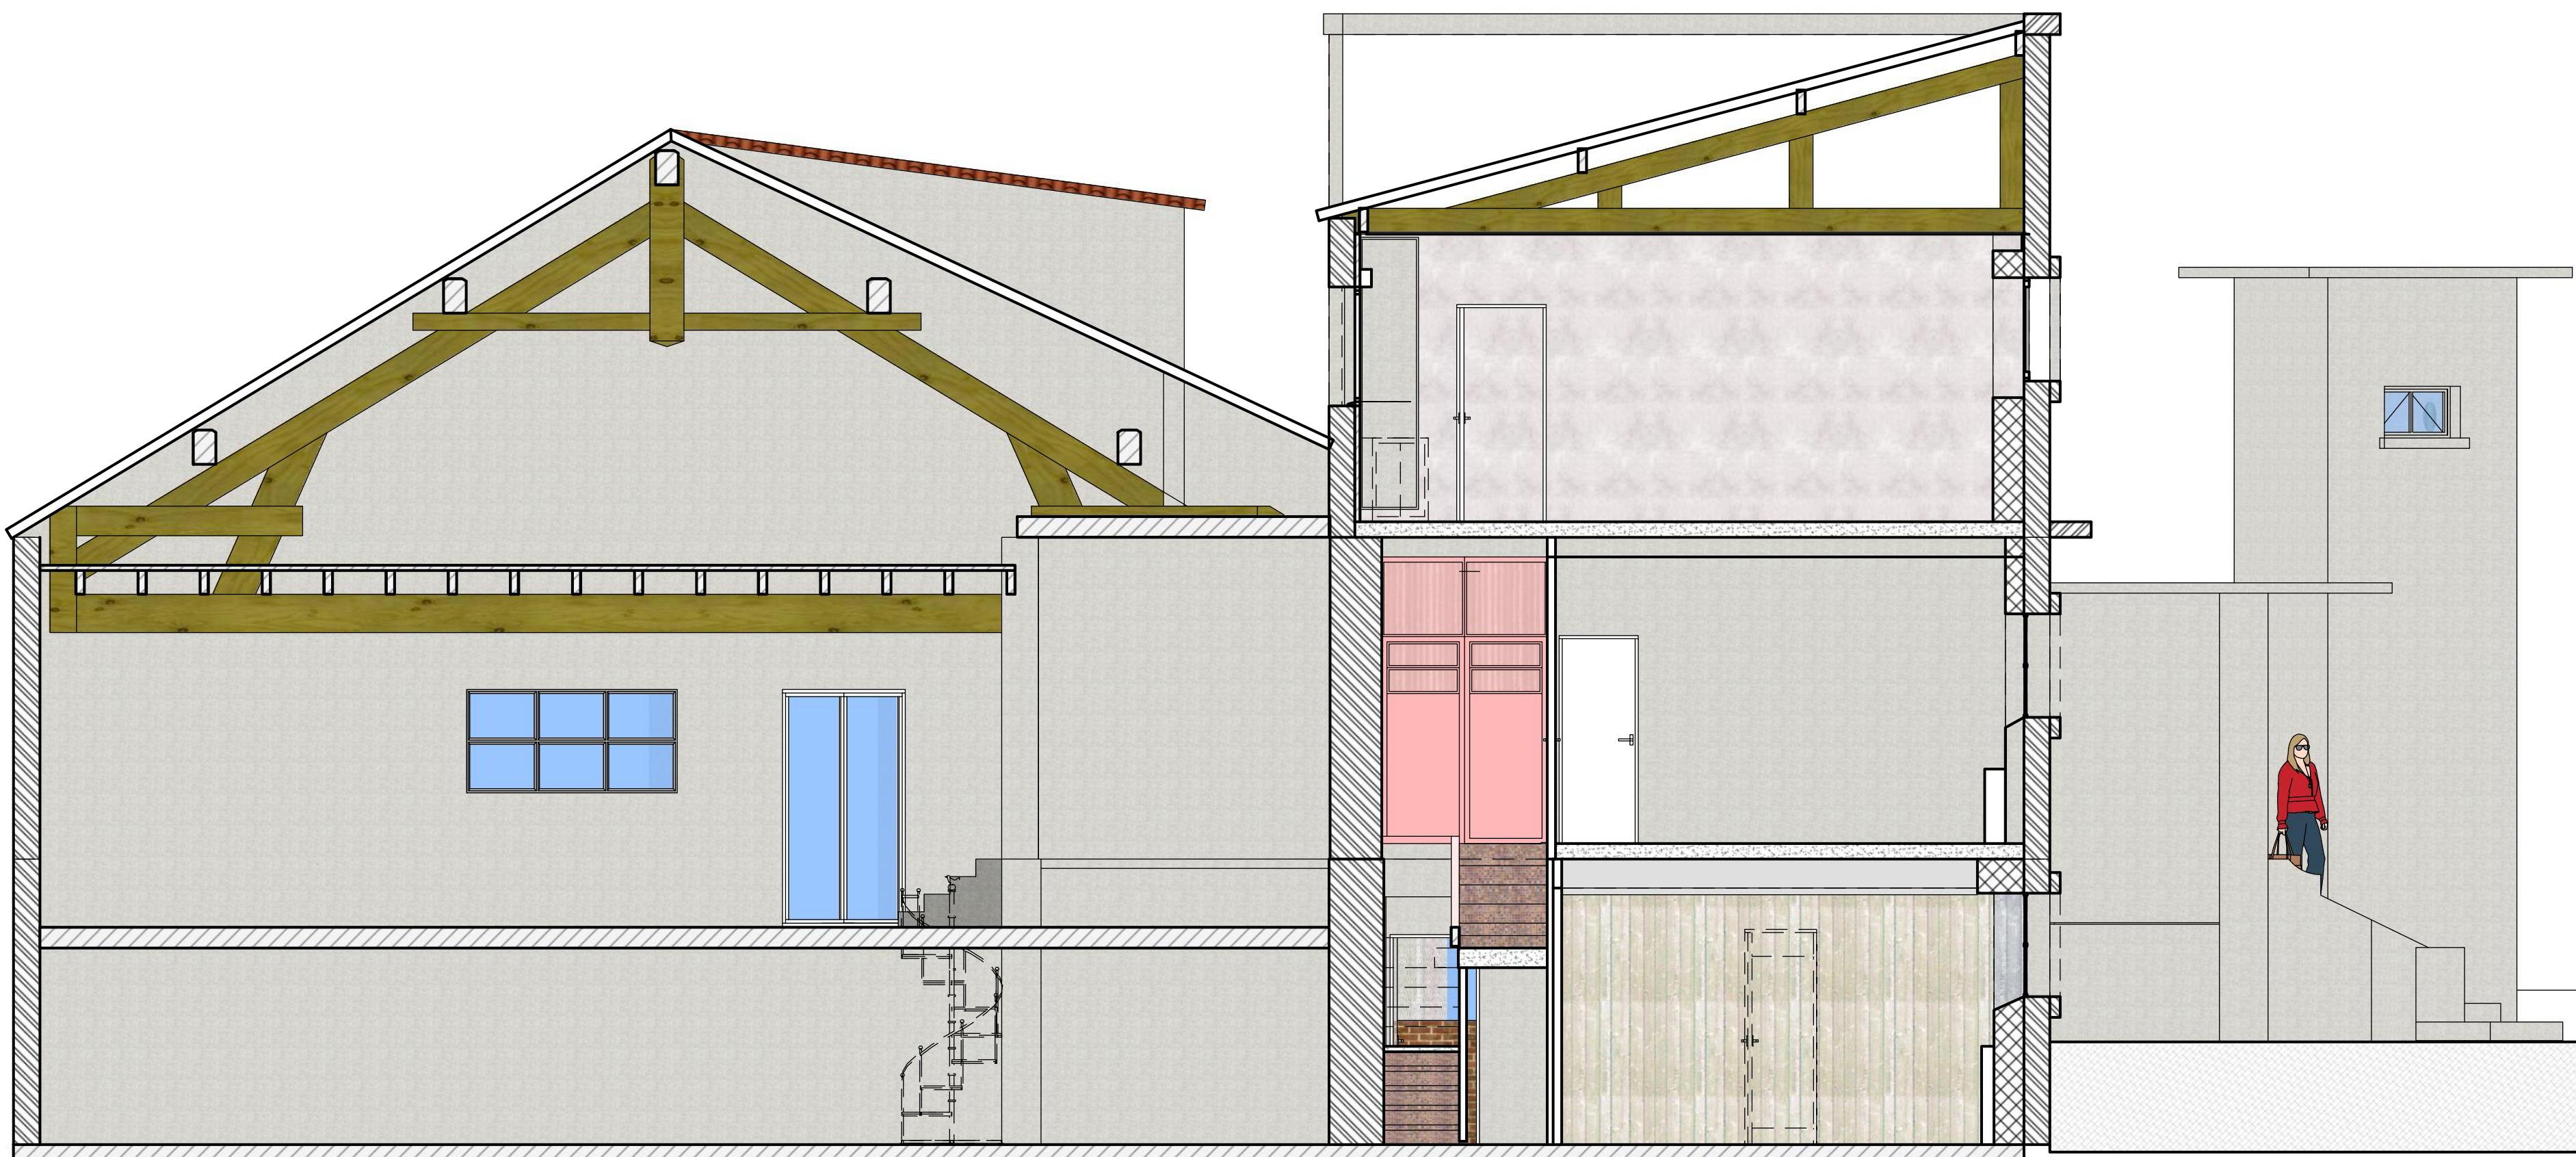

Coupe FF
1/50



Coupe EE
1/50

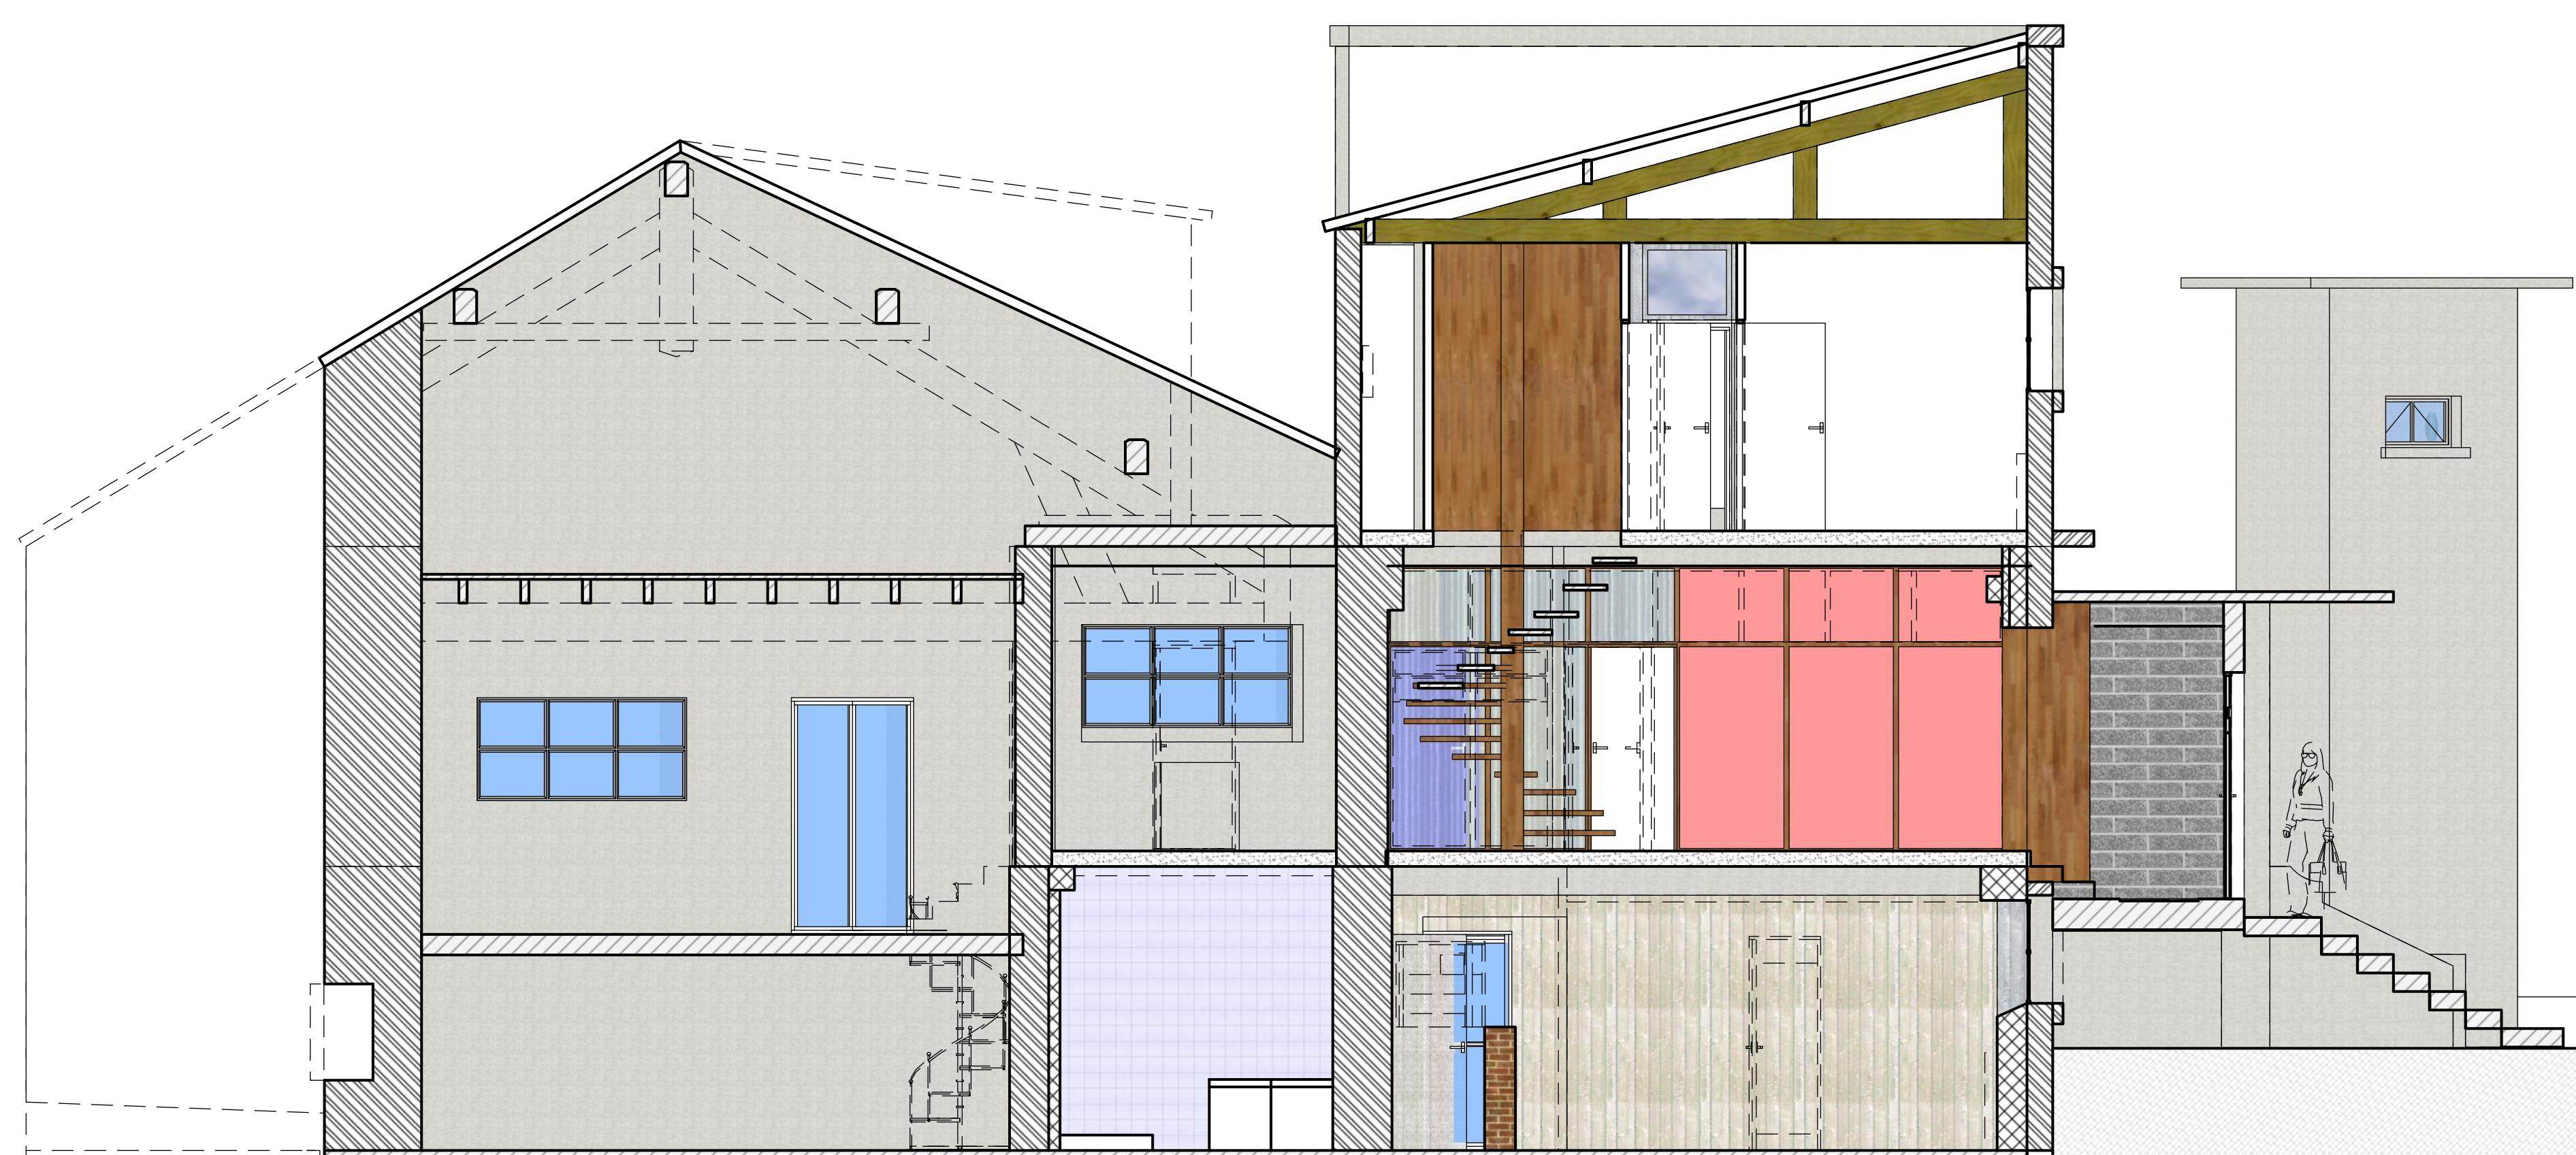

Coupe GG
1/50

