


AP EI  
ap.bureau.etude@gmail.com


7

12-14 Rue de la Gare Le Mérévillon 91660  
Résidence Le DUC d'Uber

Plan état existant - Coupe AA R-1 |BB R0 |CC R+1  
Echelle : 1/50

Dernière modification : 24/10/2023  
Révision : v0.03

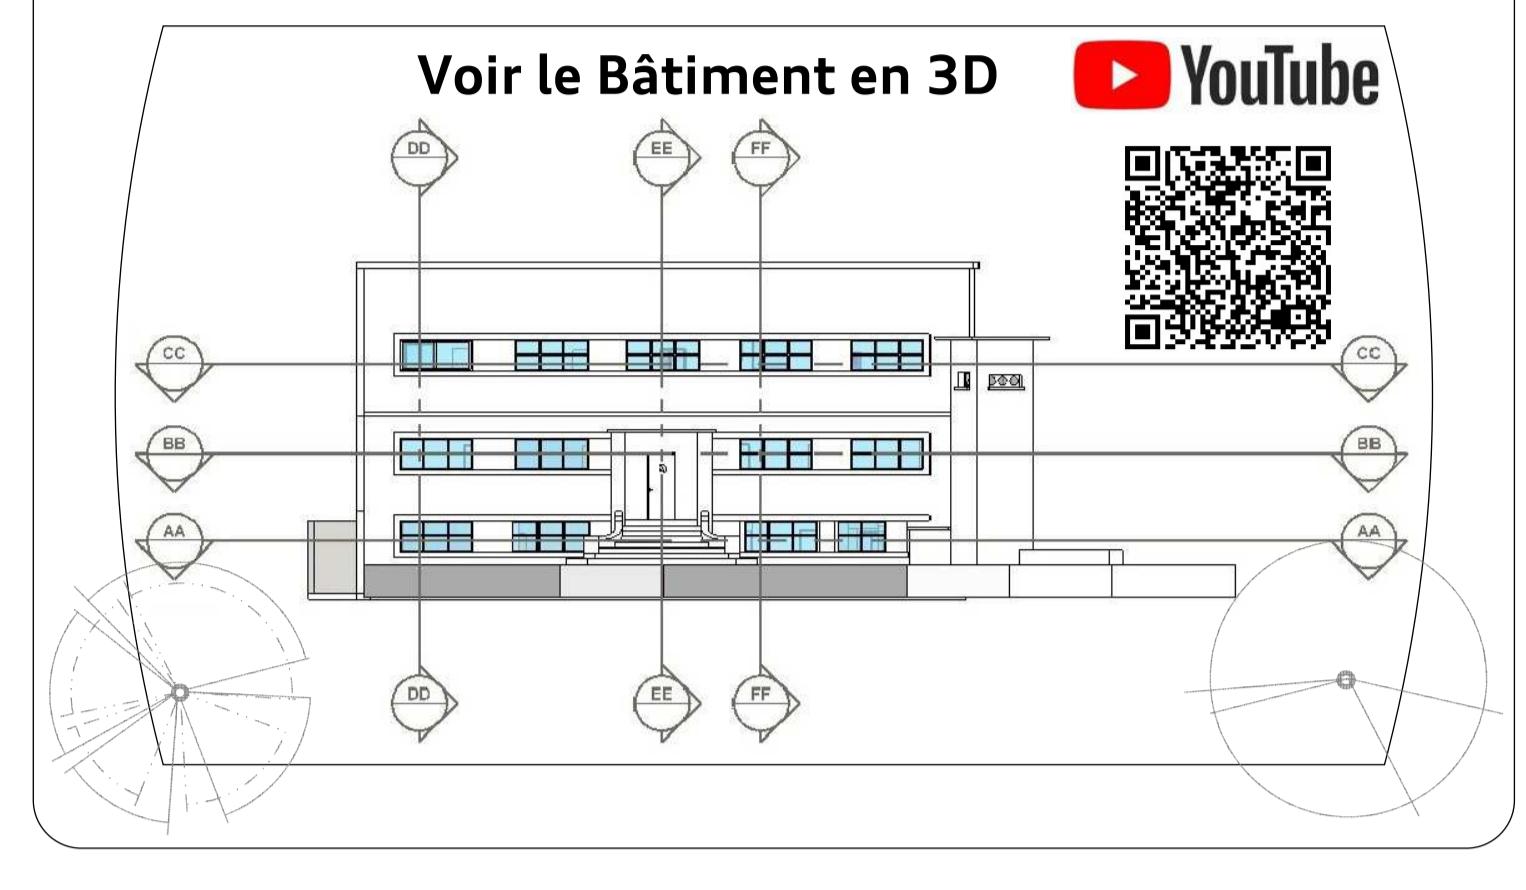

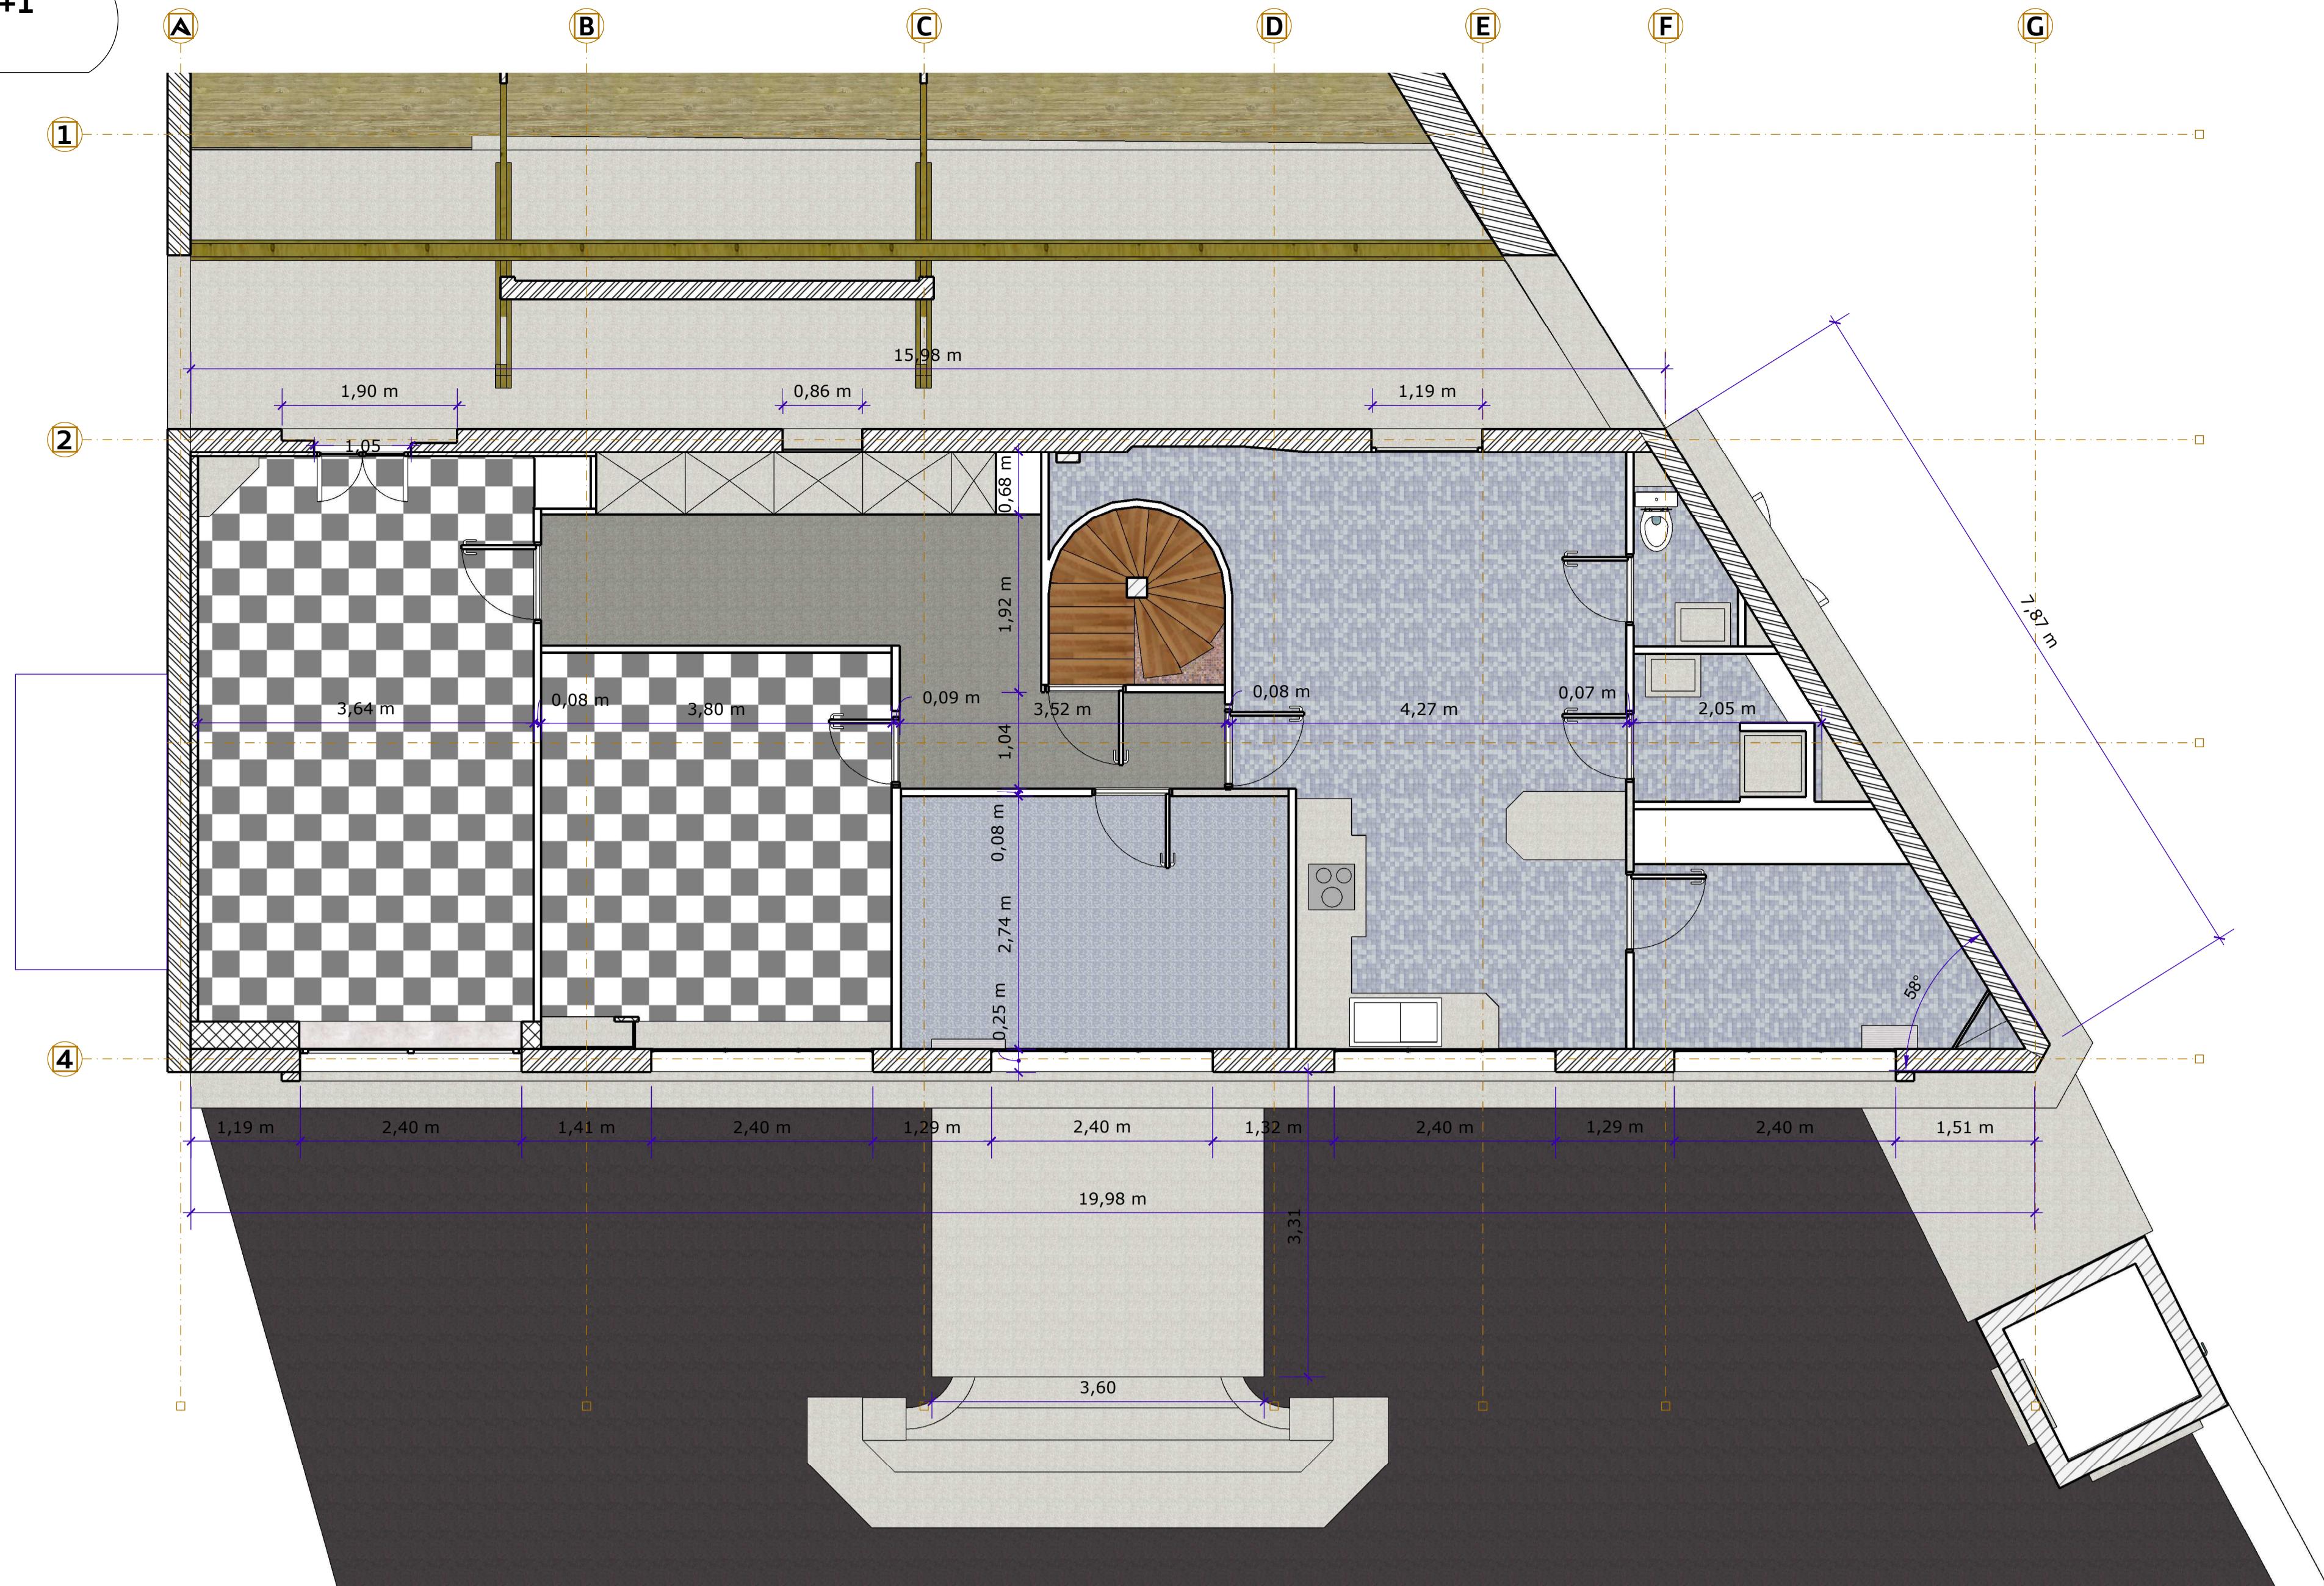

[ap.bureau.etude@gmail.com](mailto:ap.bureau.etude@gmail.com)

[View all posts](#) | [View all categories](#)


8

**12-14 Rue de la Gare Le Mérévillon 91660  
Résidence Le DUC d'Uber**

# **Plan état existant - Coupe AA R-1 |BB R0 |CC R+1**



## **Echelle : 1/50**



Dernière modification : 24/10/2023  
Revision : v0.03

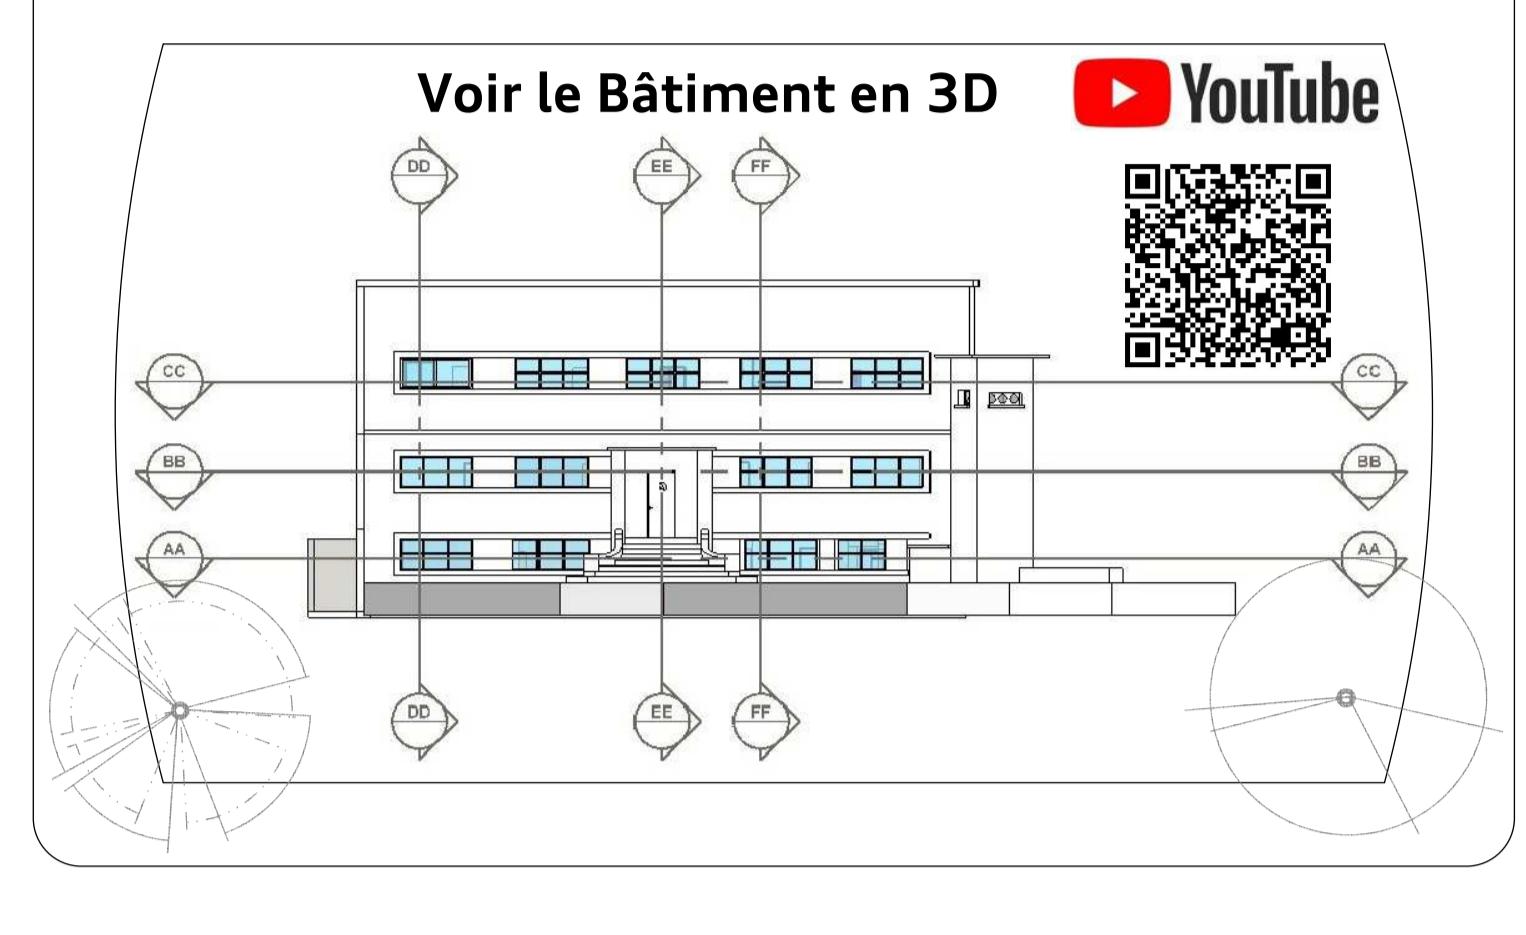


The diagram illustrates the progression of infrastructure levels from 'Niveau' at the top to 'Hors projet' at the bottom. It features a series of colored horizontal bars and labels:

- Niveau**: Represented by a purple bar with an upward-pointing arrow.
- Limite constructible**: Represented by an orange bar.
- Arrivée d'eau potable**: Represented by a blue dashed bar.
- Electricité**: Represented by a red dashed bar.
- Télécom**: Represented by a green dashed bar.
- Eau Usée**: Represented by a blue dashed bar.
- Limite séparatif**: Represented by a red bar.
- Plan d'eau**: Represented by a light blue rounded rectangle.
- Hors projet**: Represented by a light gray rounded rectangle.

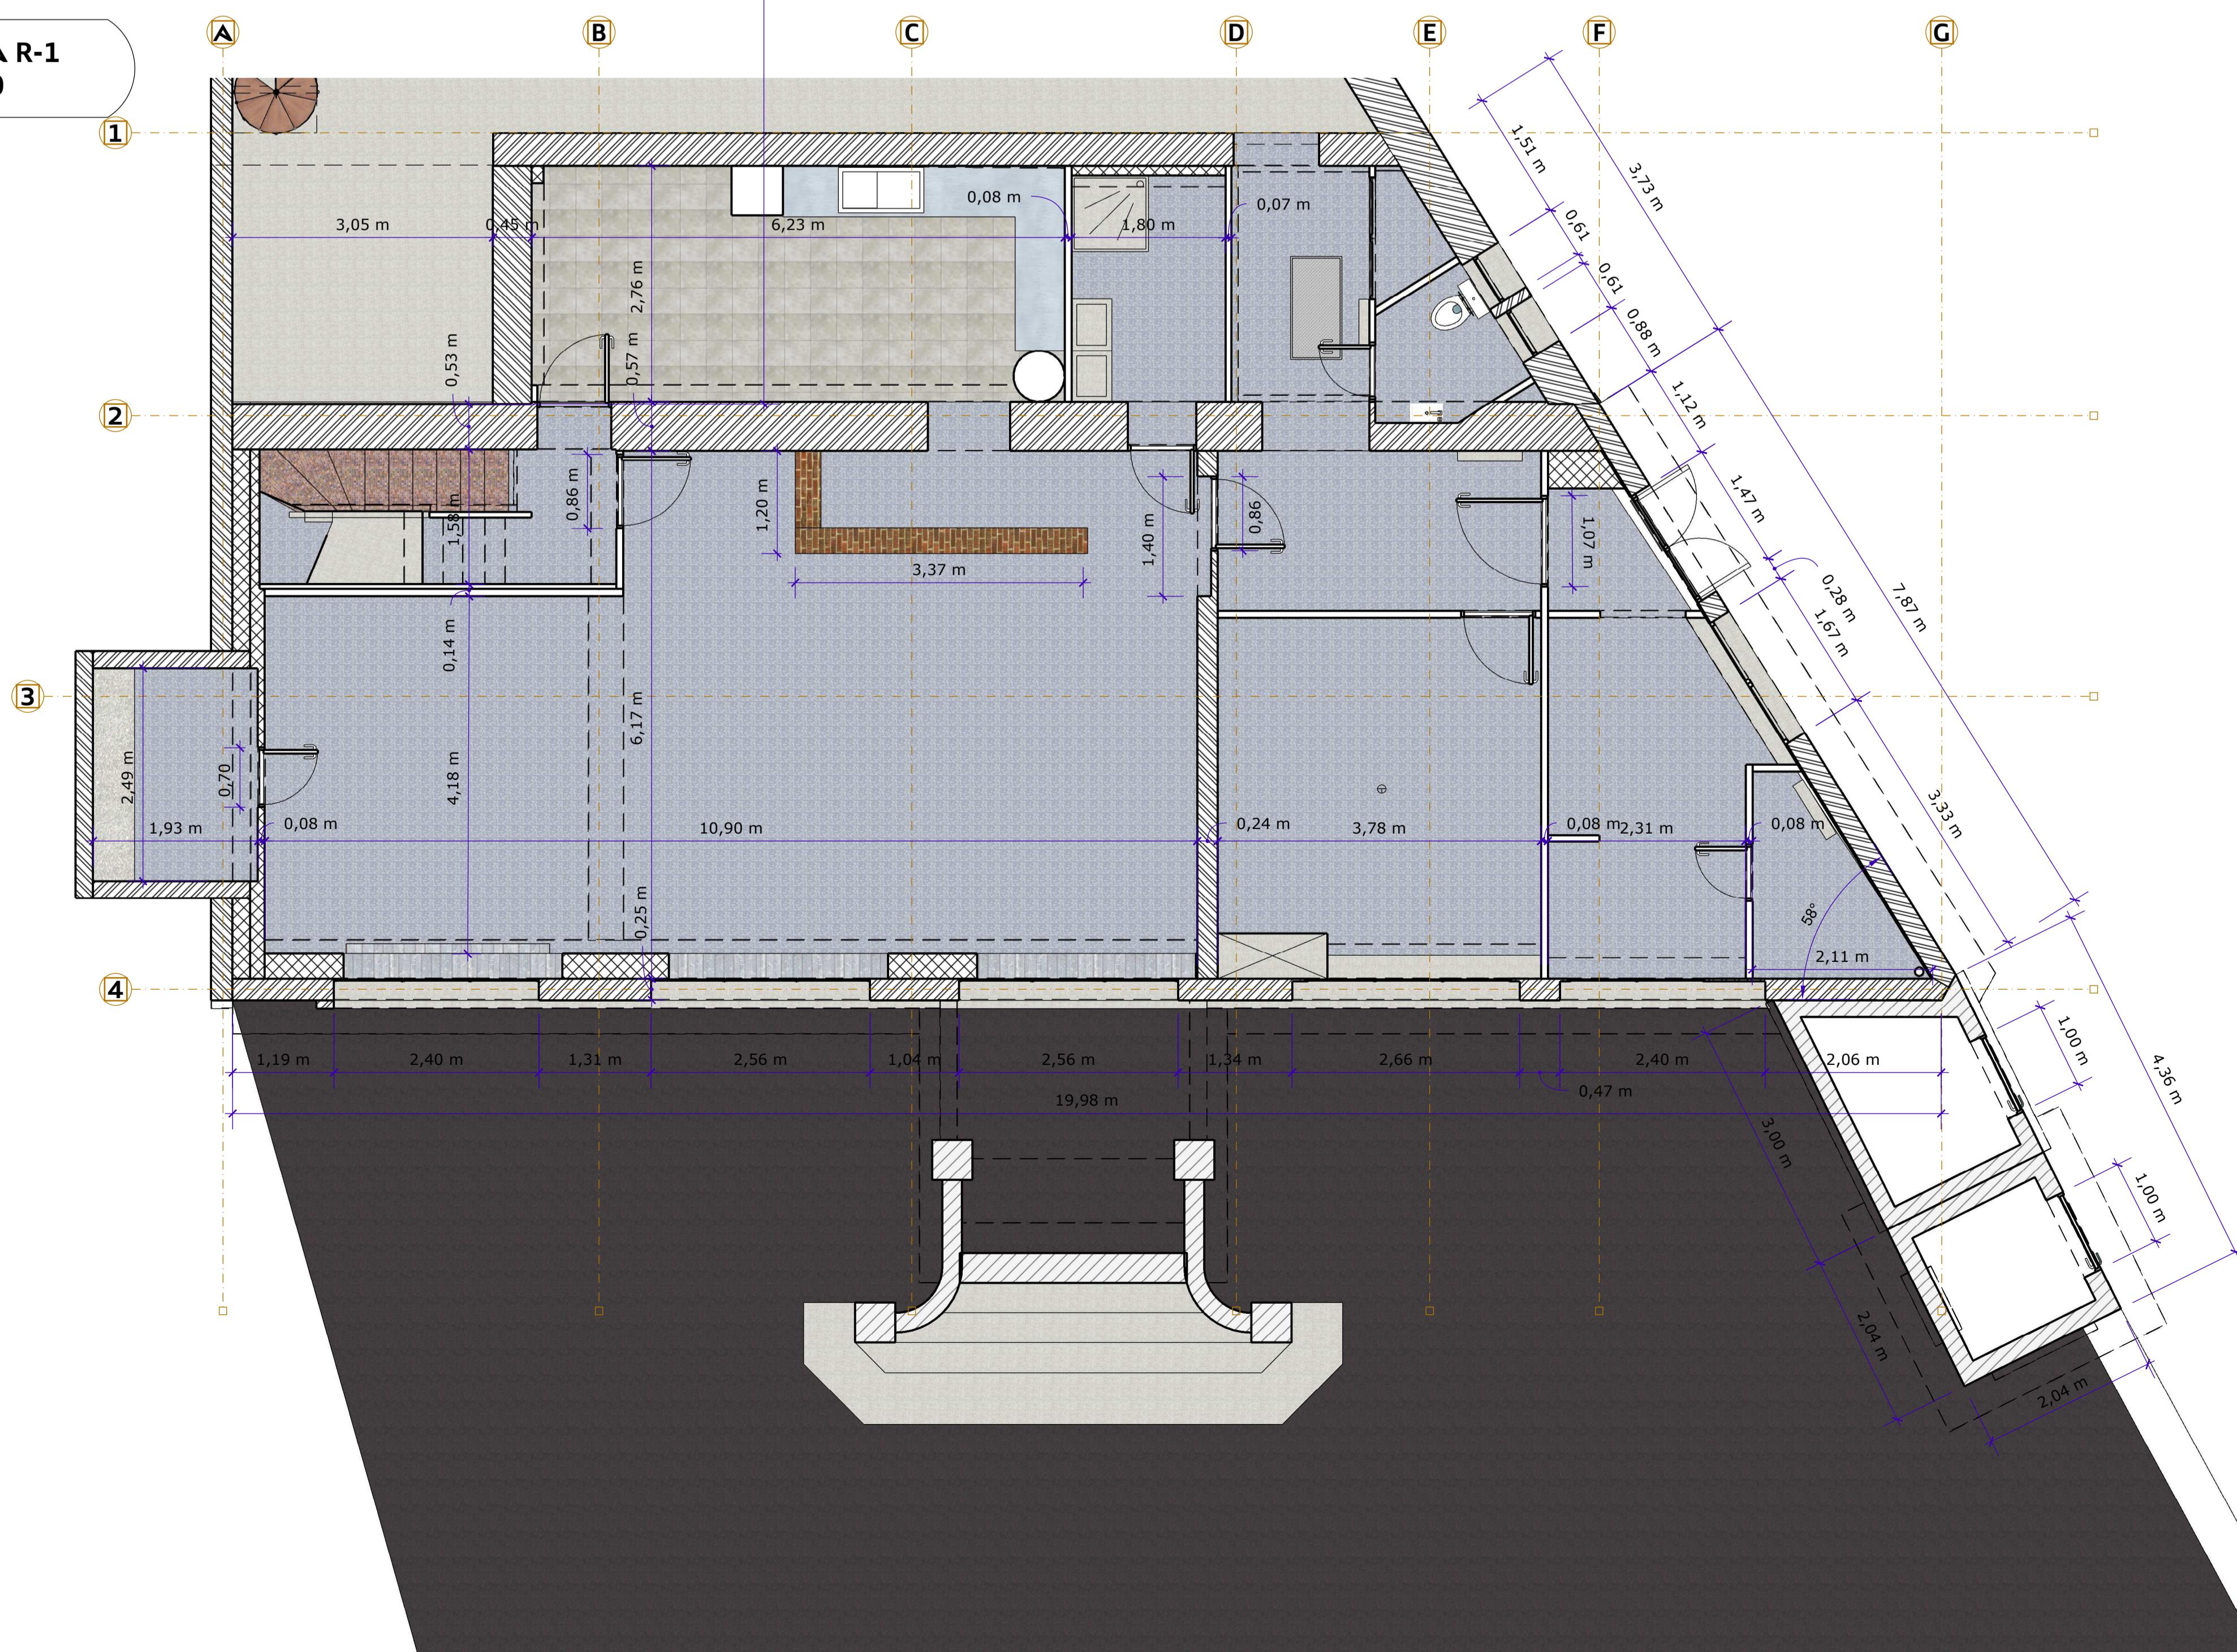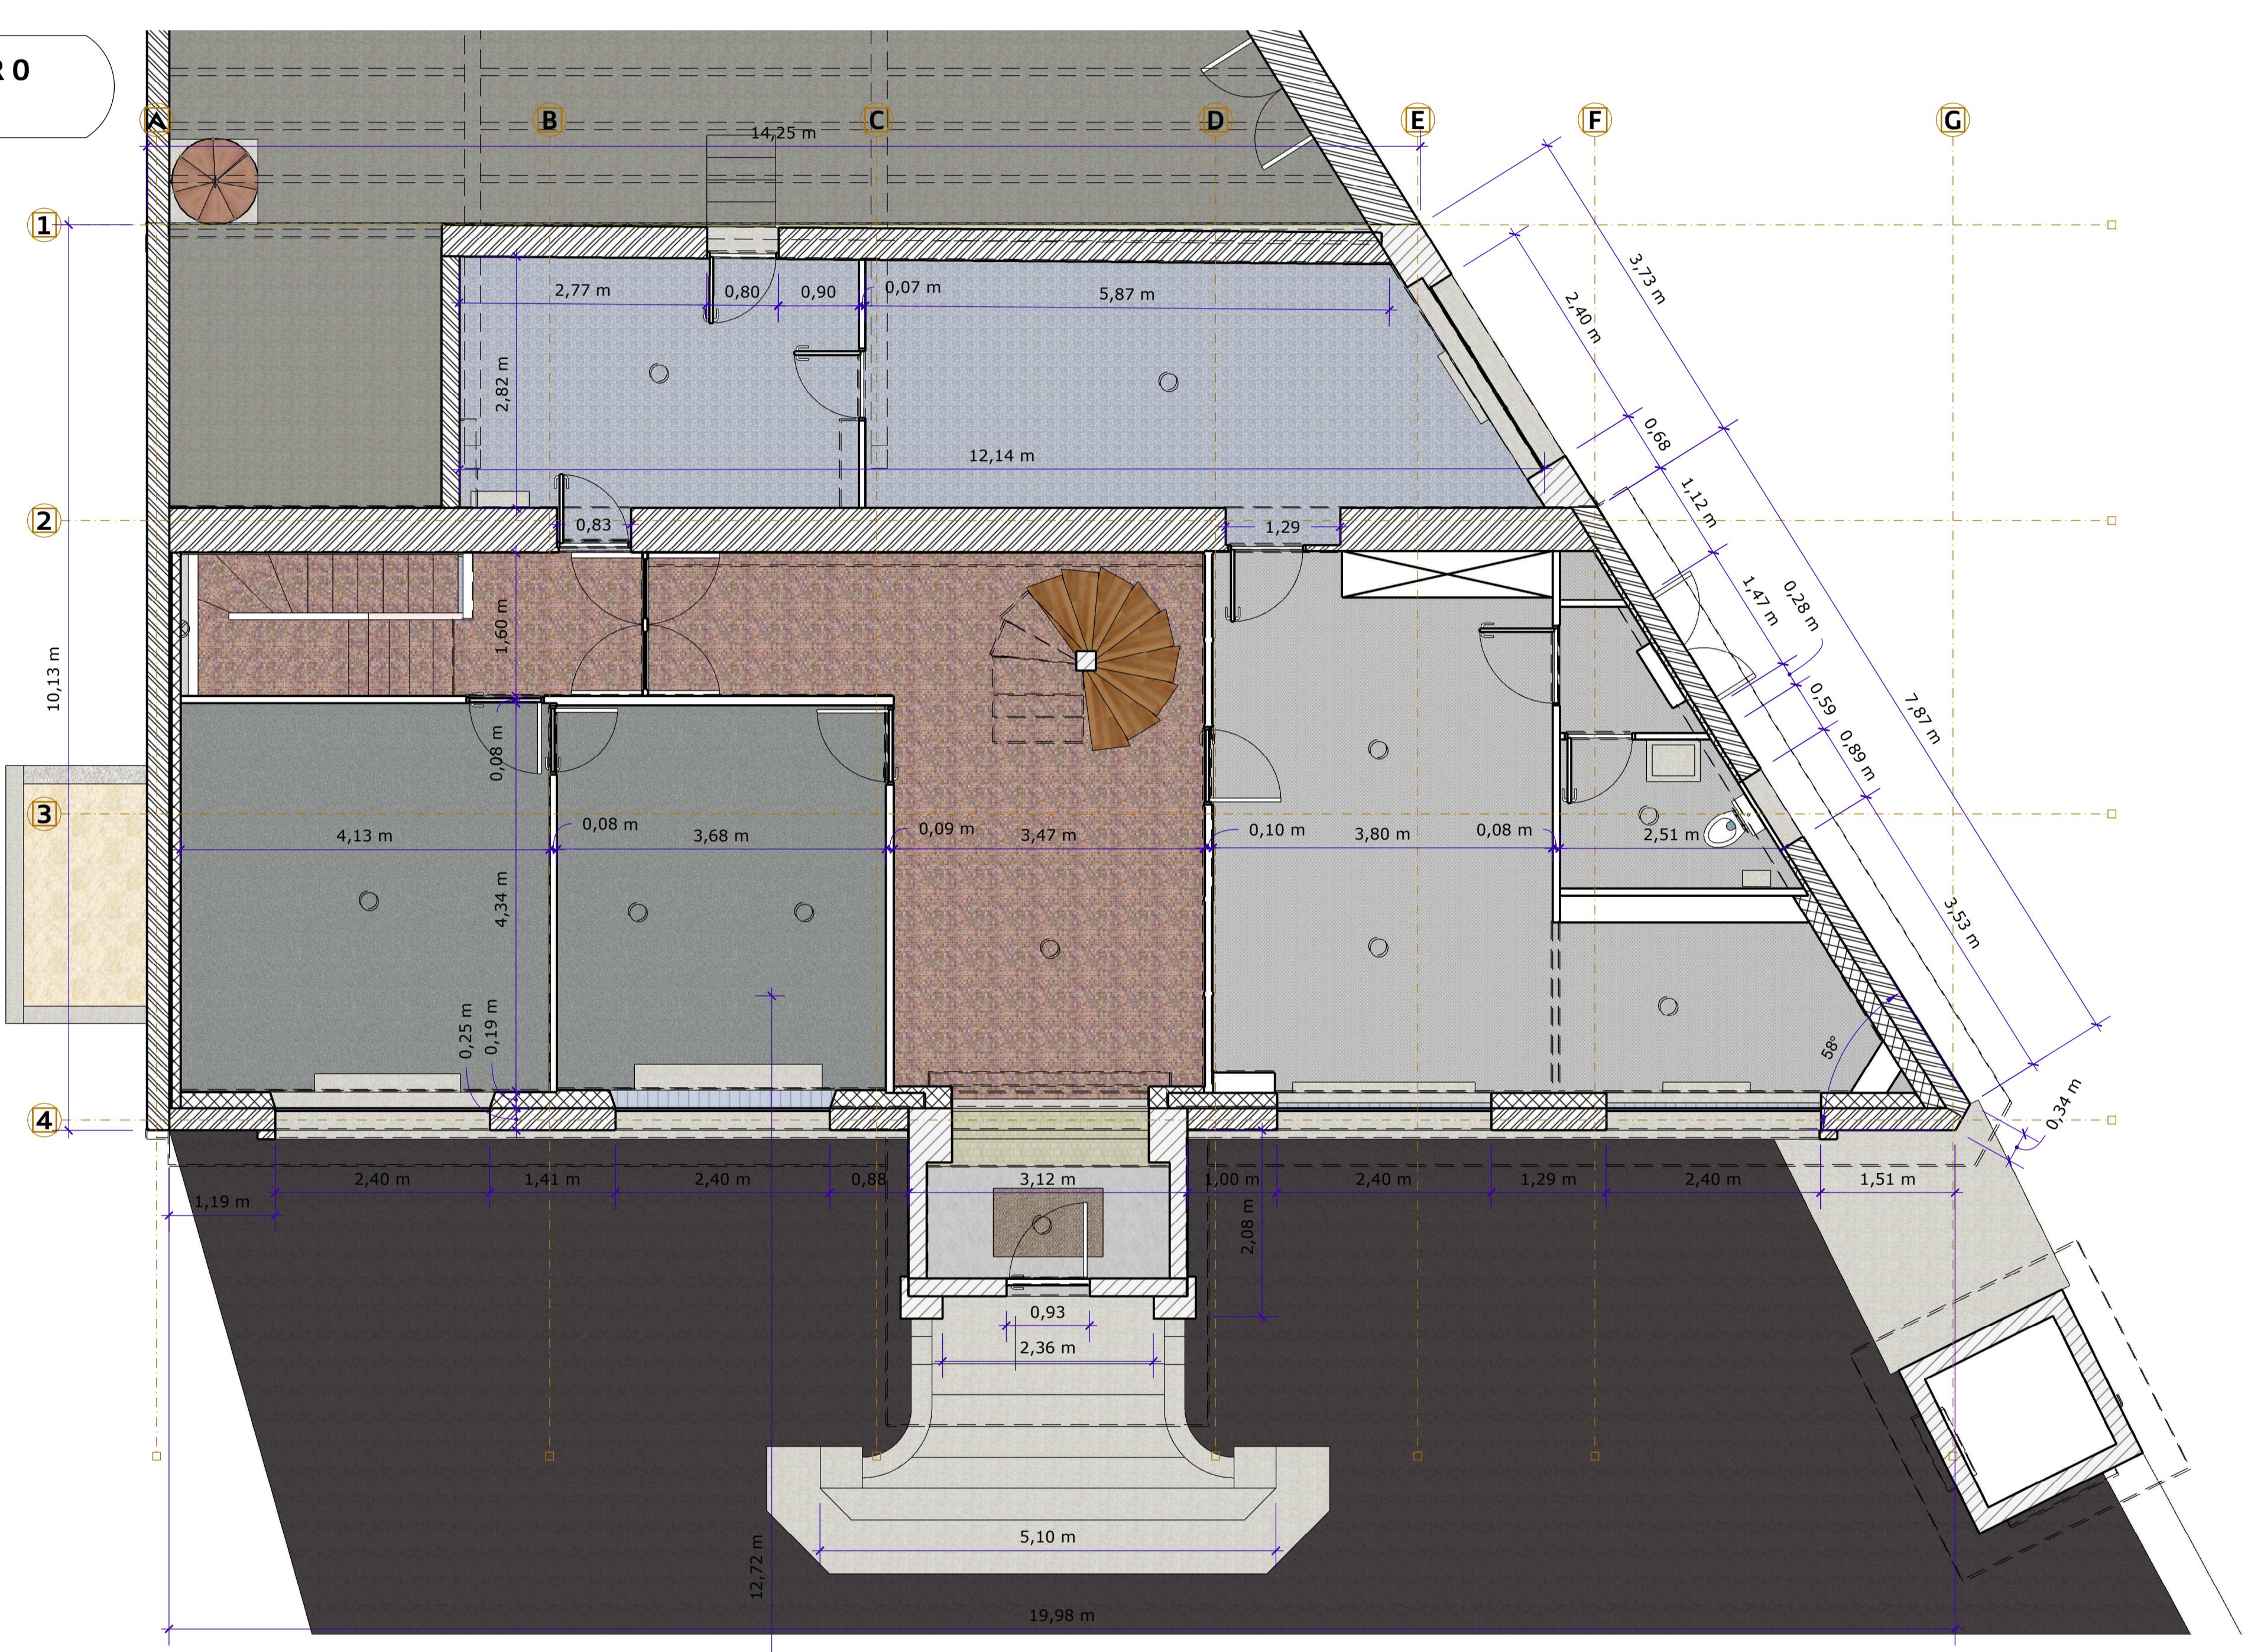

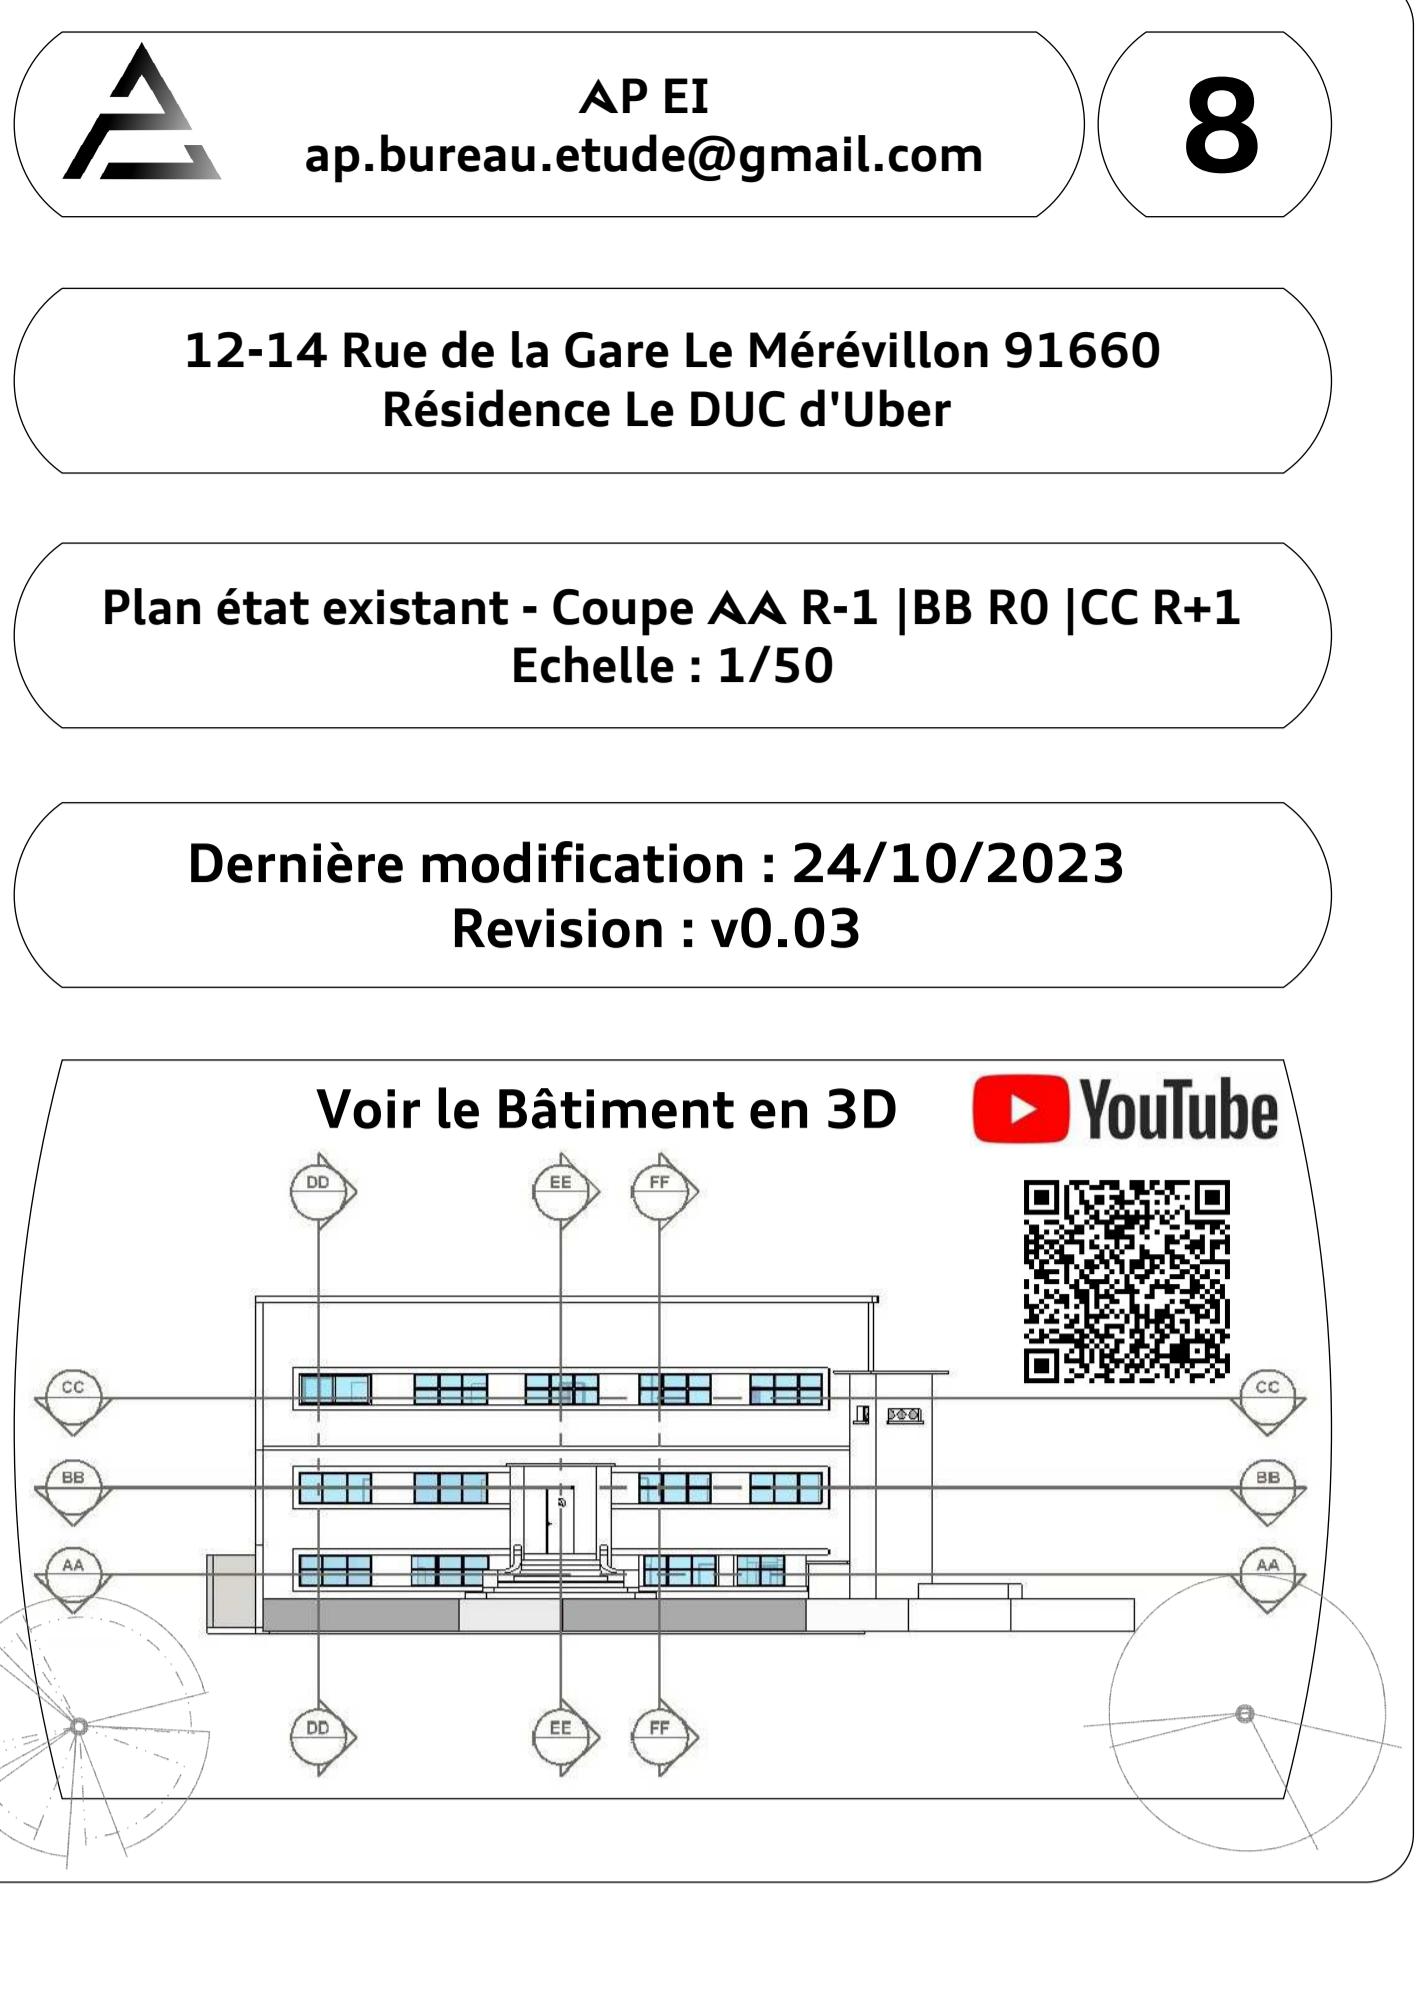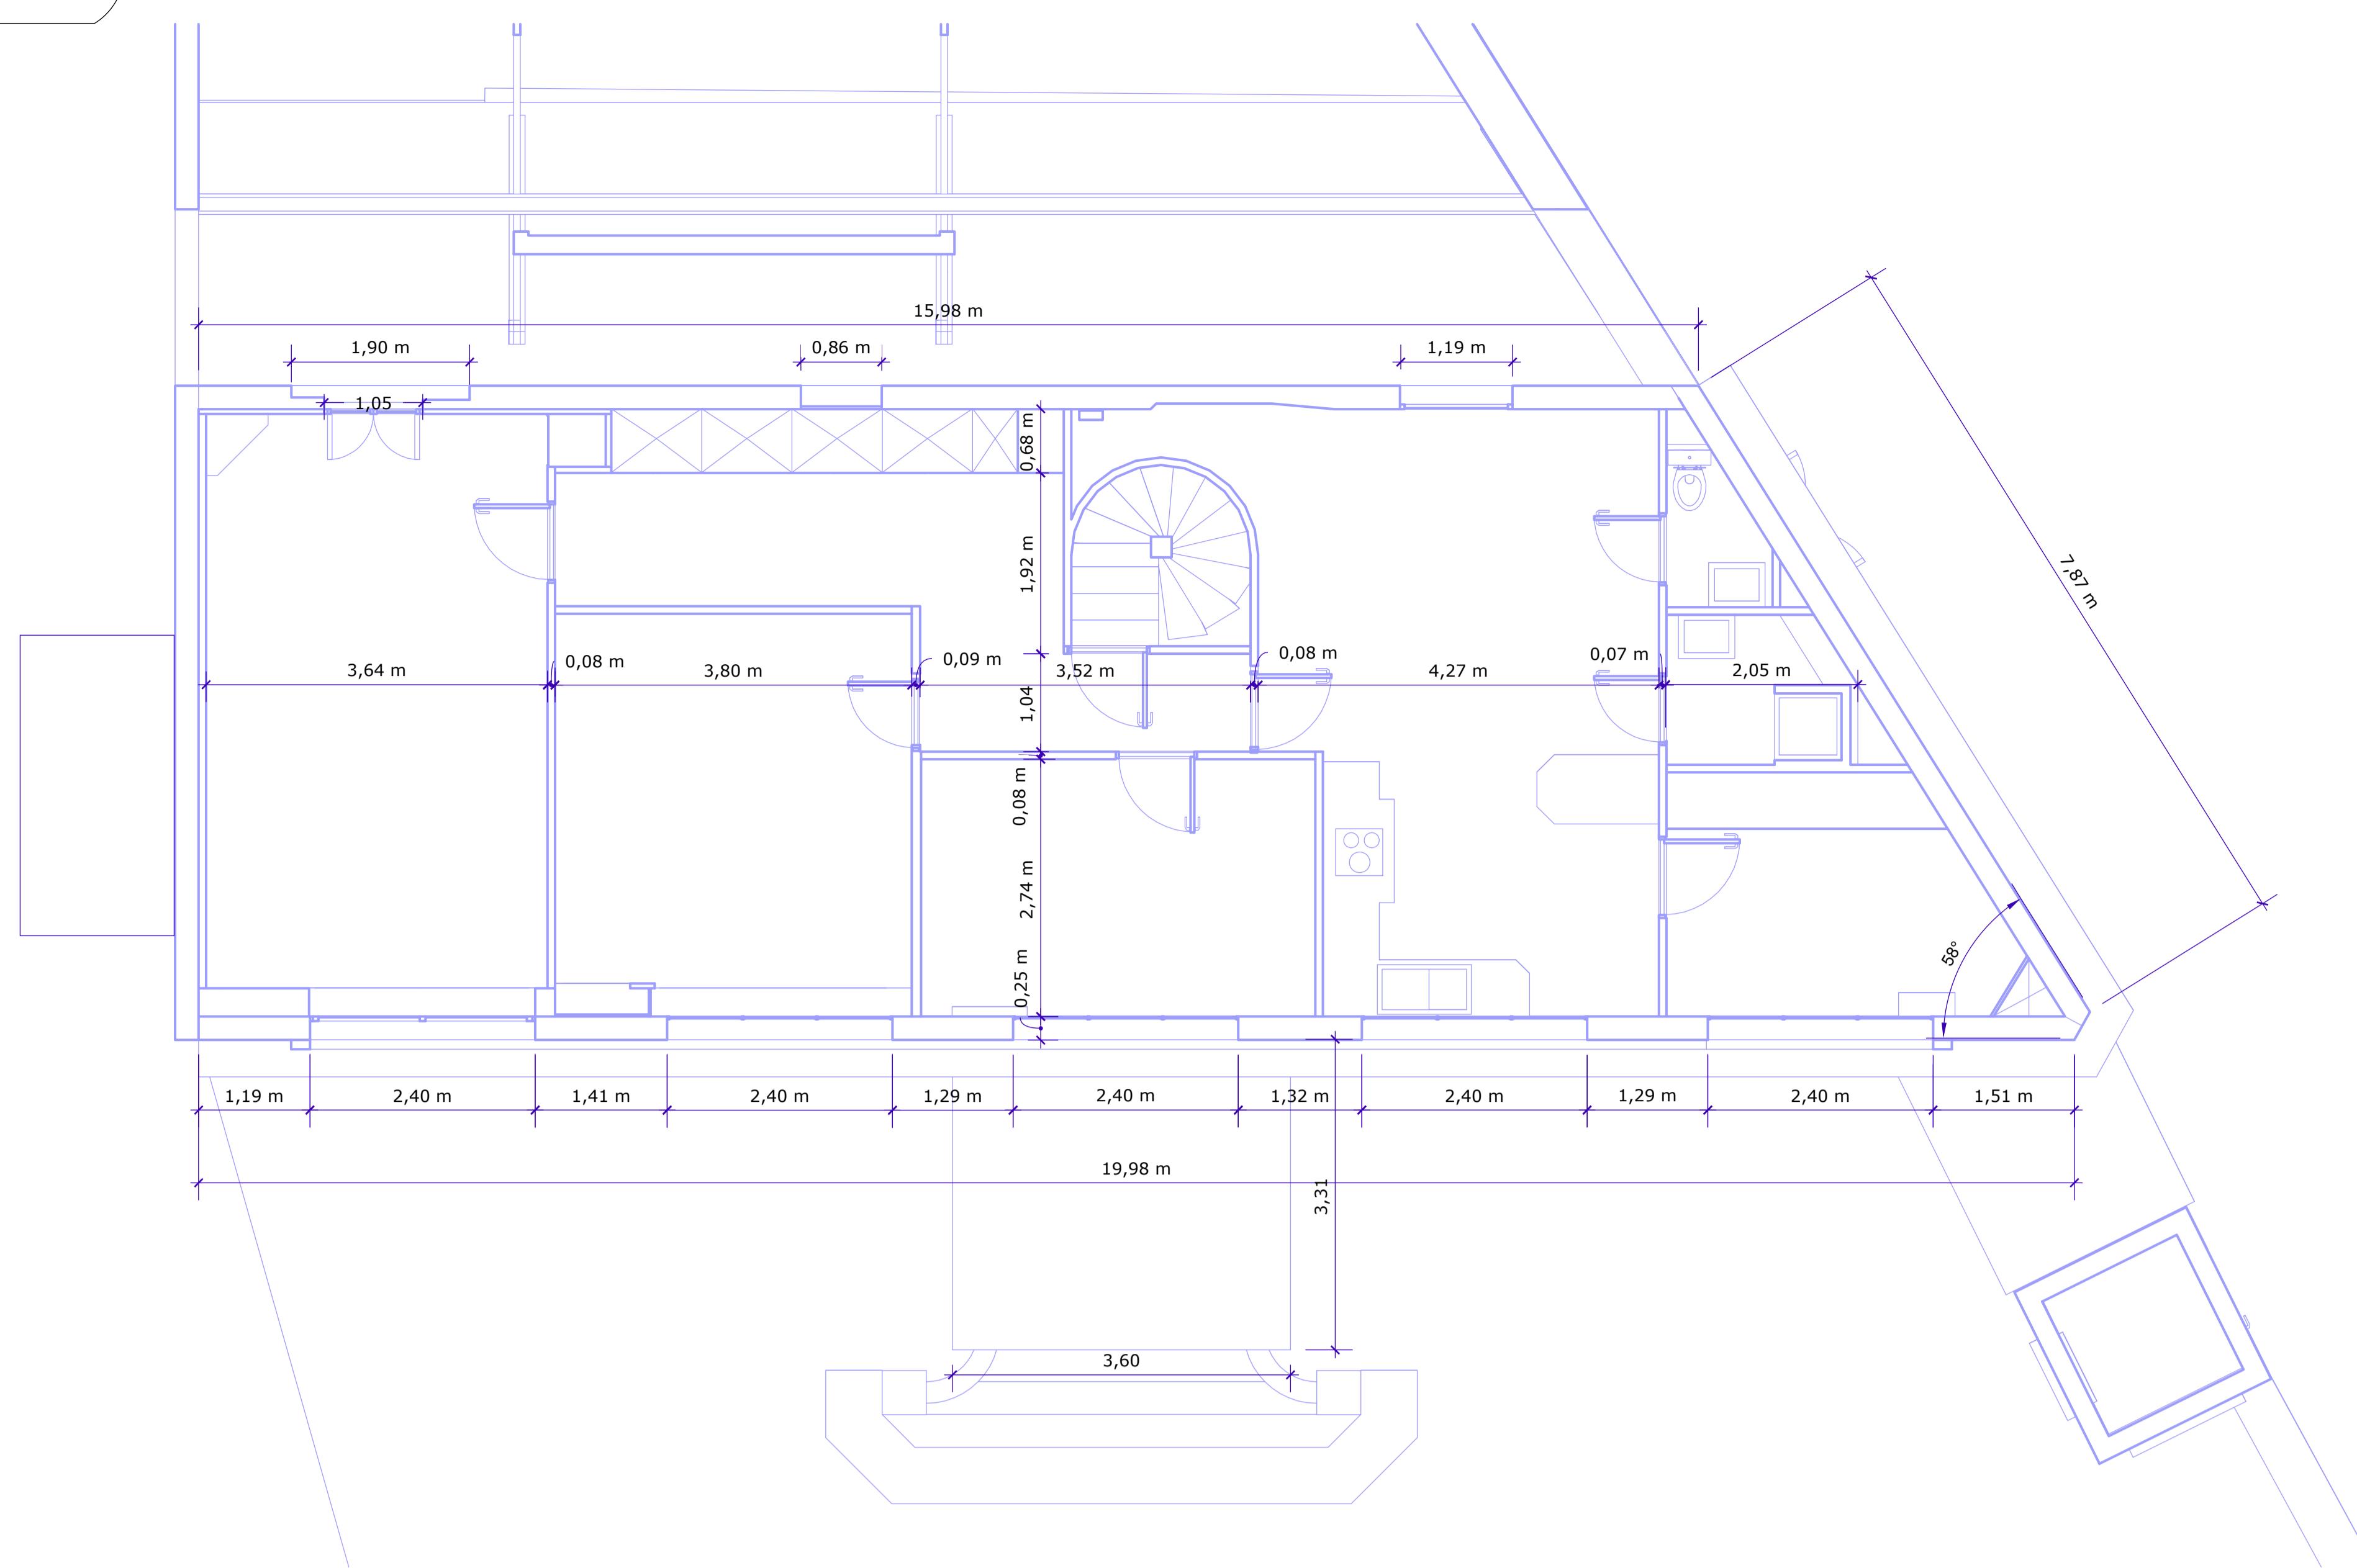

Coupe BB R 0  
1/50

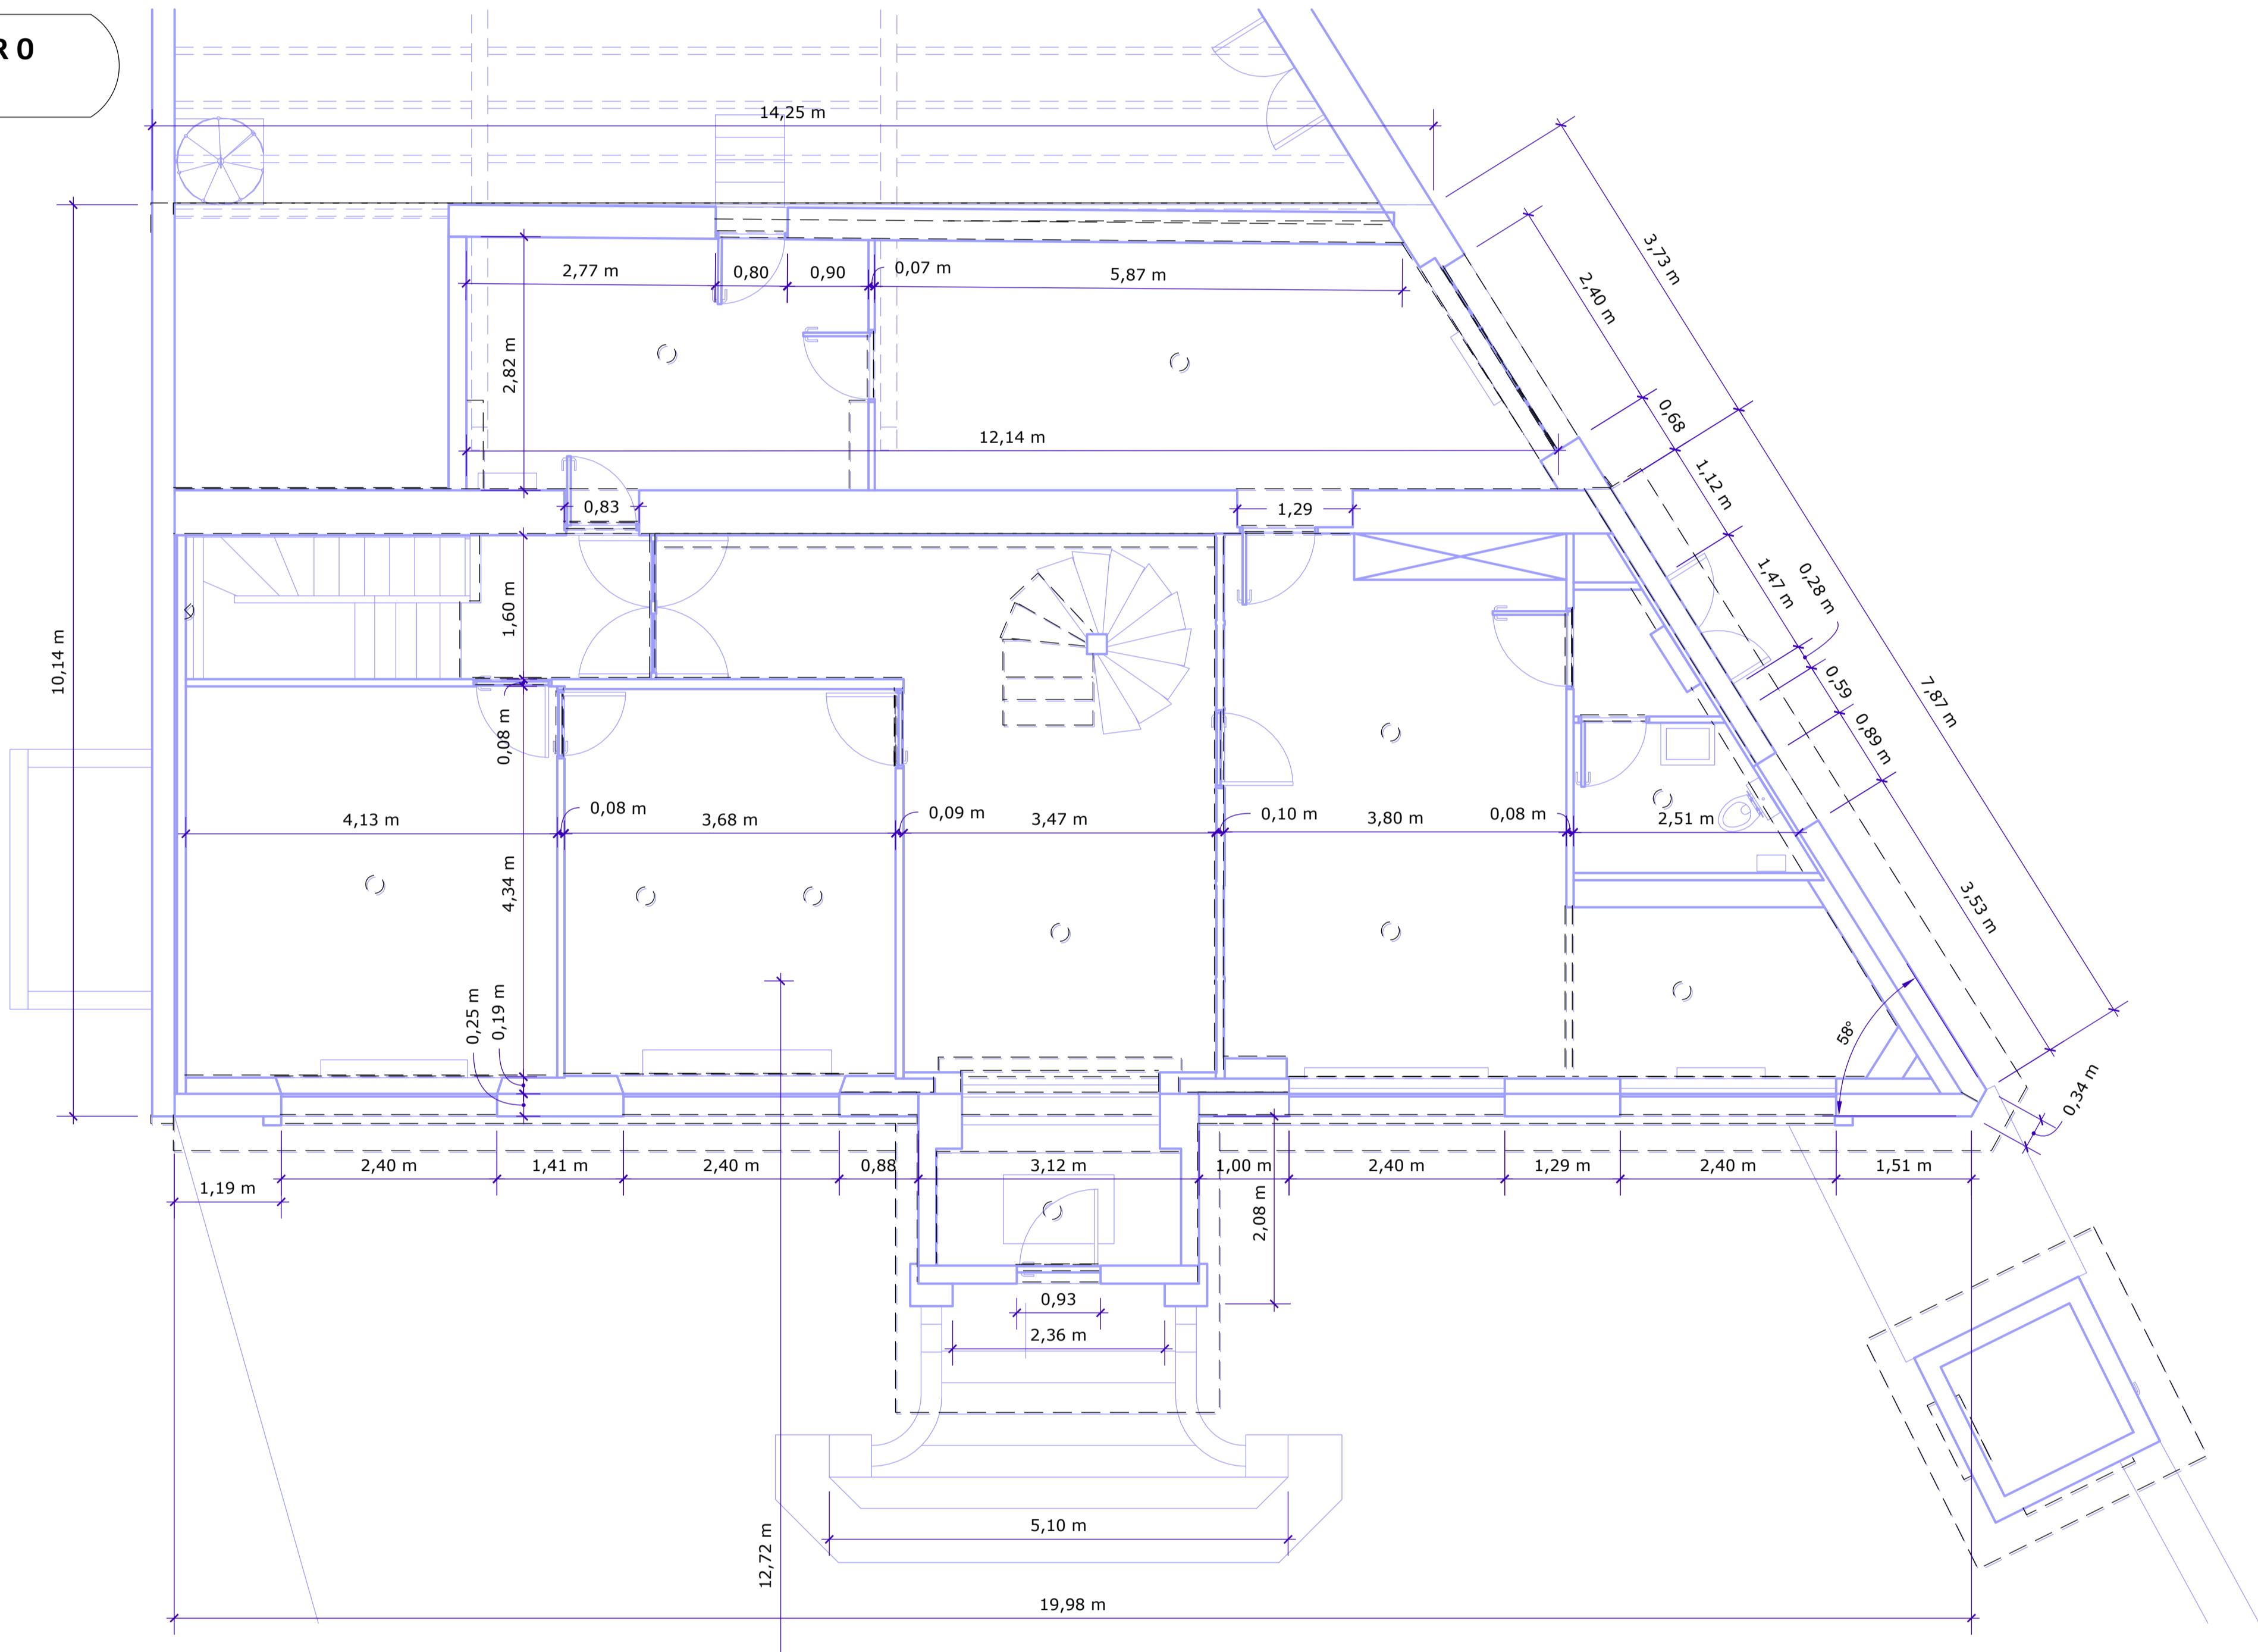

Coupe AA R-1  
1/50

