


Façade Nord




Façade Nord




Iso R+1

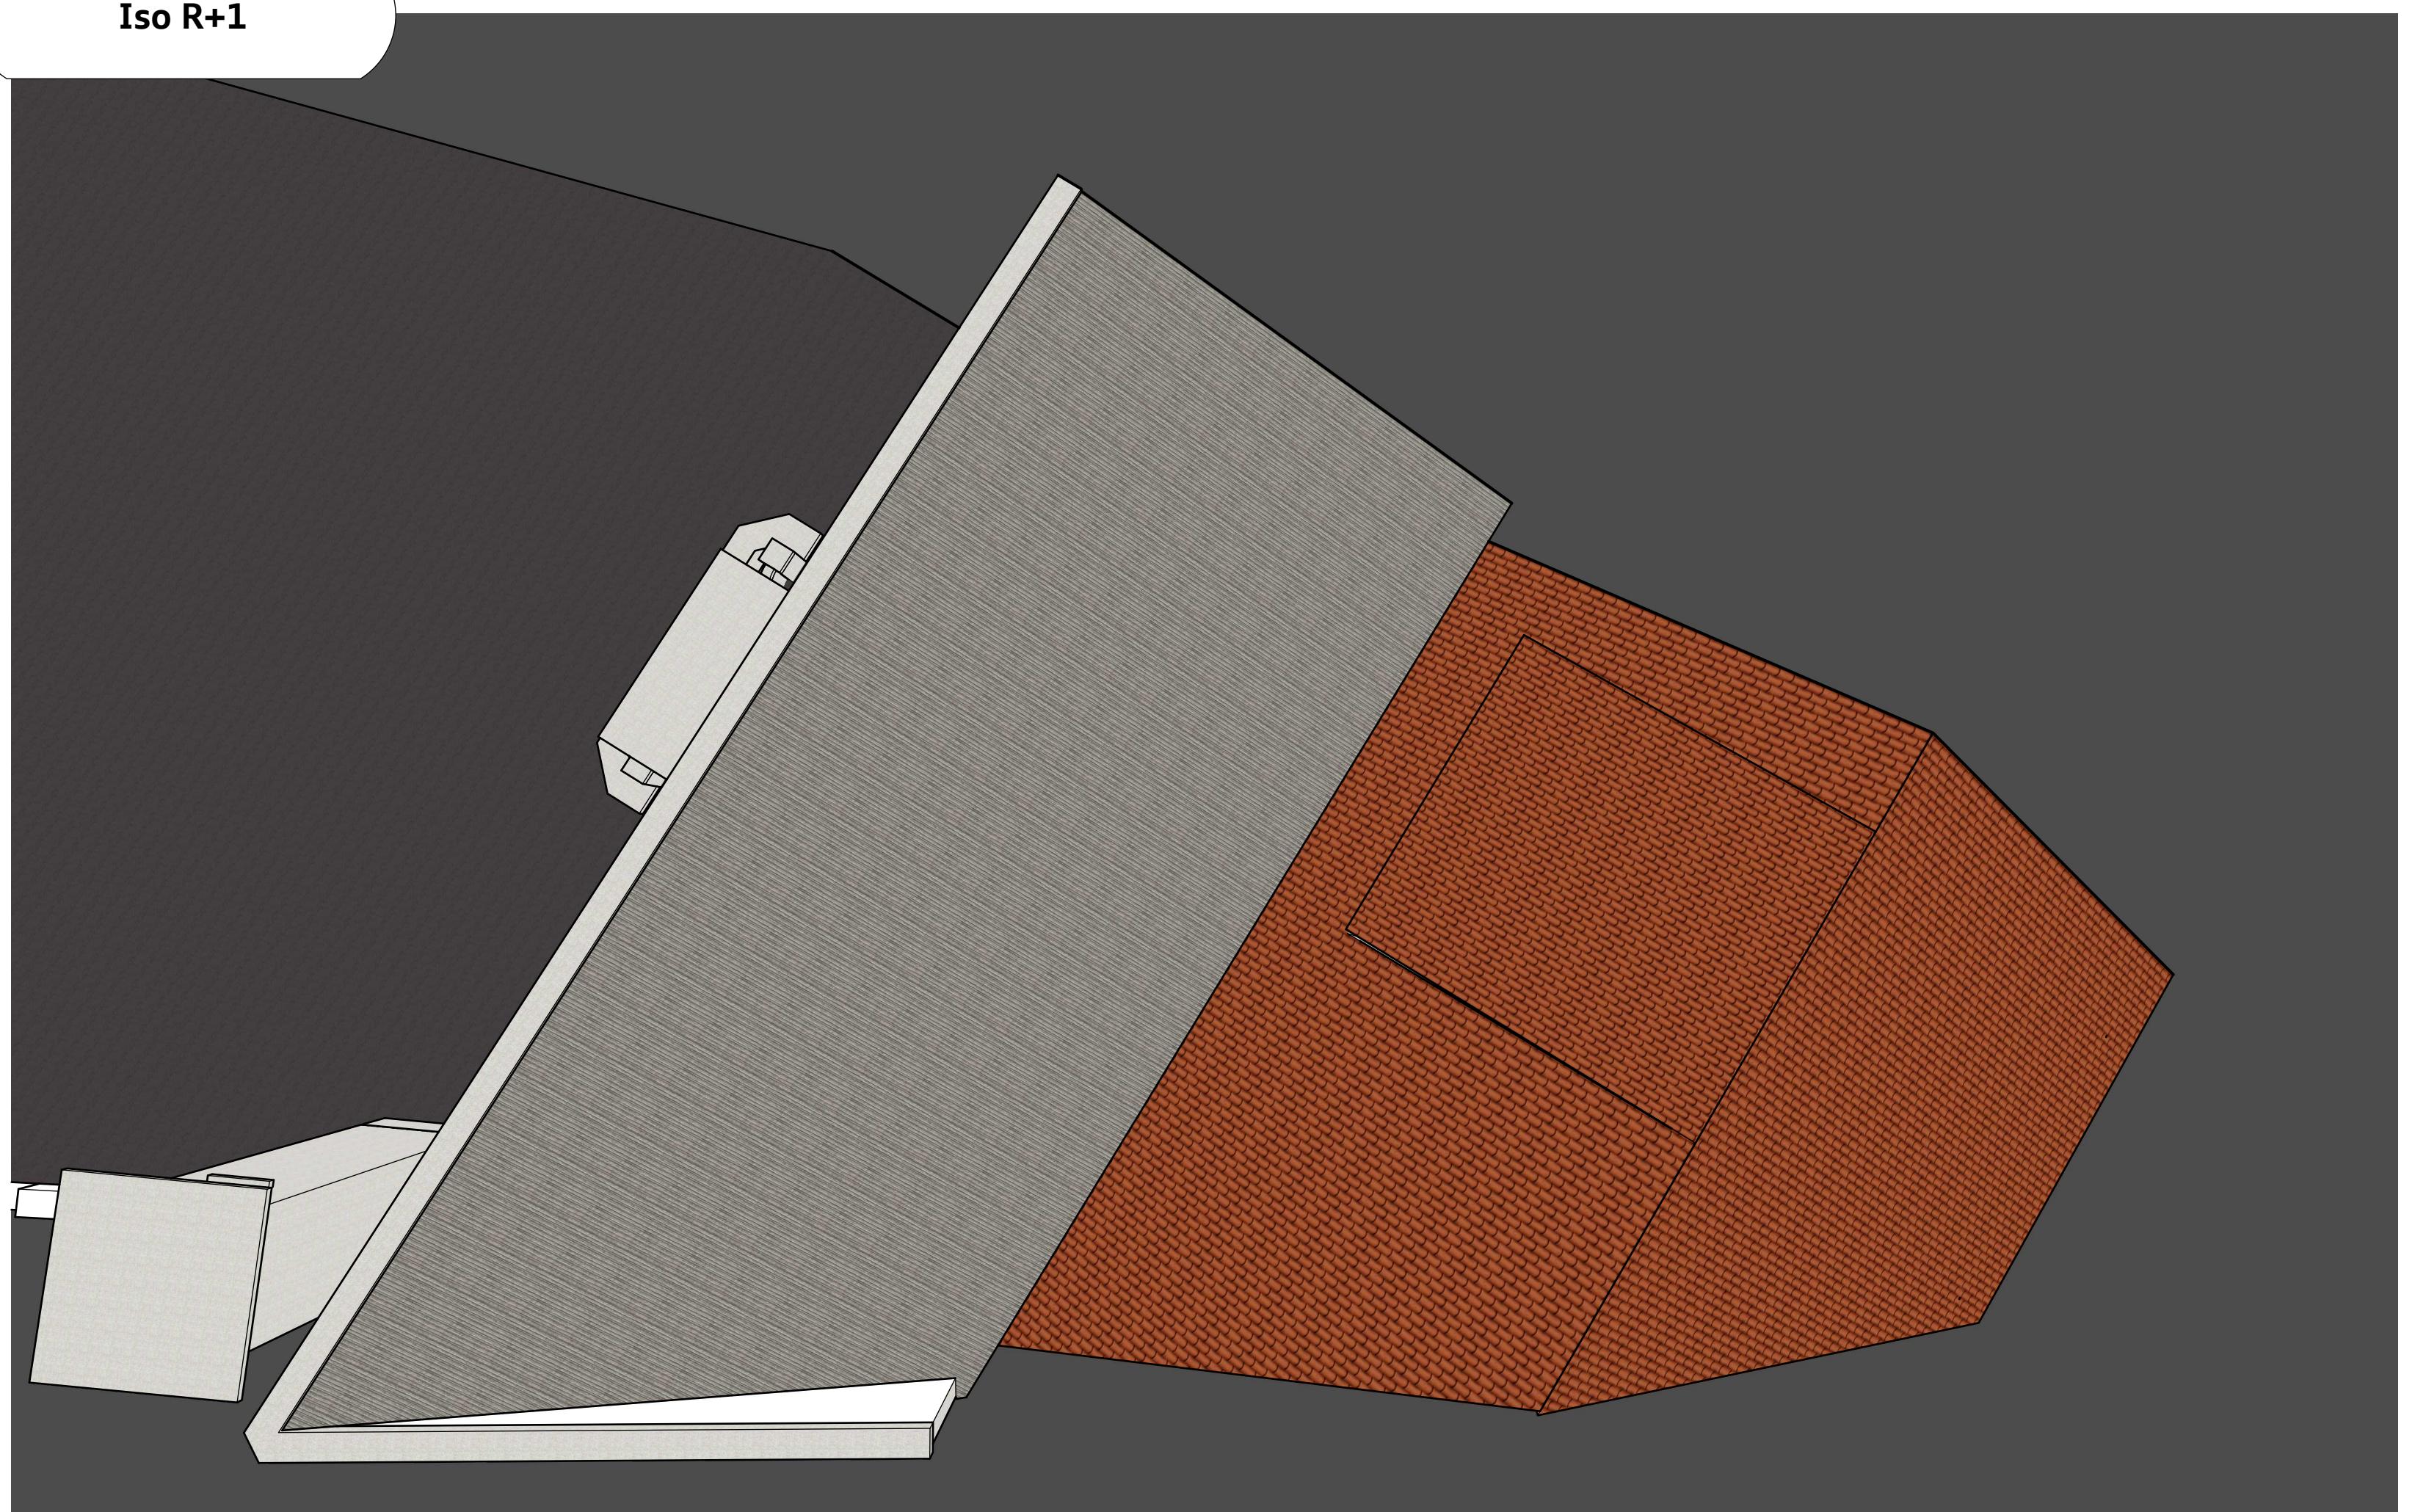

Iso R 0

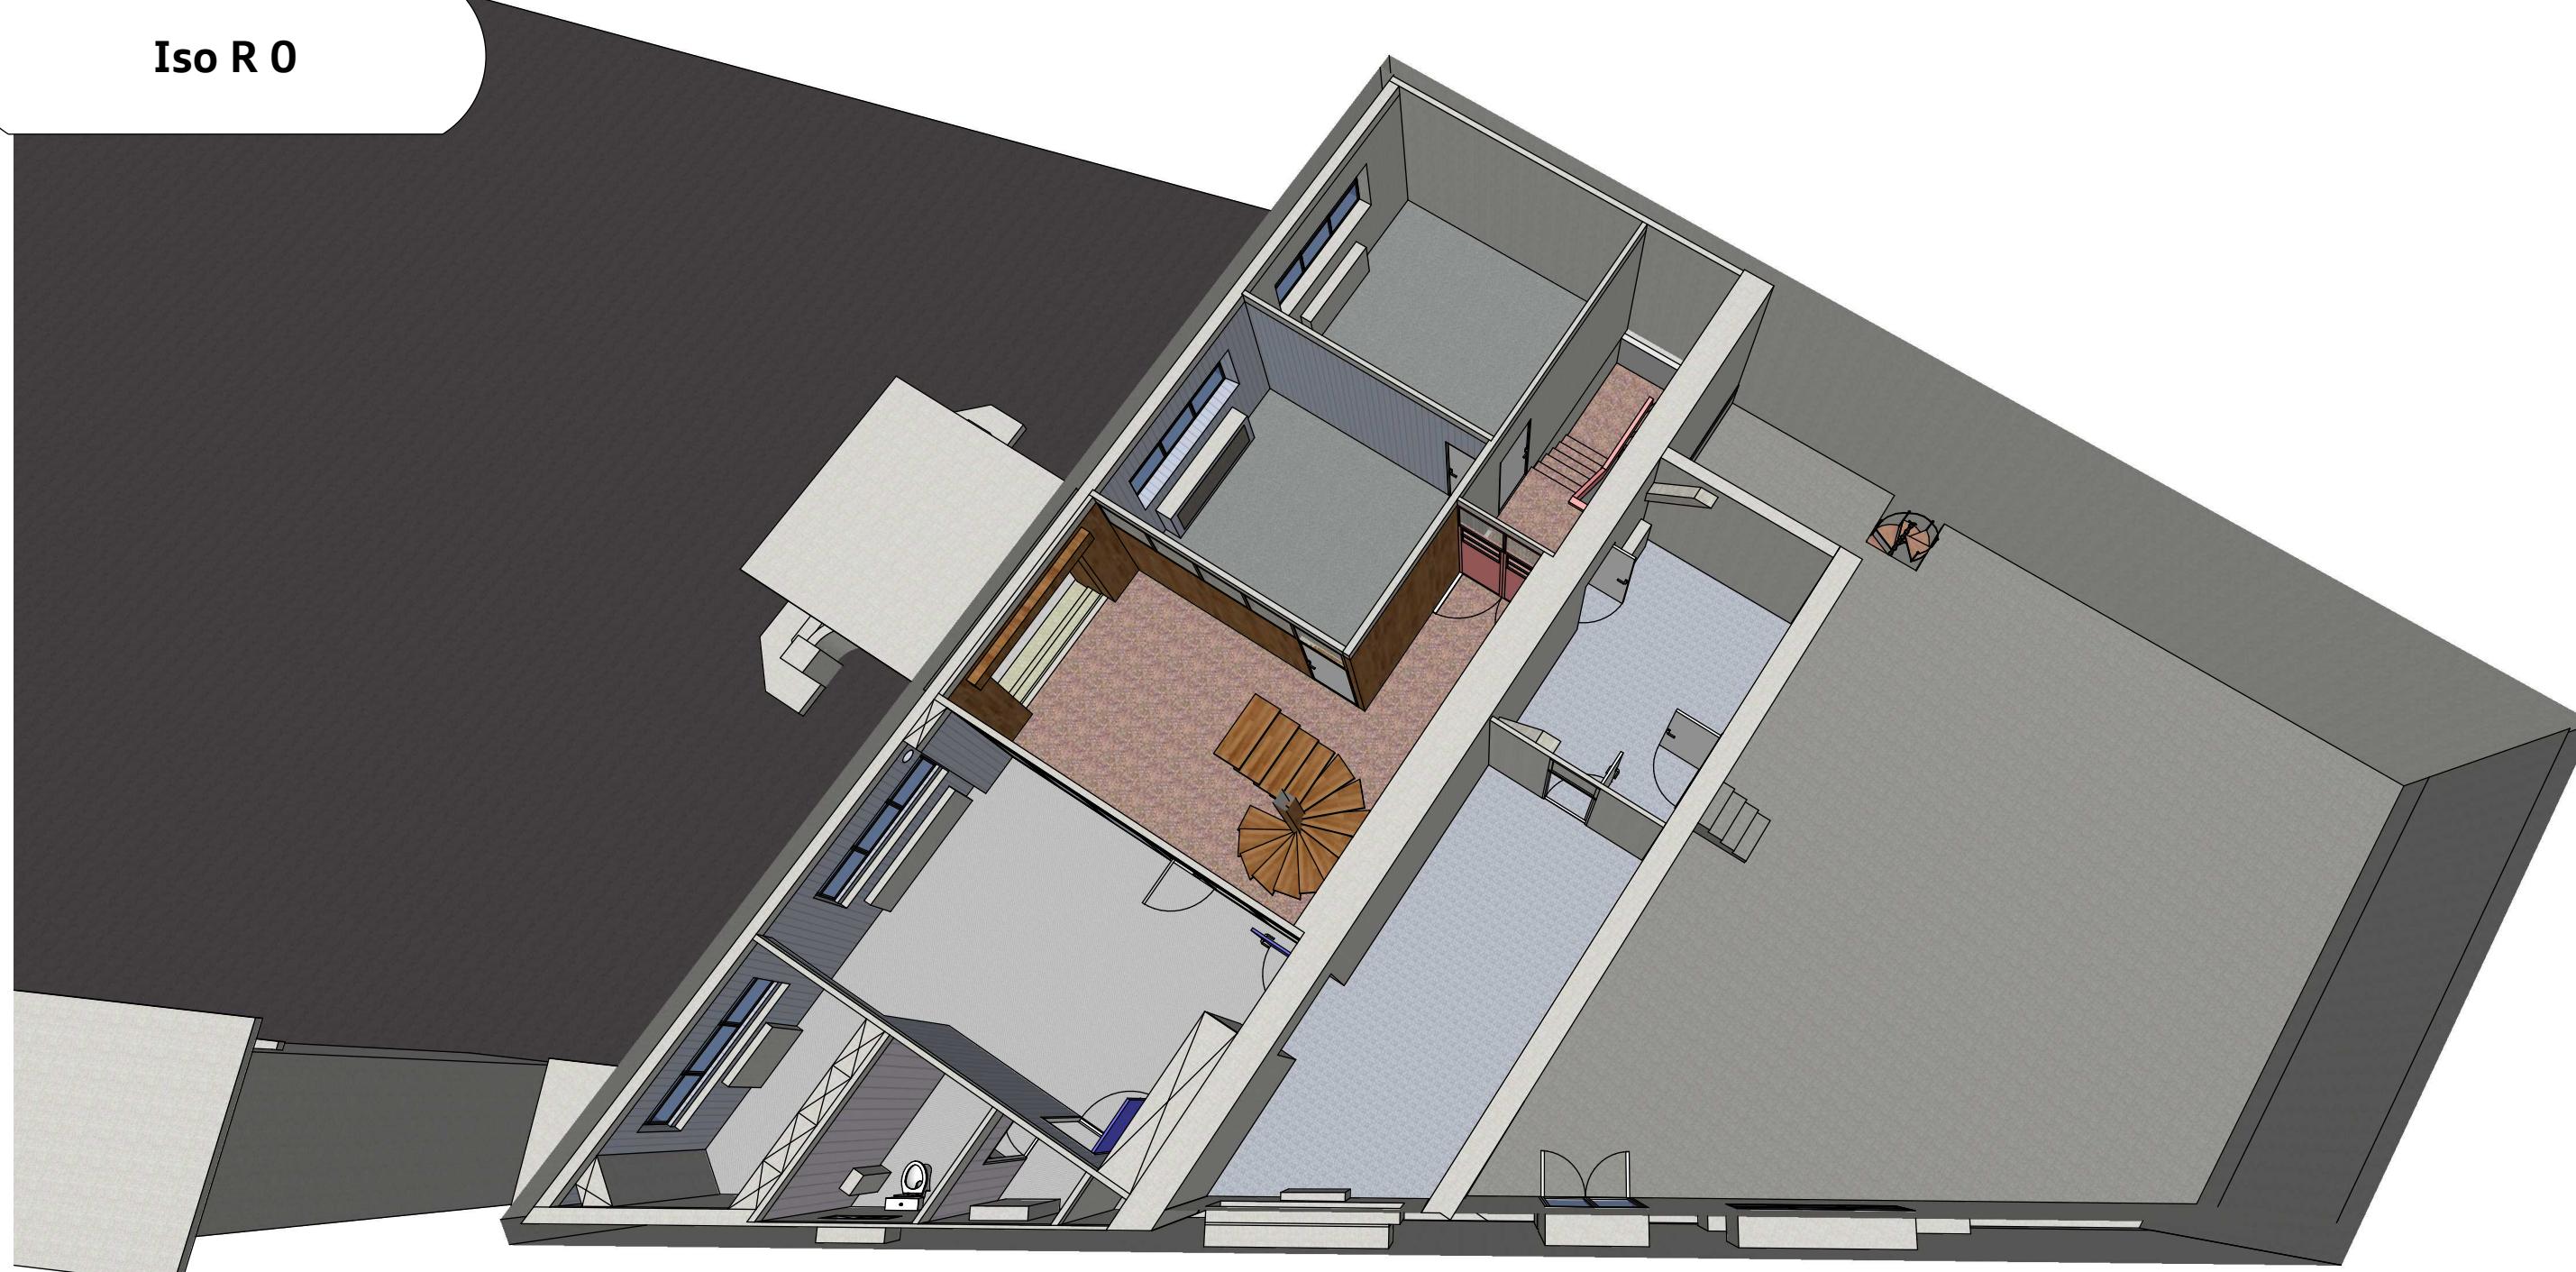

Iso R-1

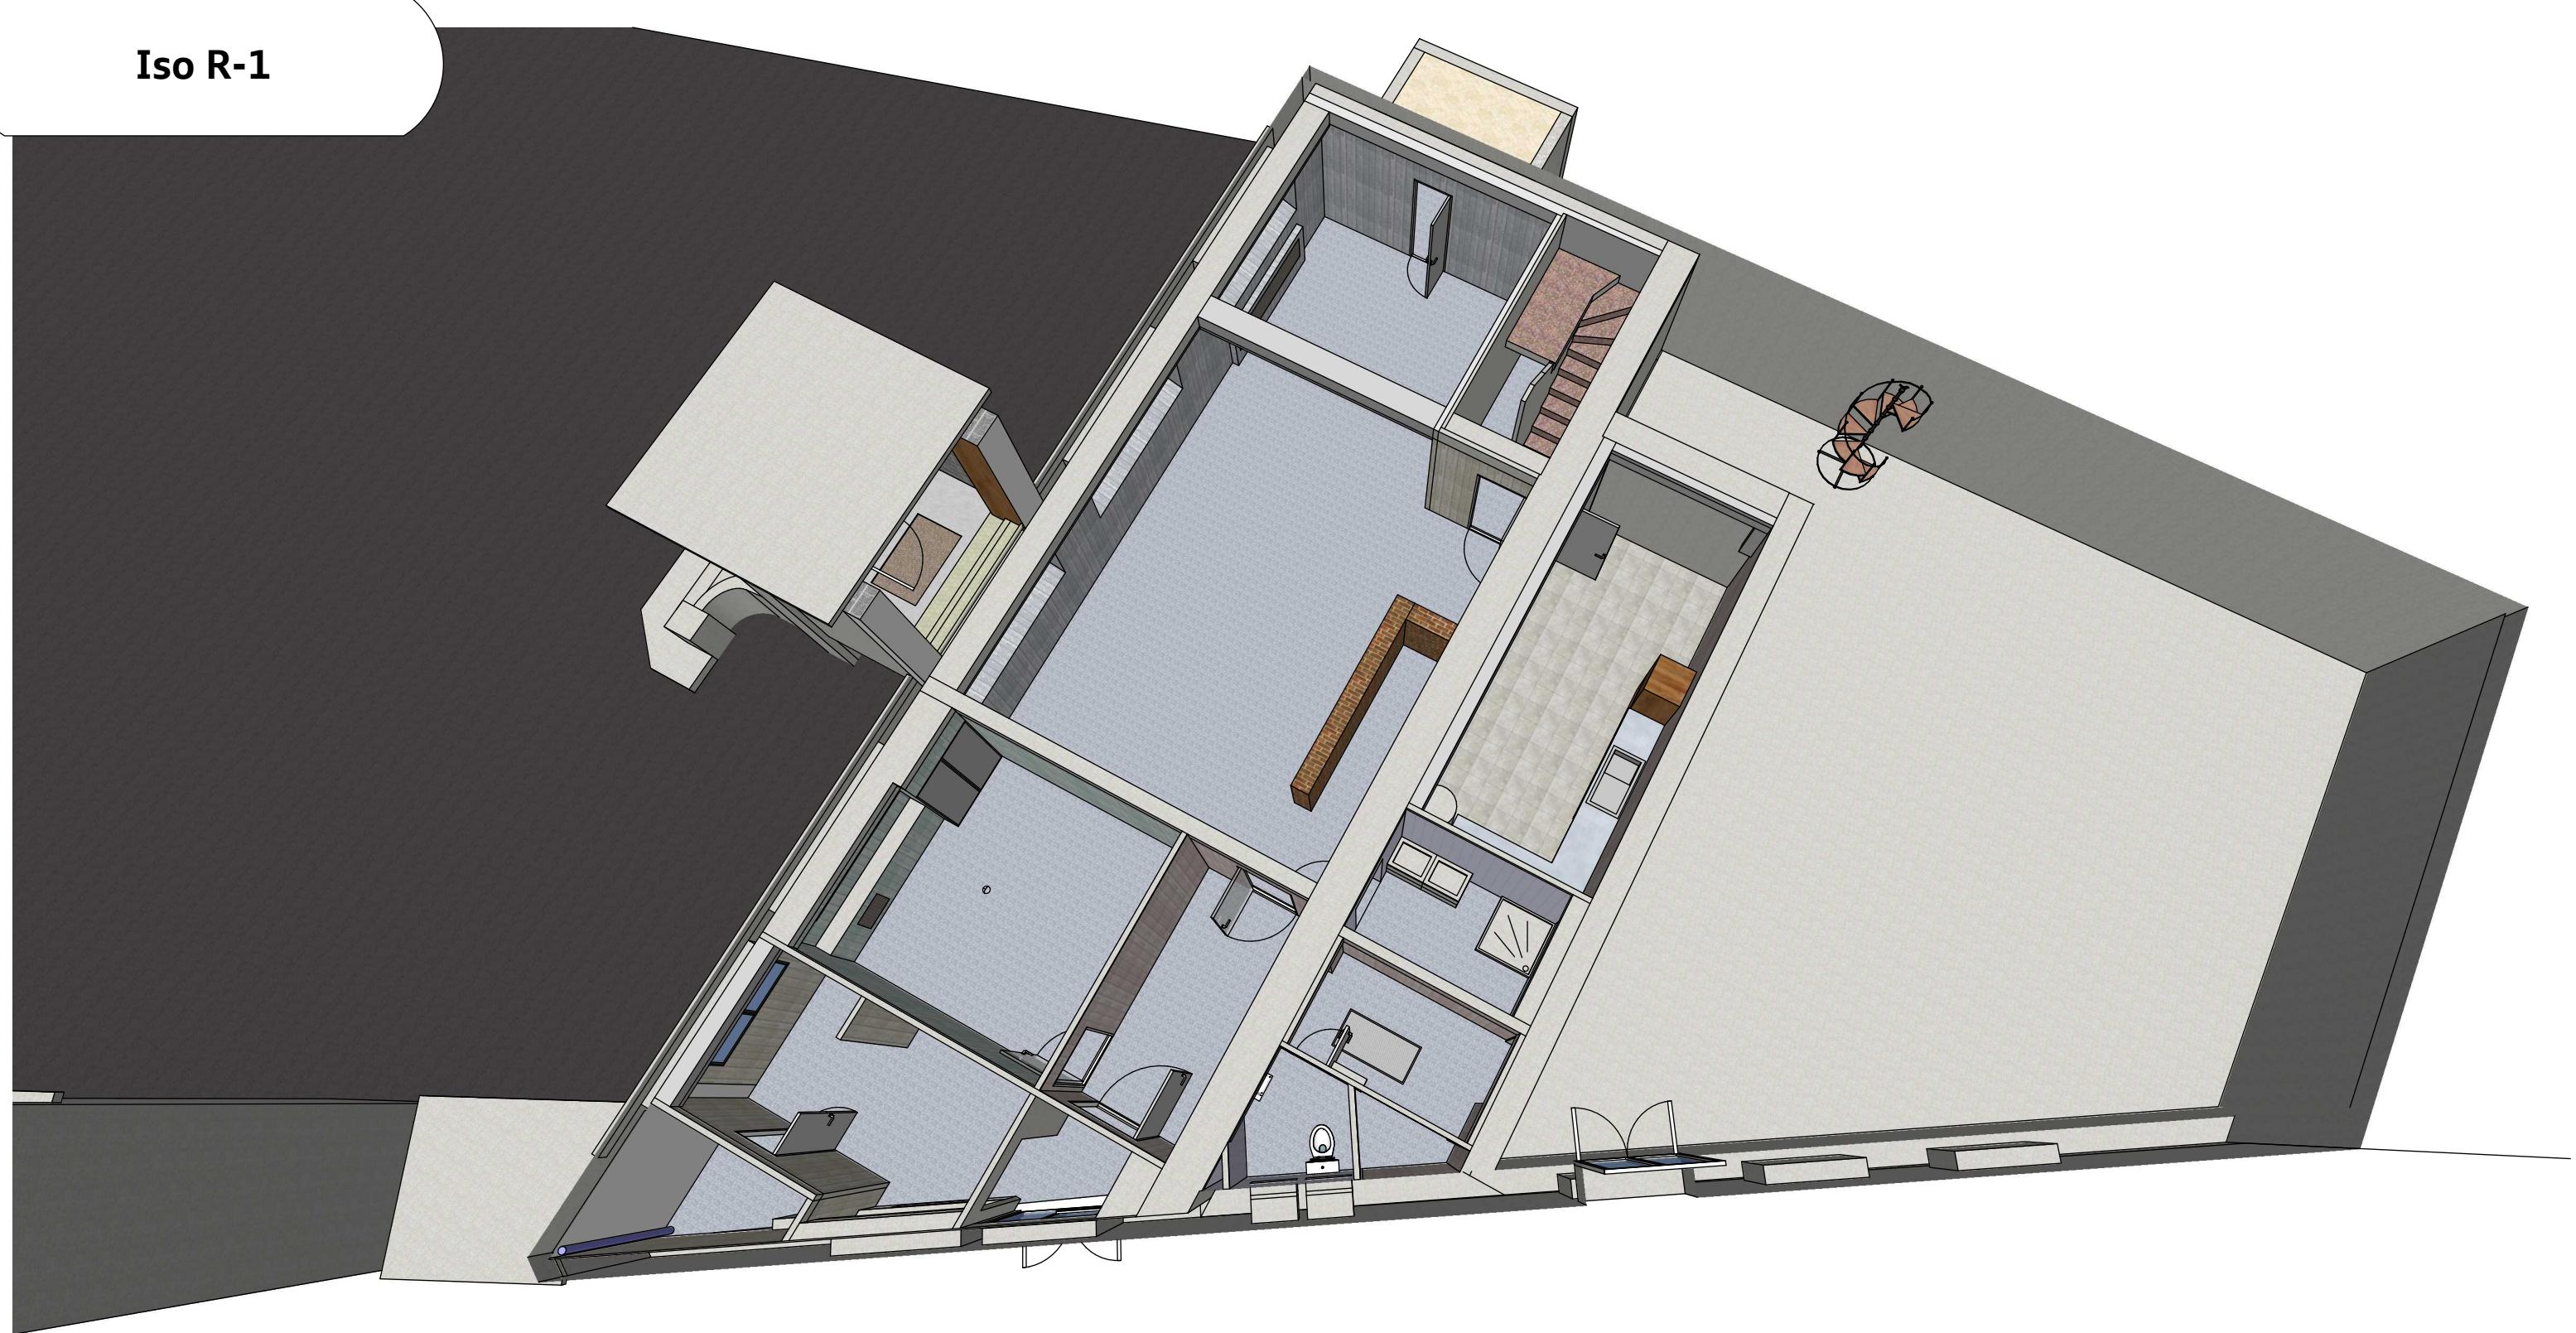

**AP EI**  
ap.bureau.etude@gmail.com **1**


12-14 Rue de la Gare Le Mérévillon 91660  
Résidence Le DUC d'Uber

Plan état existant - Localisation / Toitures / Iso  
Echelle : ....

Dernière modification : 14/12/2023  
Révision : v0.03


Voir le Bâtiment en 3D [YouTube](#)

Aerial map showing the building's location in Le Mérévillon, 91660.

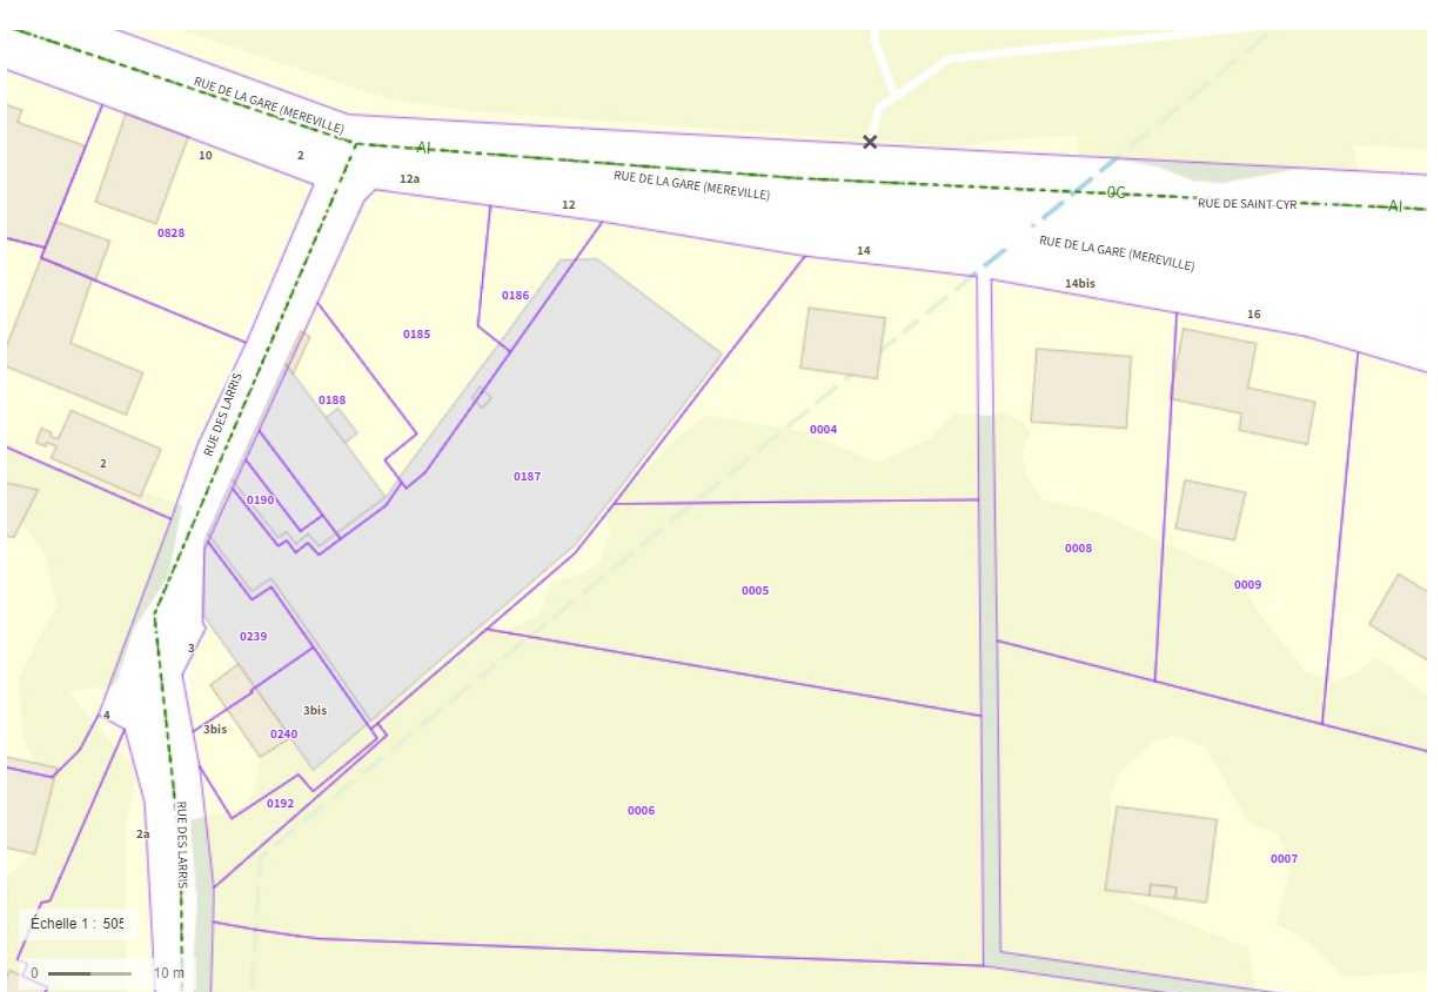



Façade Est  
1/50

Façade Sud  
1/50

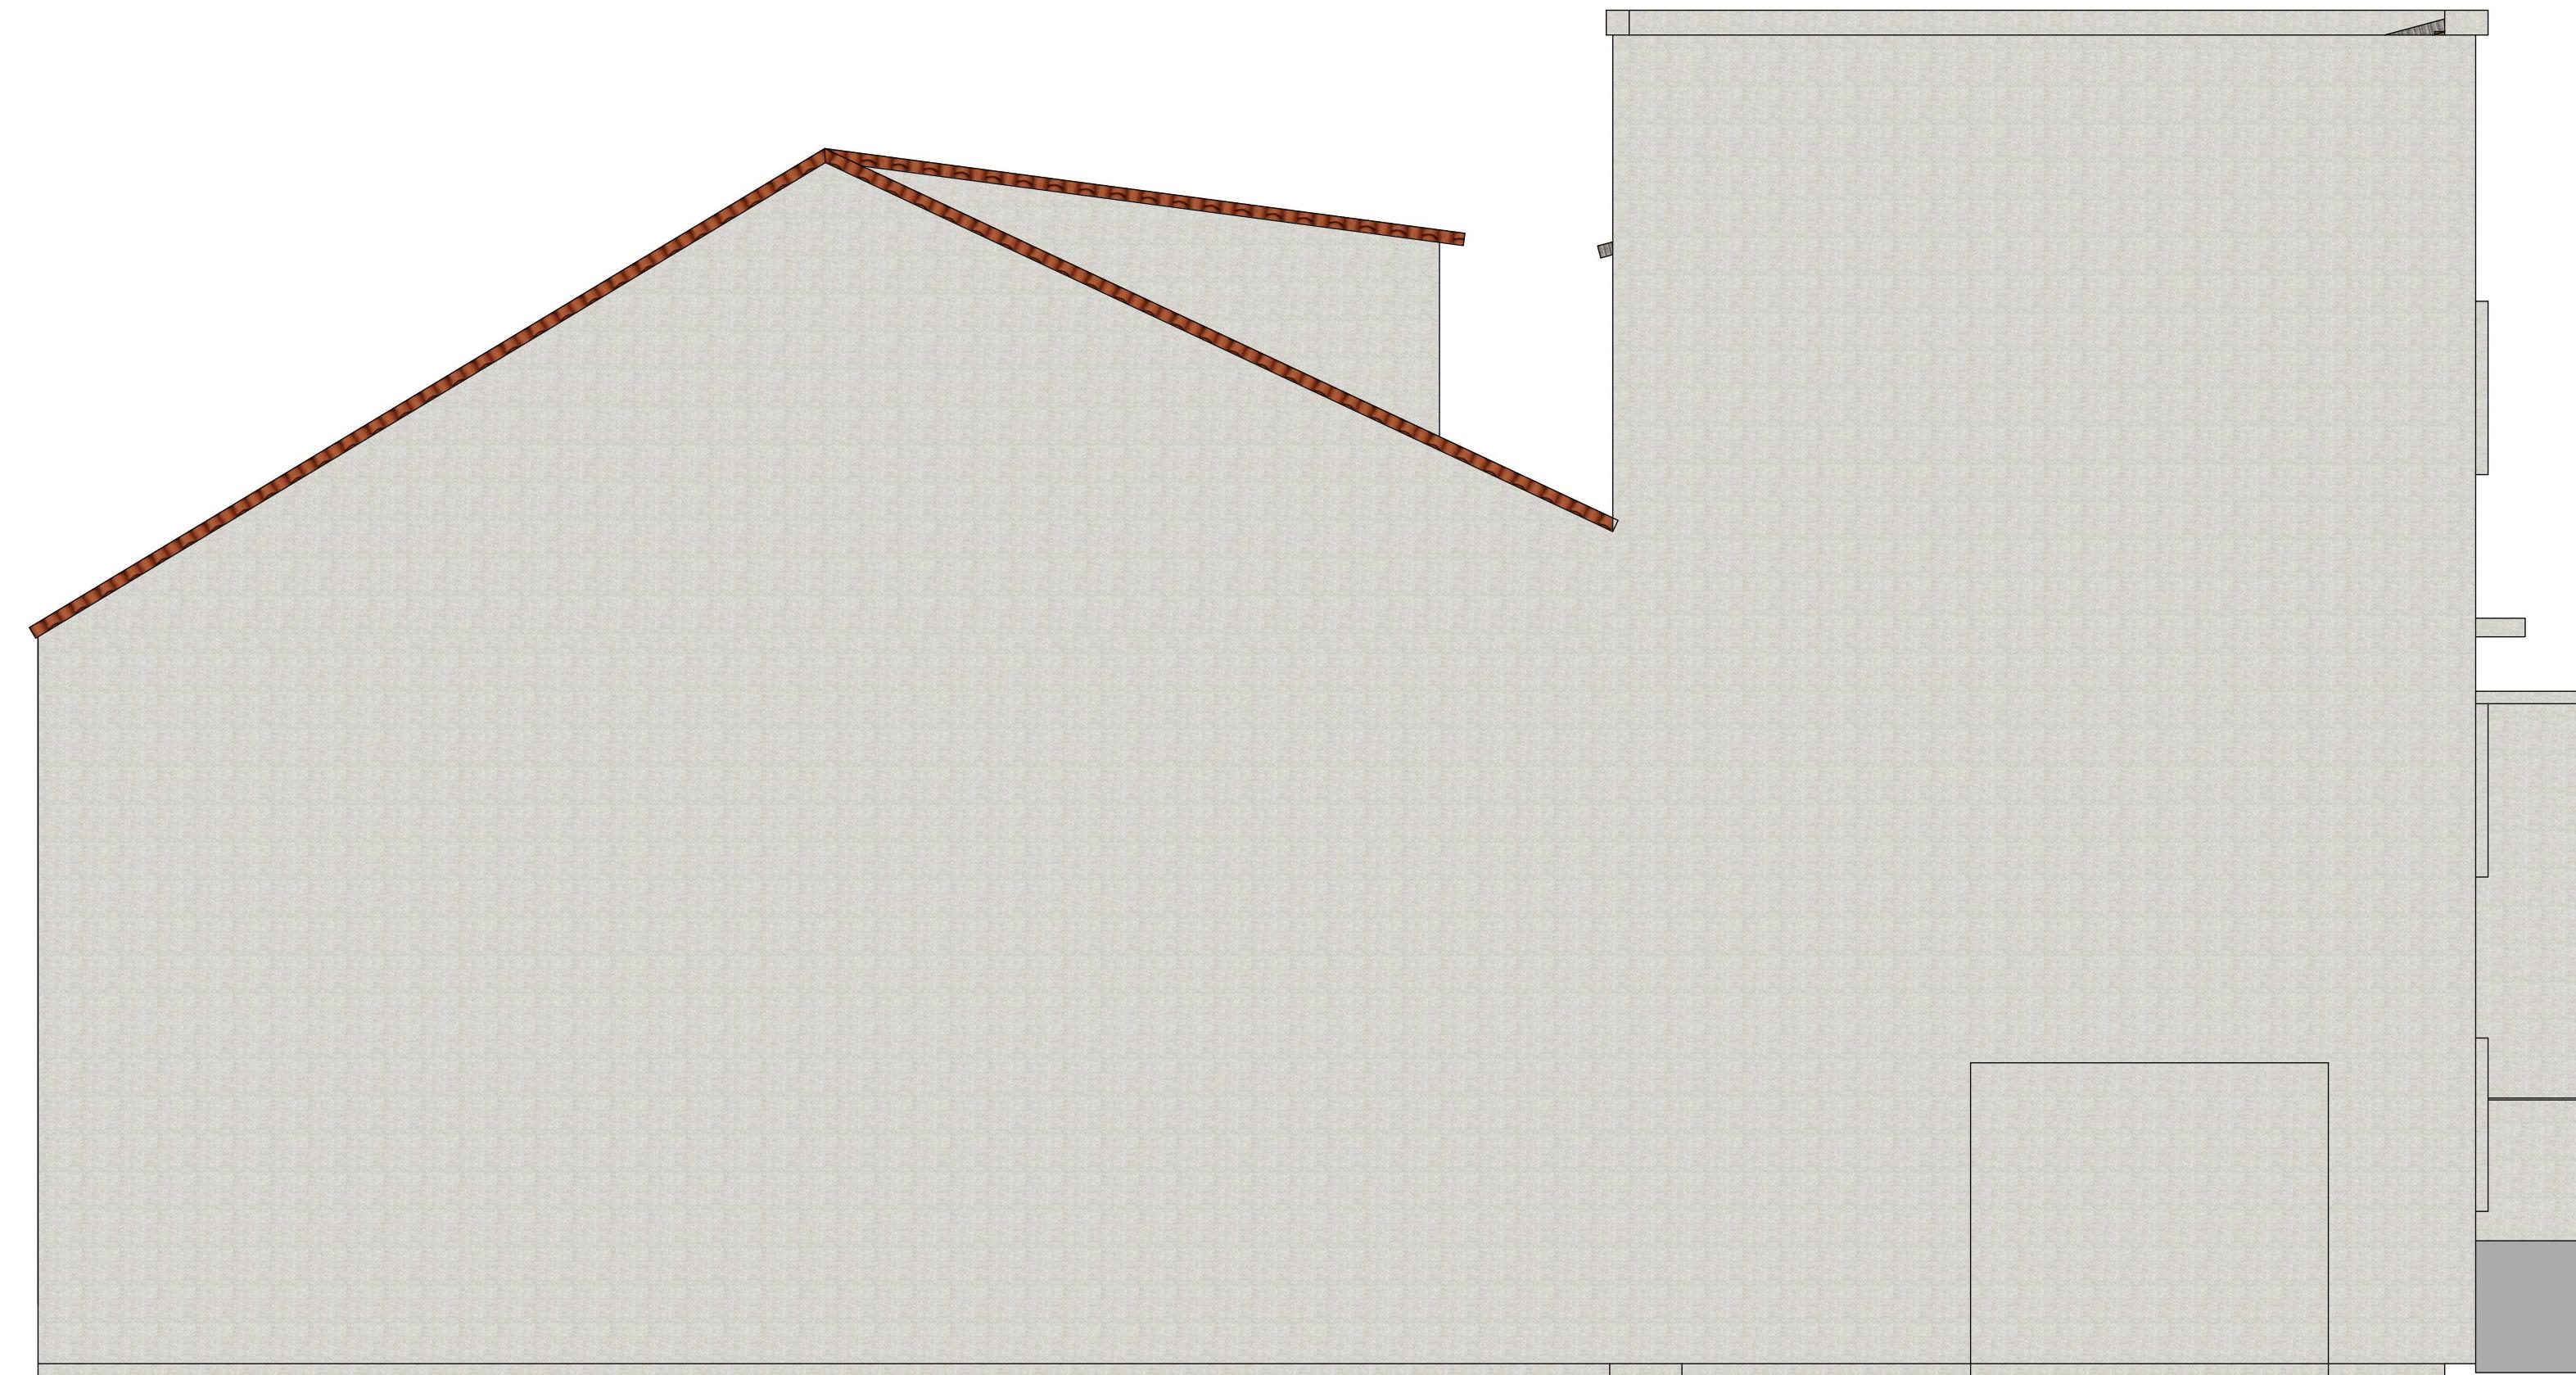


Façade Ouest  
1/50

Façade Nord  
1/50

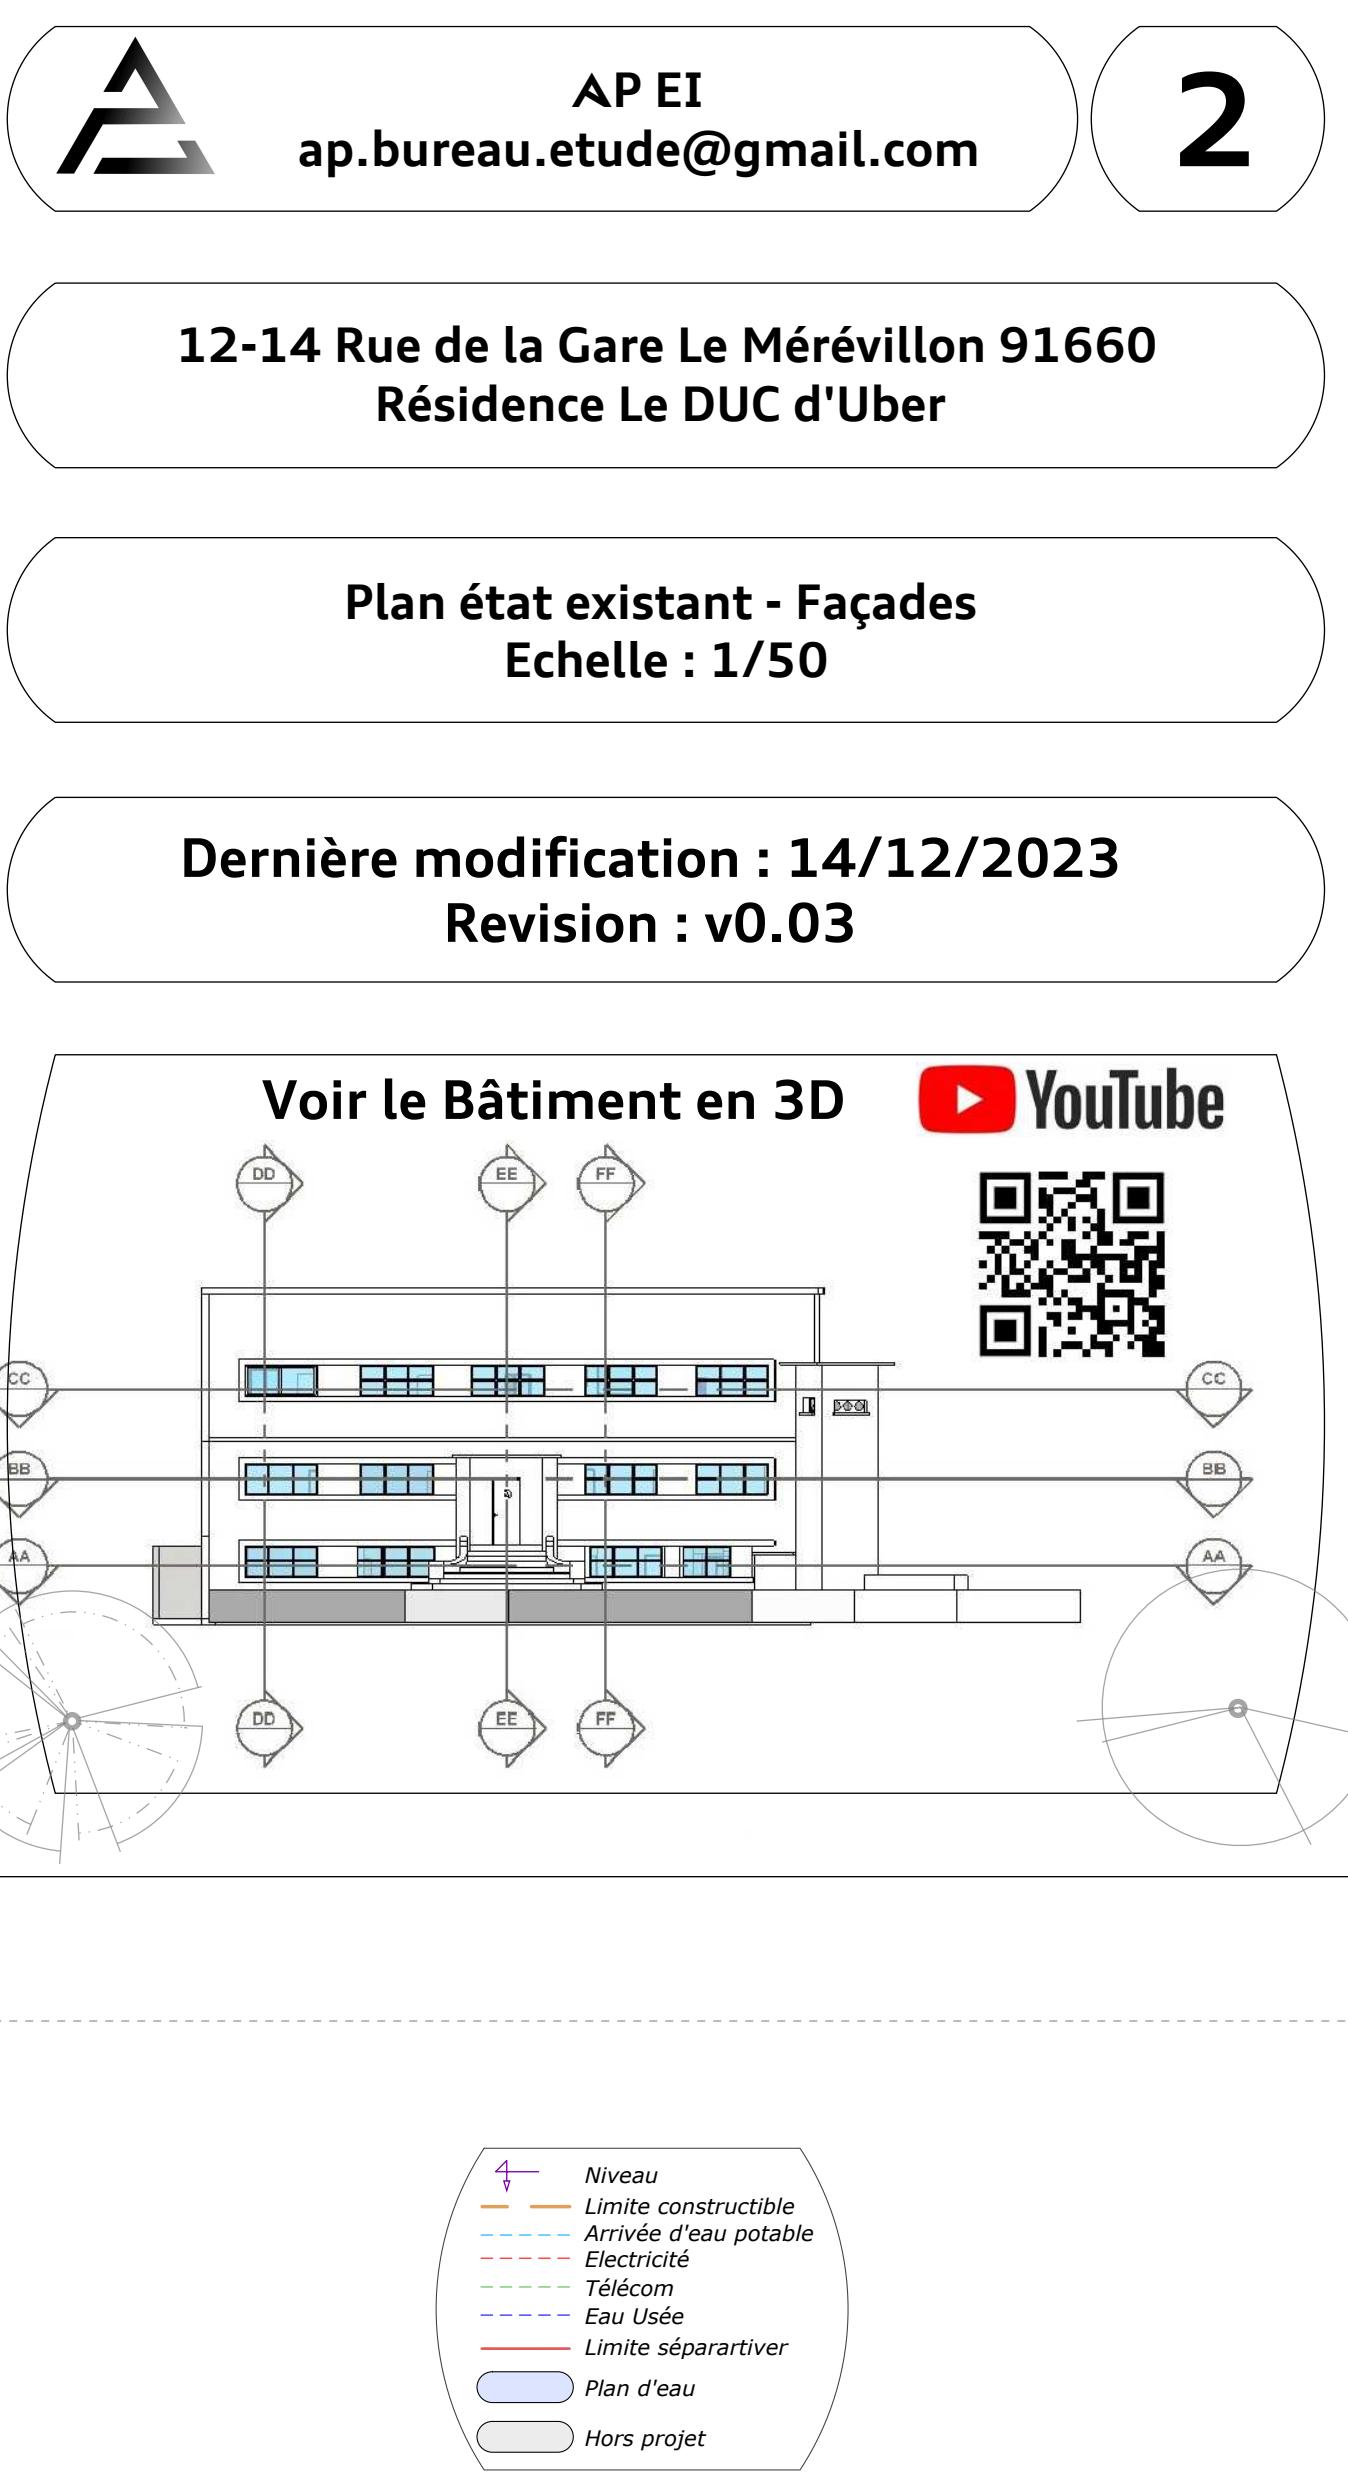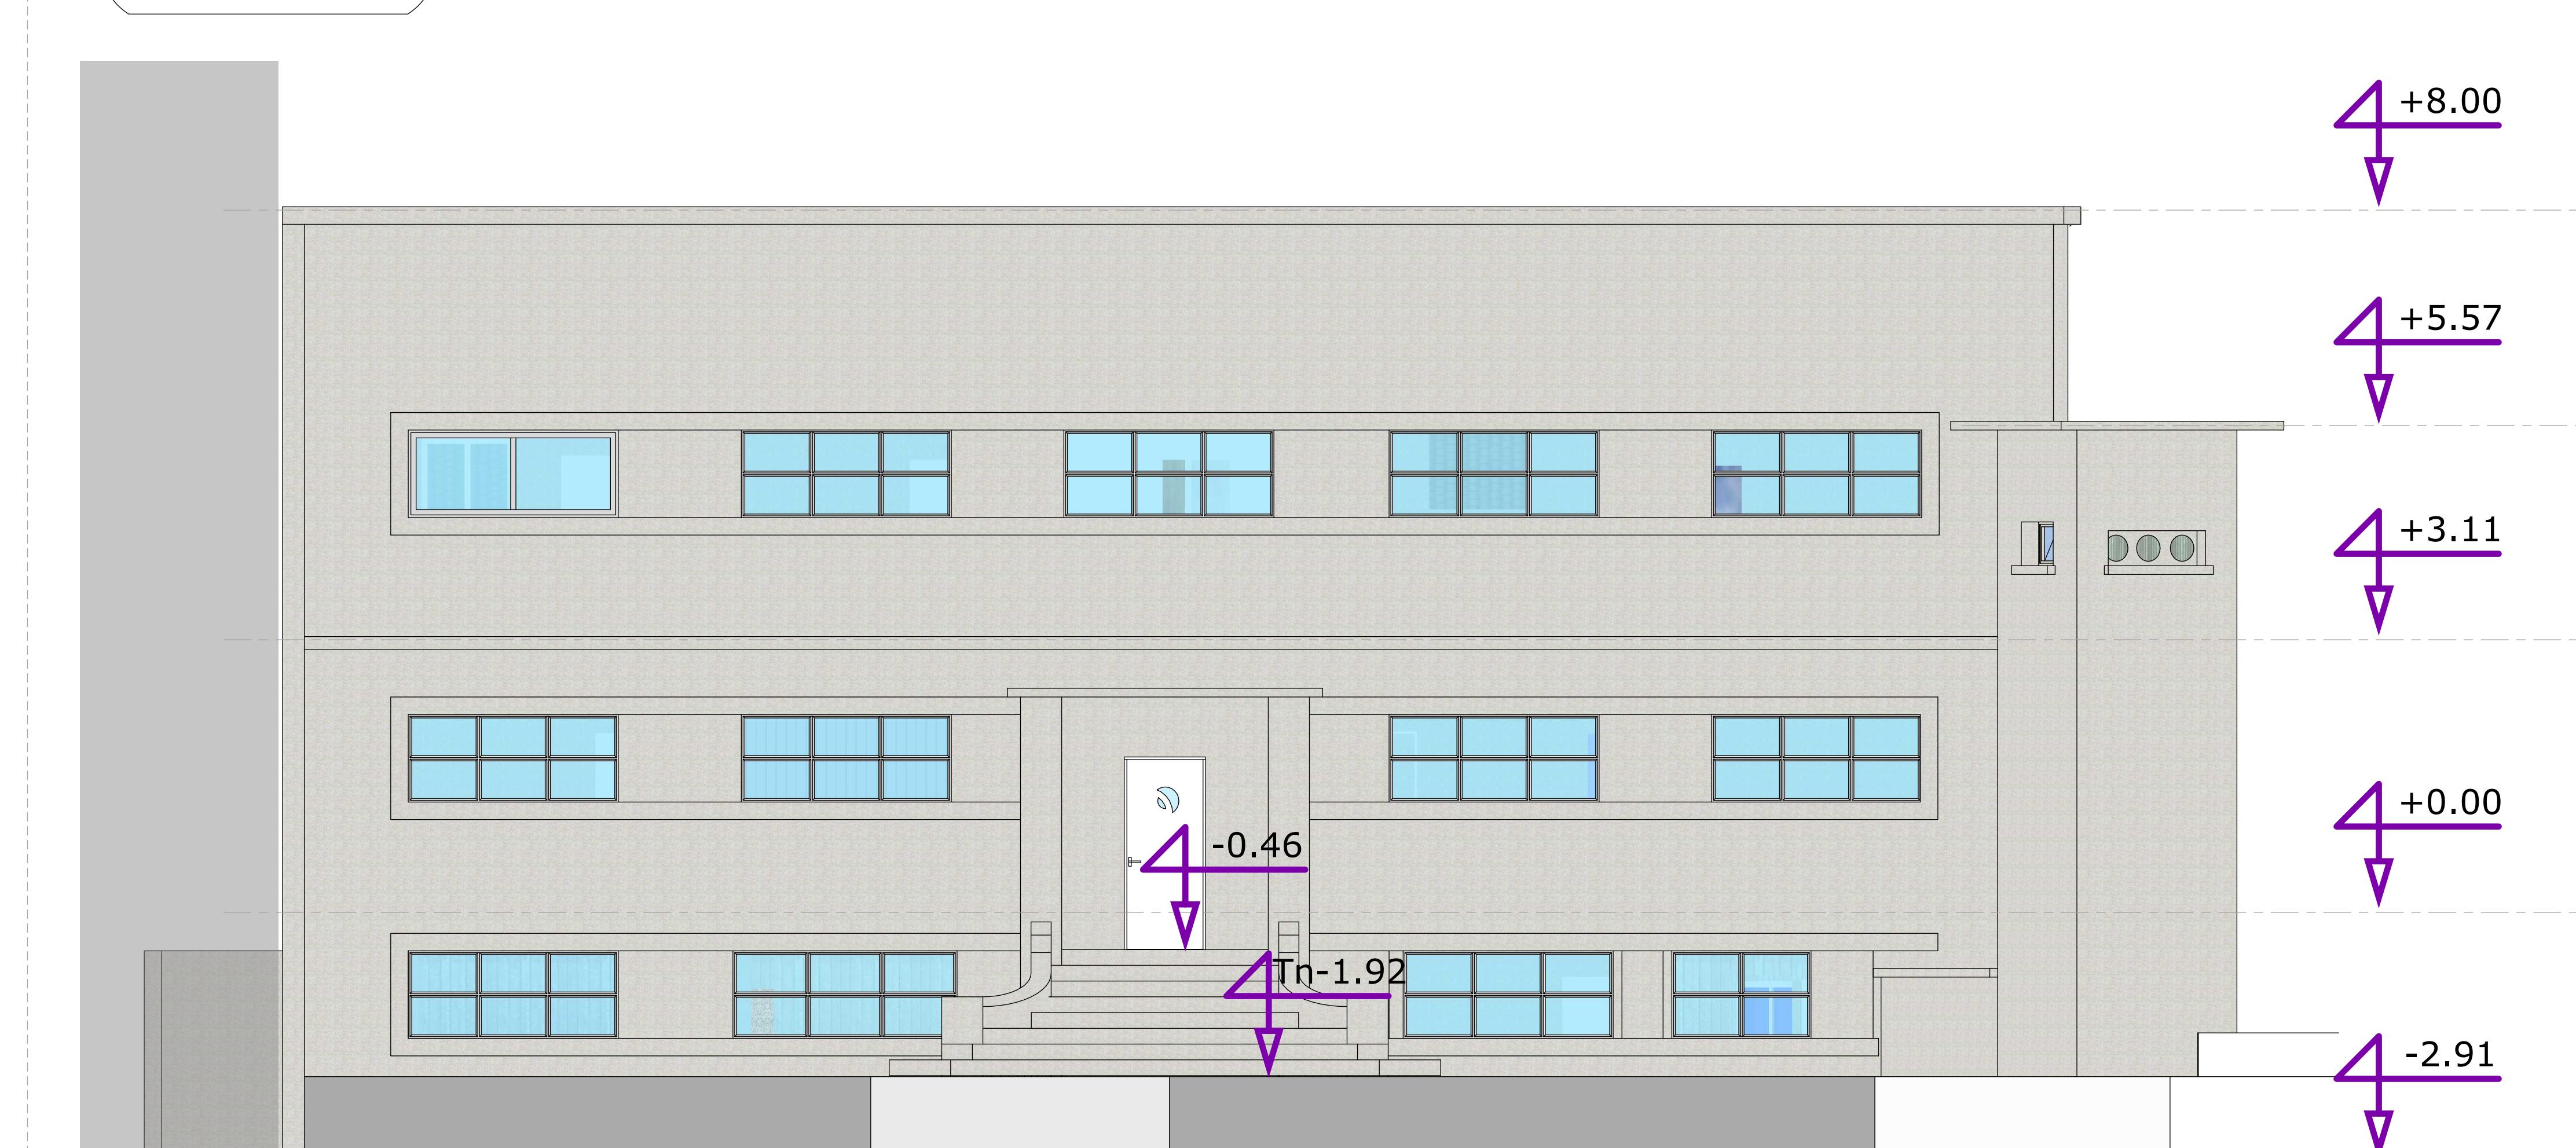


Coupe DD  
1/50

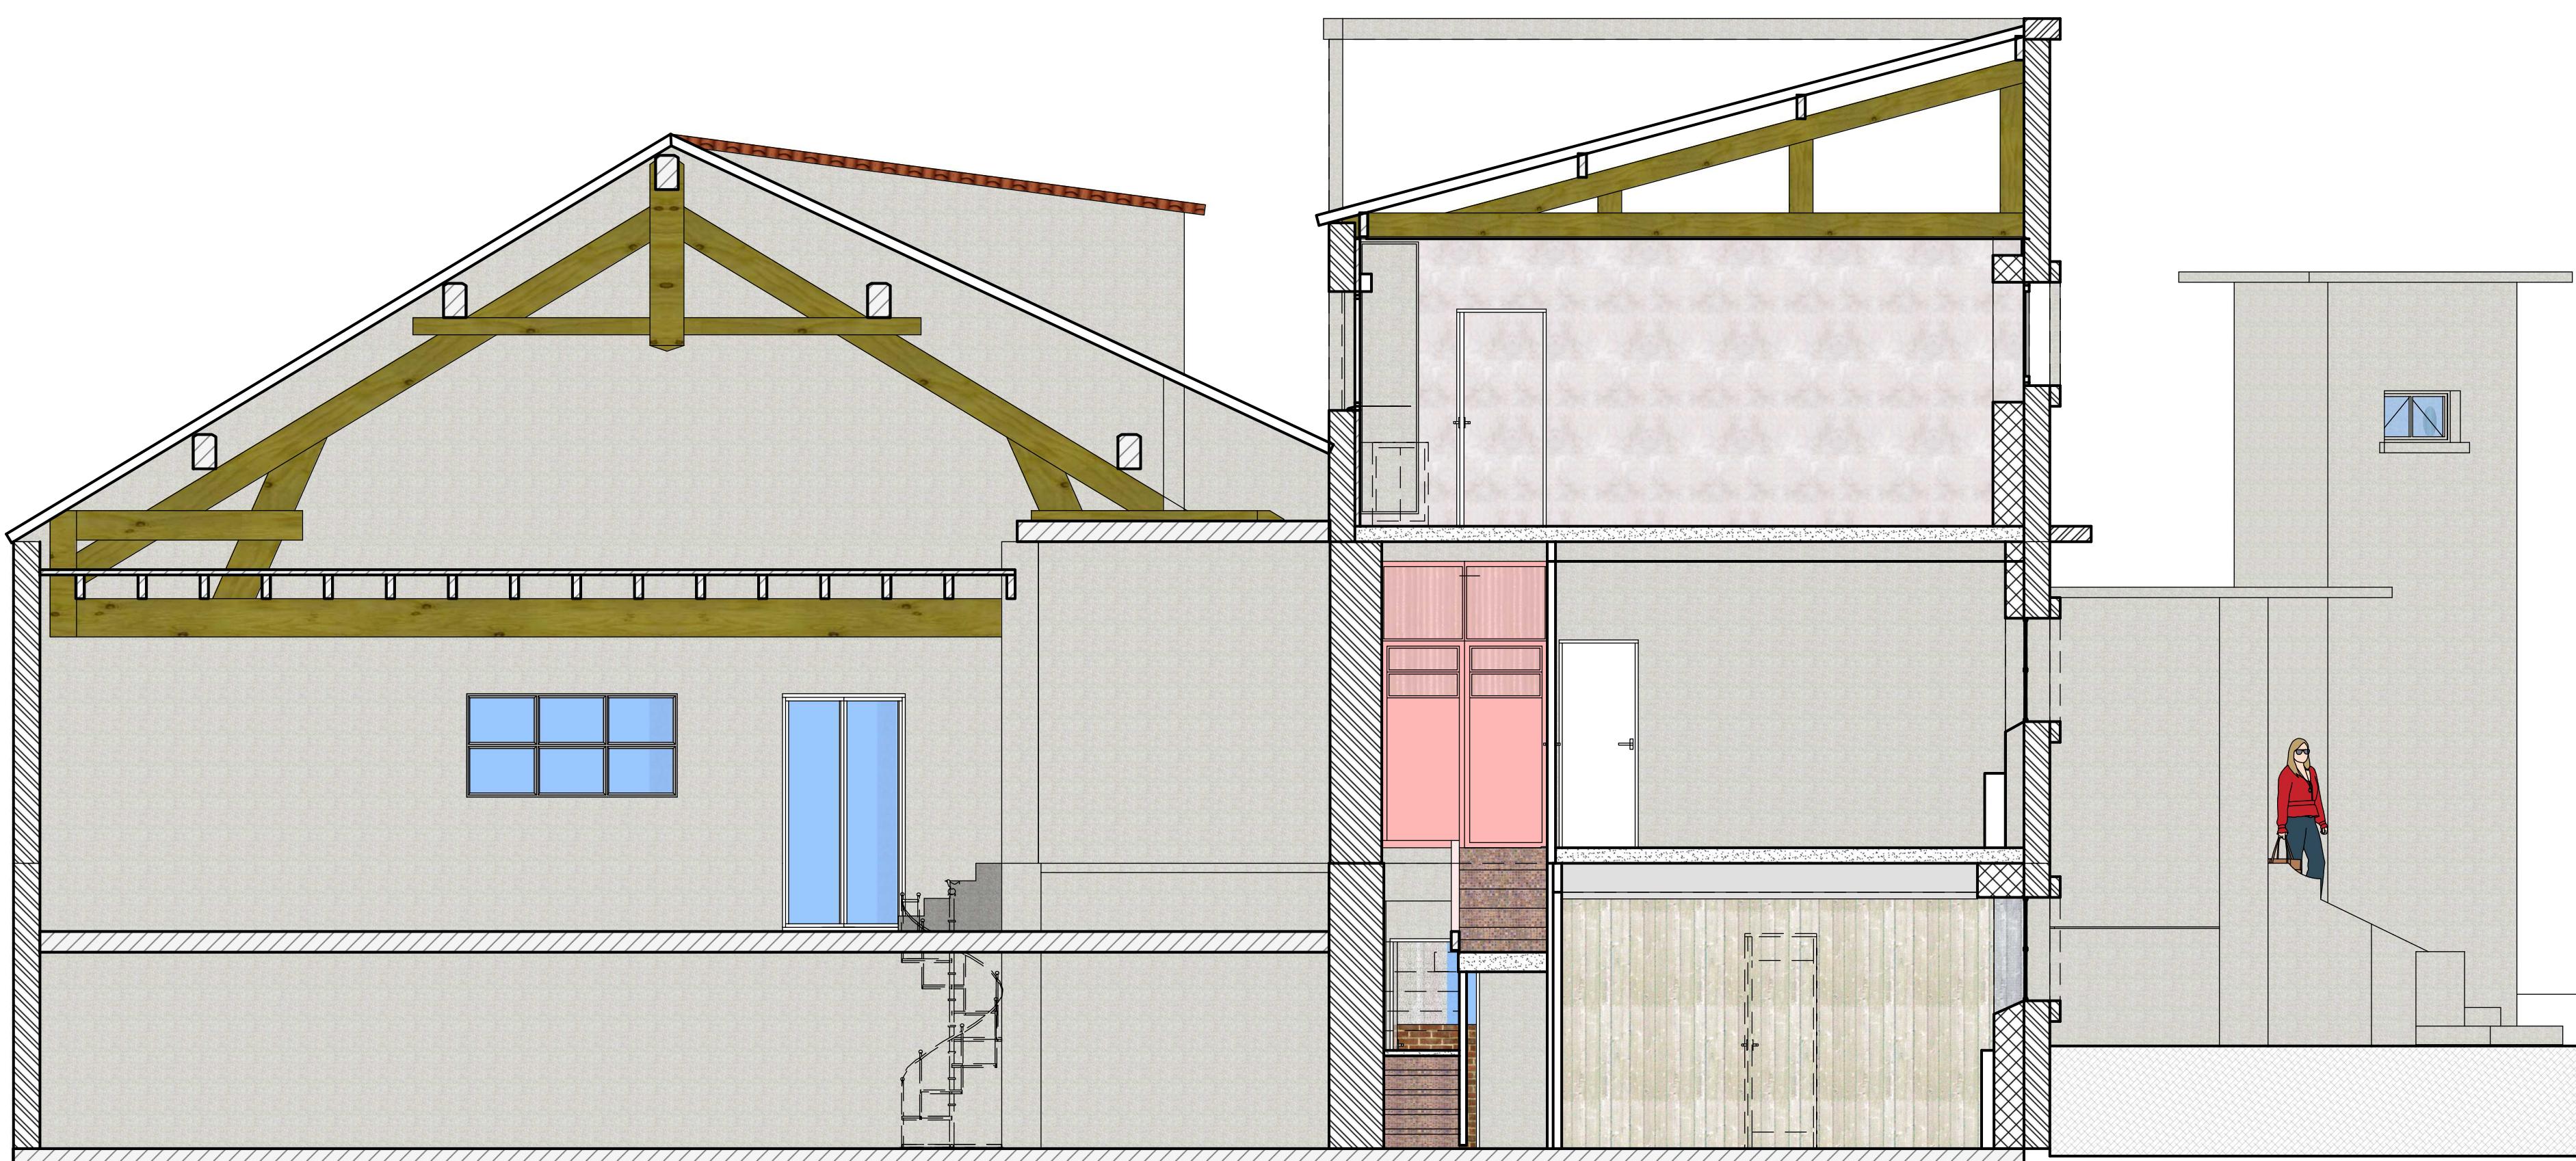


Coupe FF  
1/50



Coupe EE  
1/50

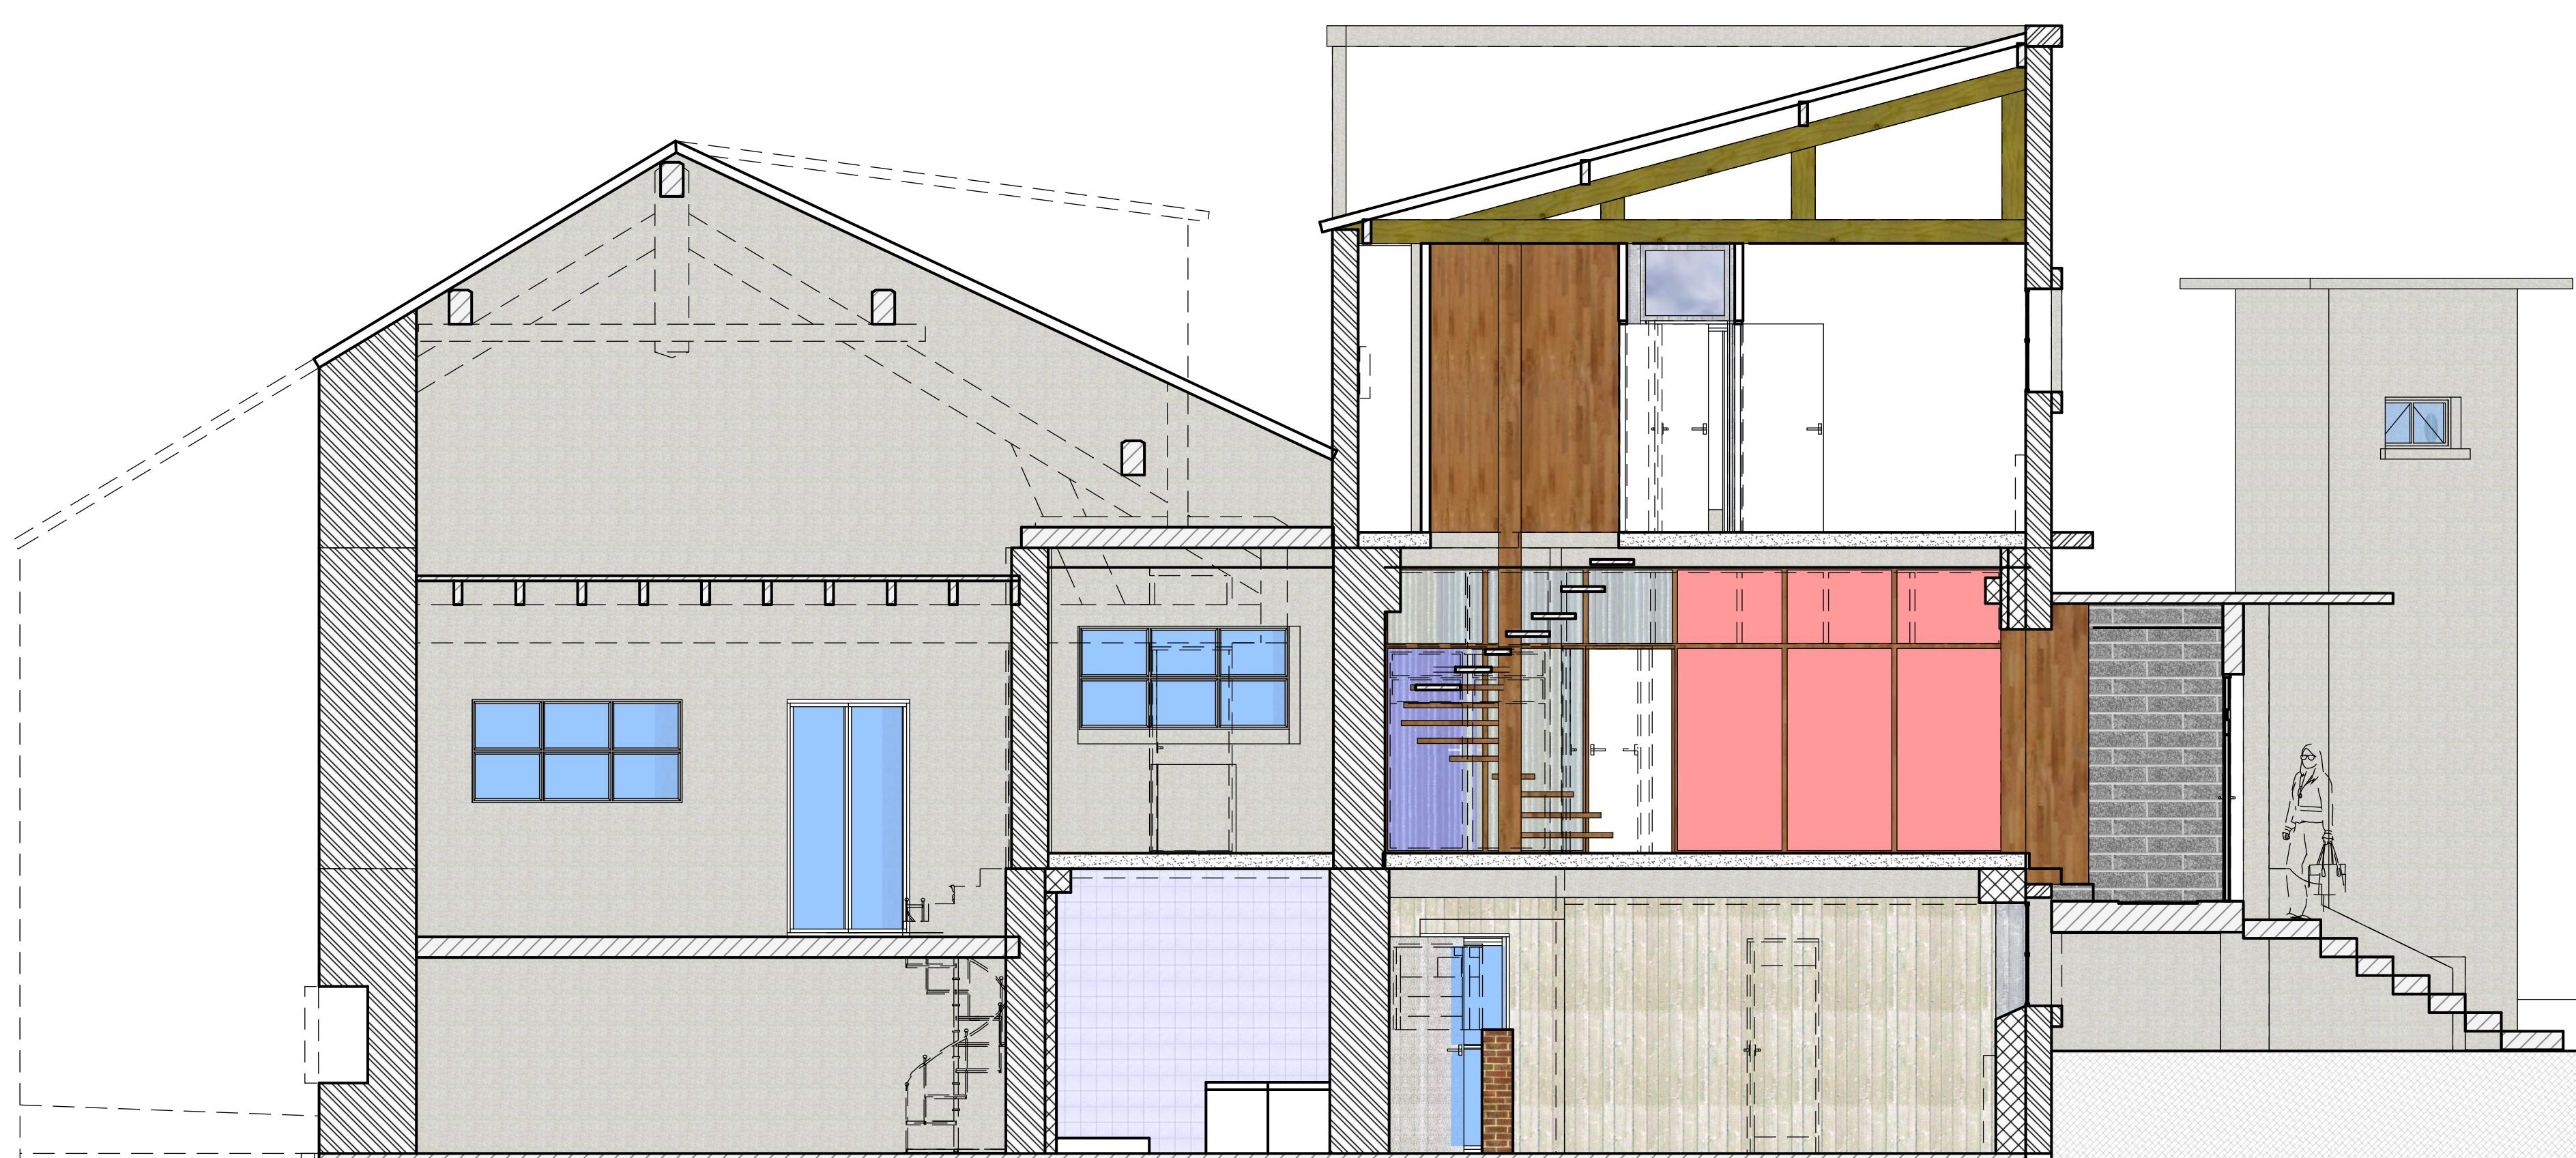

Coupe GG  
1/50

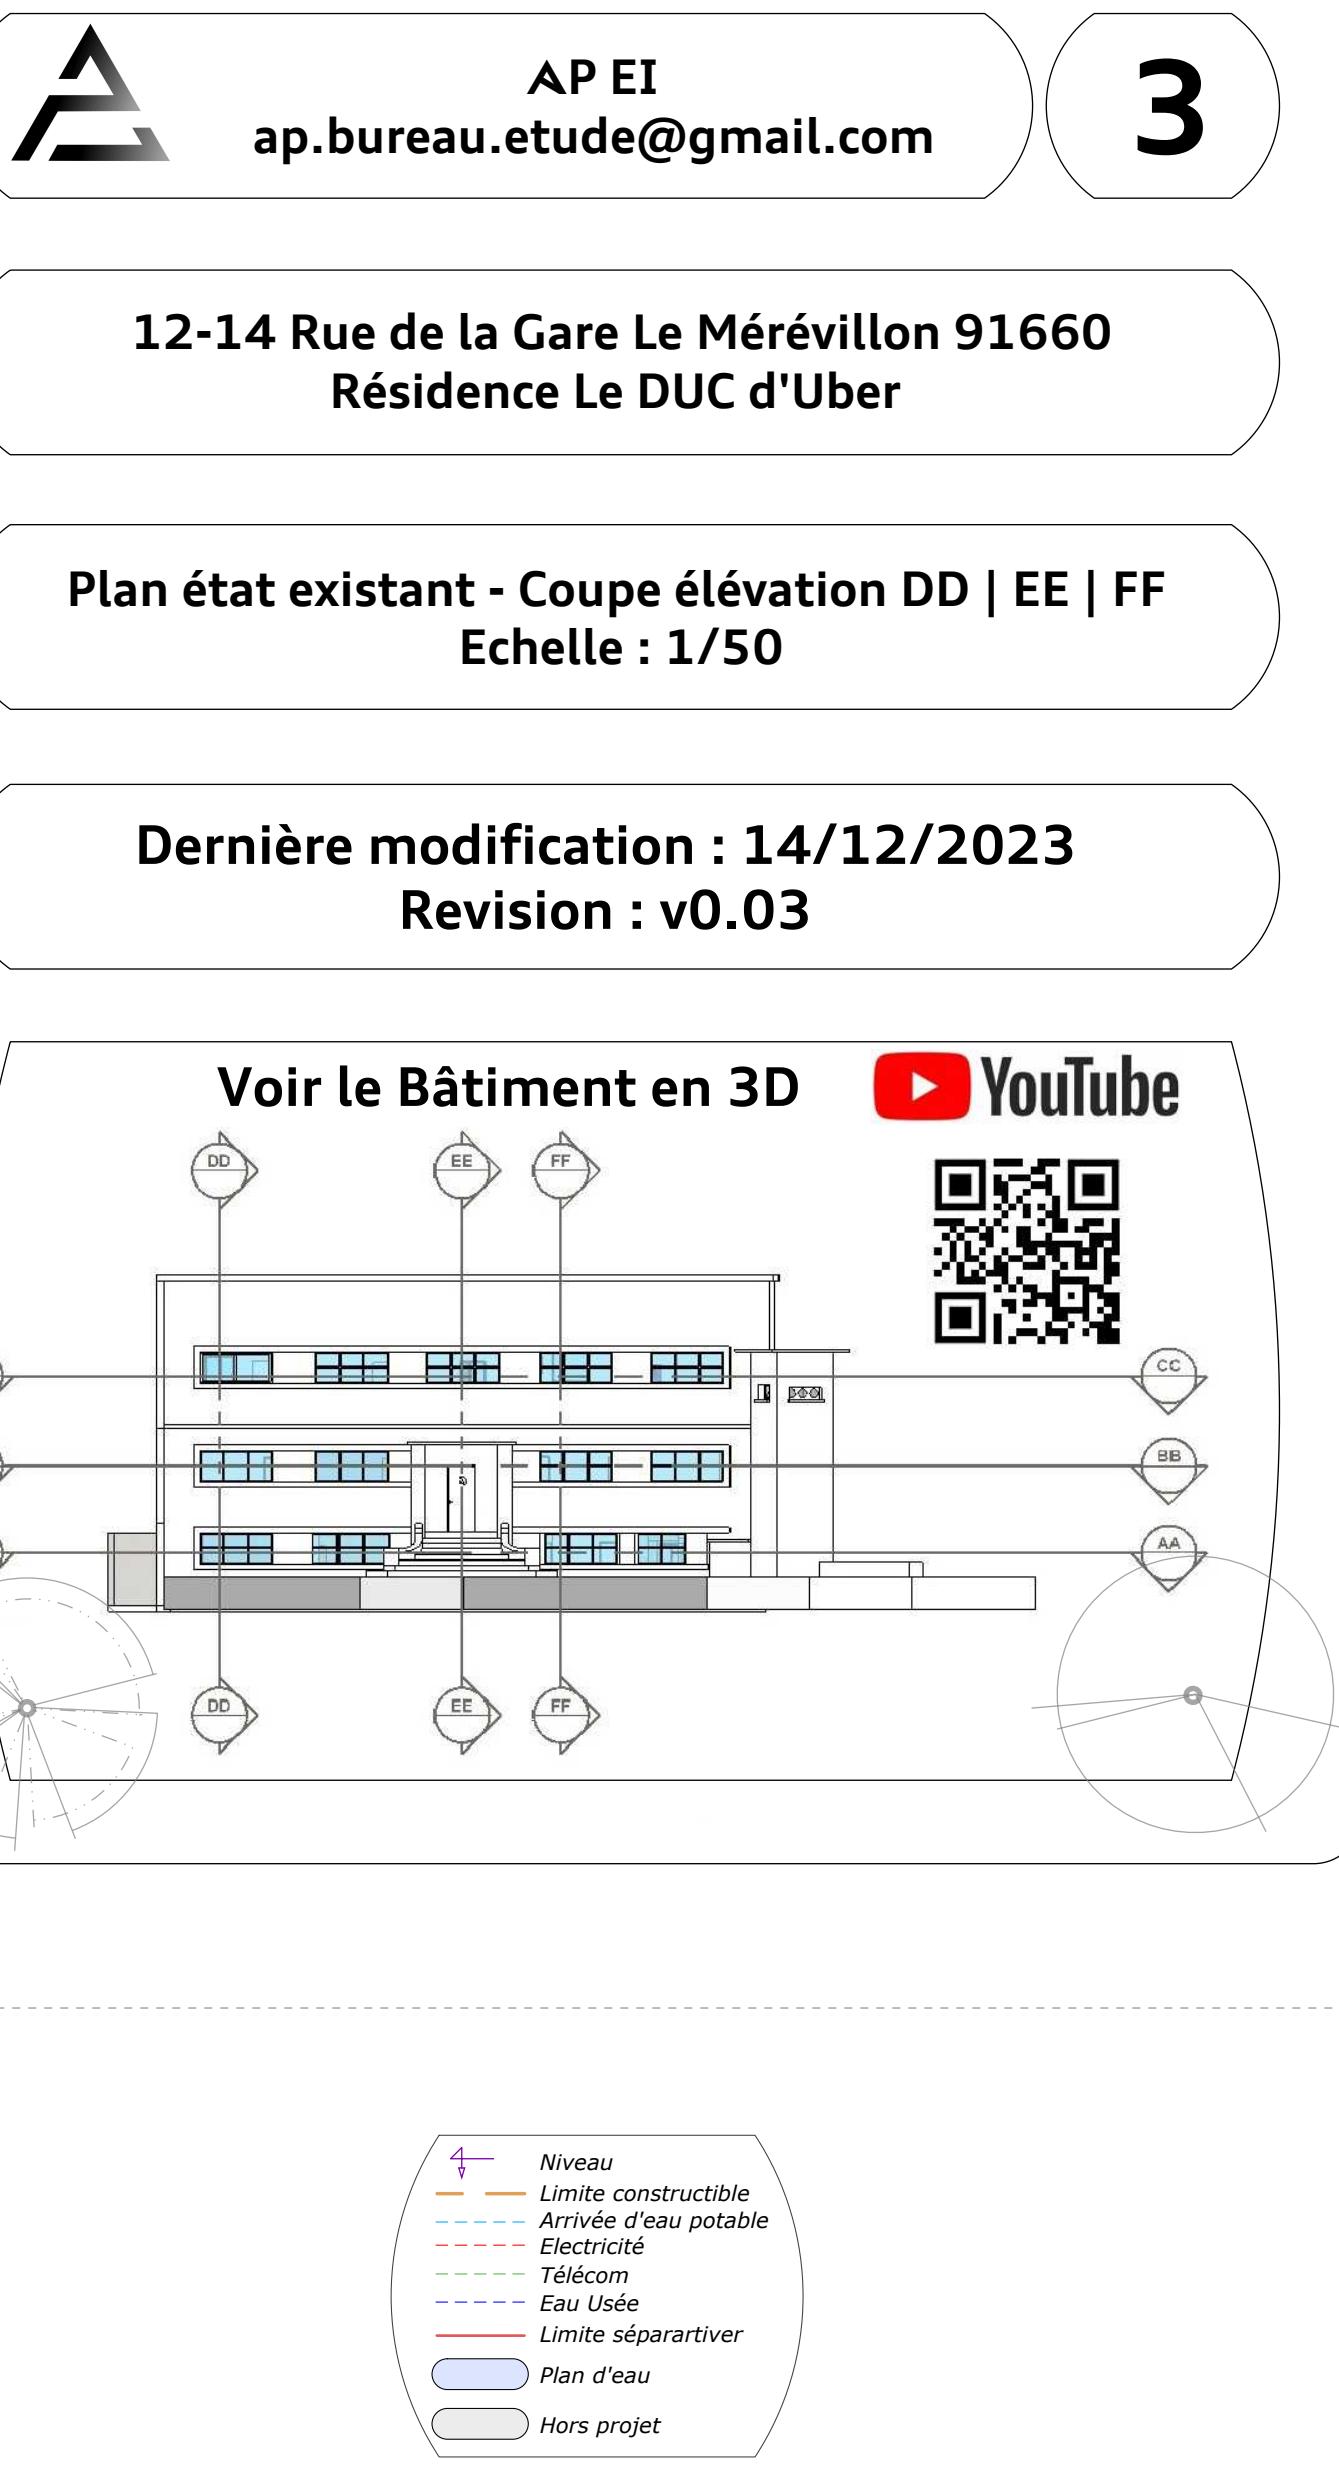

+8.00

+3.11

+0.00

-2.91